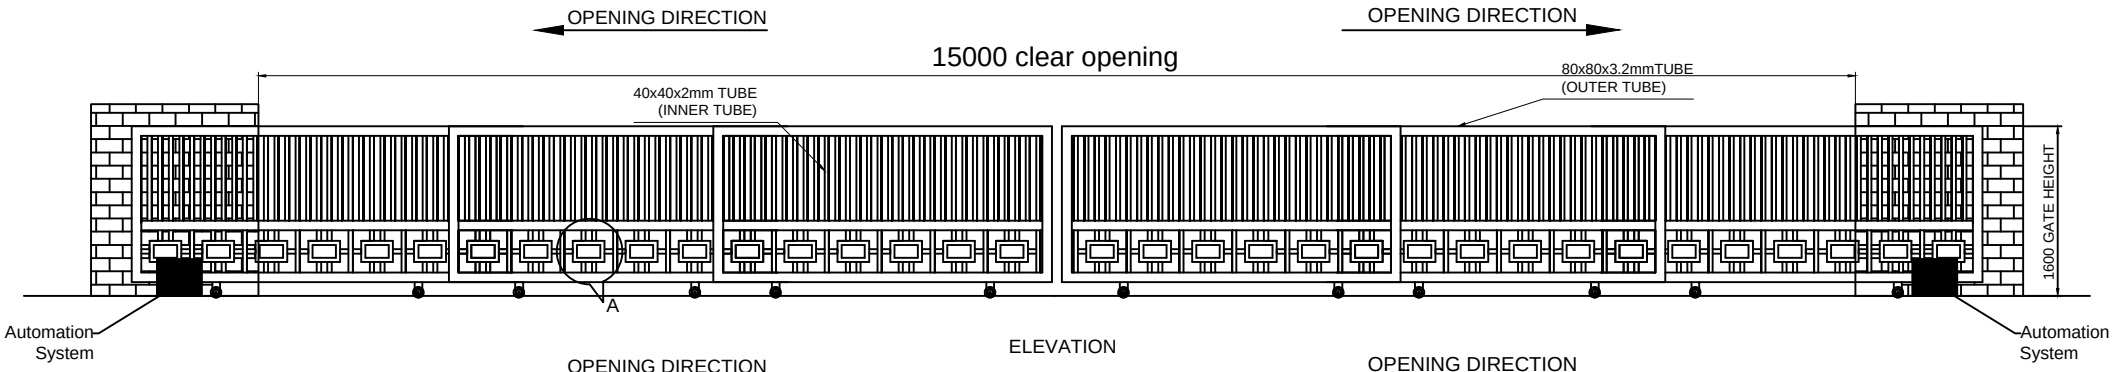

ELEVATION

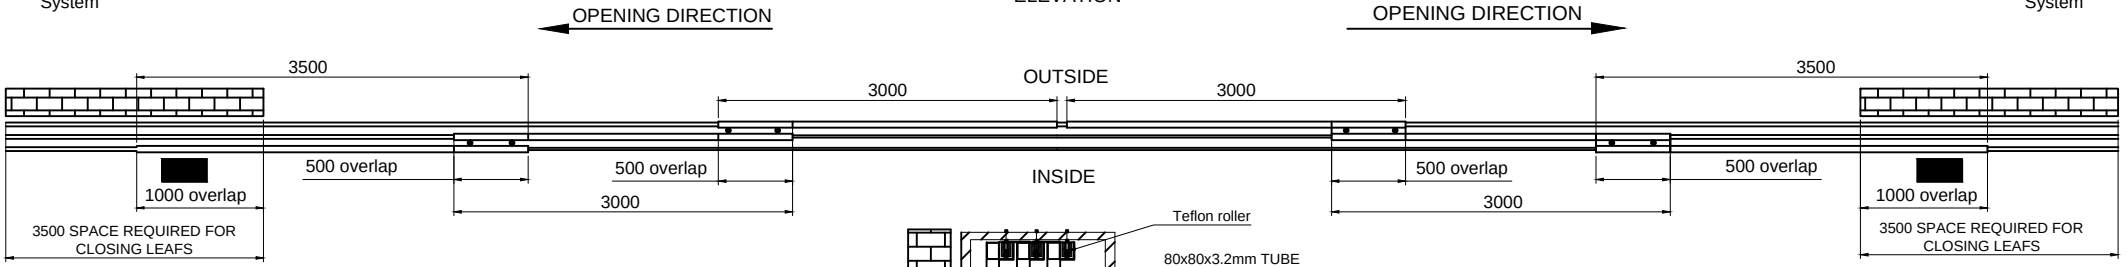

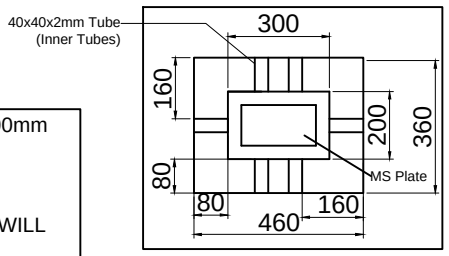

DETAILED VIEW OF A

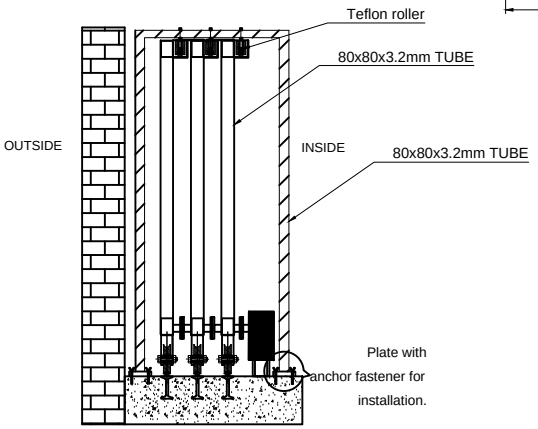

Clear Opening size -15000mm x 1600mm
Total No. of Leaf - 6 Leaf
Outer Tube Size-80x80x3.2mm
Inner Tube Size-40x40x2mm
NOTE :- *ALL REQ. CIVIL WORK WILL BE IN CLIENT SCOPE.

This drawing & designing is the property of NIHVA TECHNOLOGIES. Not be sold or copy to any other concern.

TITLE	TELESCOPIC SLIDING GATE	
	SIGN	DATE
DRAWN	OMKAR	23/03/16
CHECK	ANIL	23/03/16
REV.	01	
APPROVAL		
If any queries contact : projects@nihva.com		
ALL DIMENSION ARE IN mm		

NIHVA
NIHVA TECHNOLOGIES PVT. LTD.
NIHVA TECHNOLOGY
PVT. LTD. PUNE
Tel : 020 66304033
Email:- info@nihva.com
Website:- www.nihva.com

CLIENT -
PROJECT -
SITE -
DWG. NO. : NIHVA/15-16/
SCALE: 01 | WT: | SHEET: 01 OF 01