

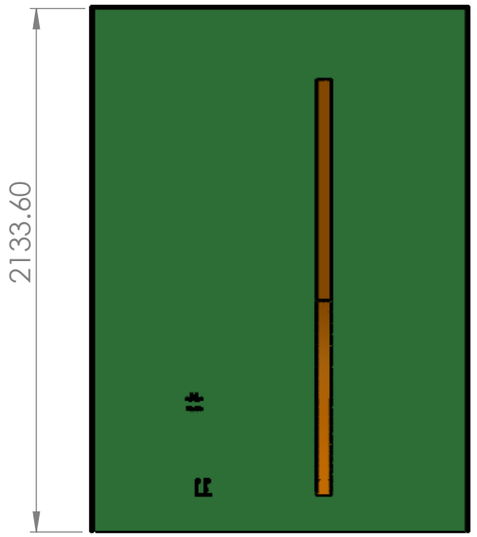


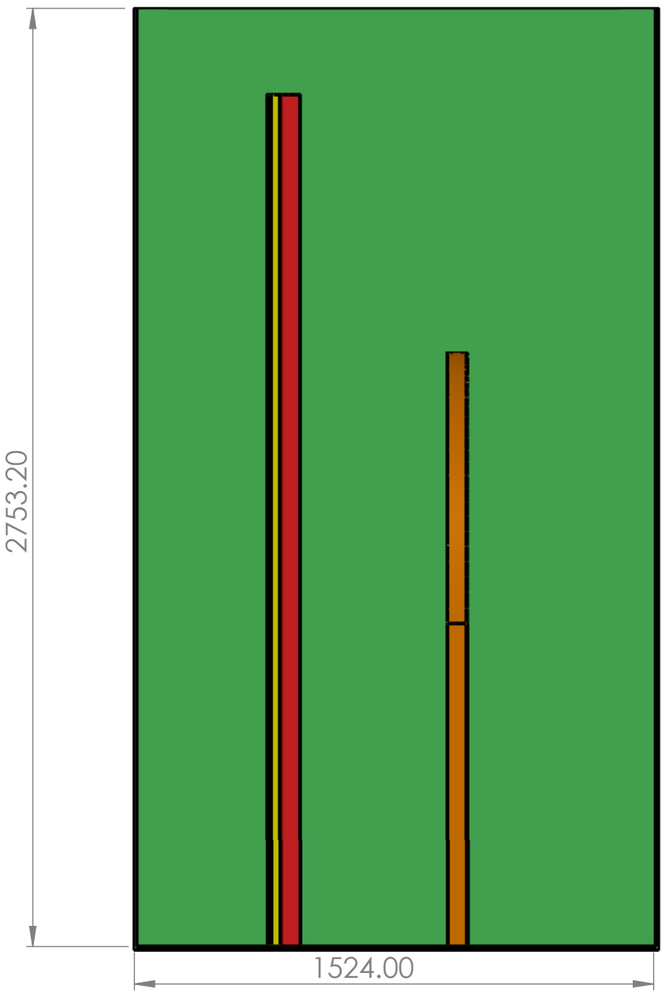


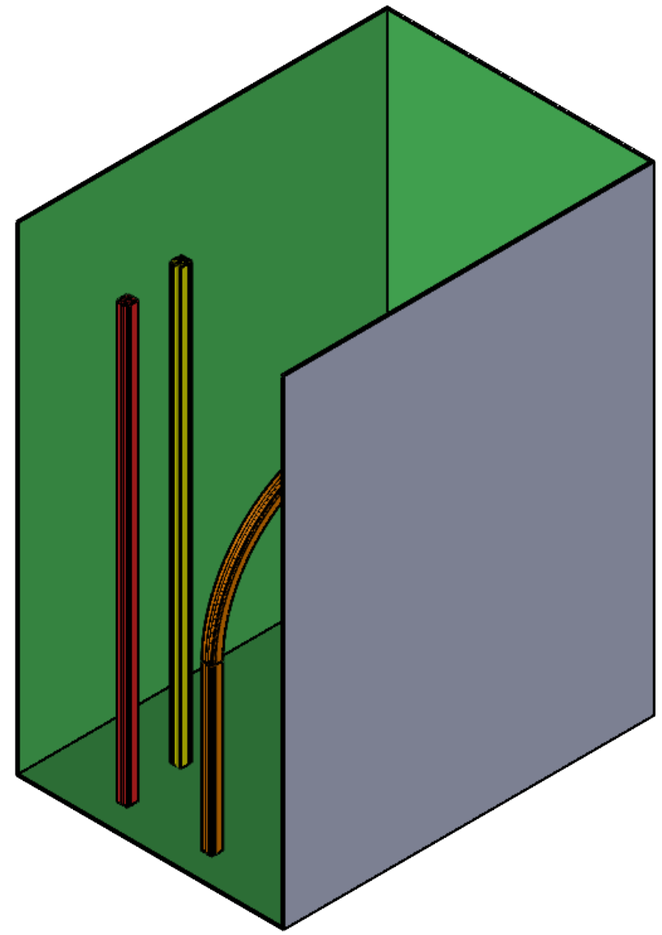


LIFT SIZE -
W-1524 MM
H-2753 MM
D-2133 MM


ASM DRAWING -
LIFT WITH MATERIAL

TITLE : CIVIL DRAWING			NIHVA Technologies Pvt. Ltd. NIHVA TECHNOLOGIES PVT LTD
	NAME	SIGNATURE	DATE
DRAWN	DNYANENDRA V.		11-02-2023
CHK'D	PRANAV M.		
APPV'D	VIJAY T.		
CLIENT NAME :	BEHEDE CONSTRUCTION		
PRODUCT NAME :	SHPERICAL DOME		
SITE LOCATION :	PUN E		
DWG NO.	NIHVA\22-23\00XX	A3	
		REVISION : 0	
	DIMENSIONS ARE IN MILLIMETERS	SCALE:	SHEET 1 OF 2

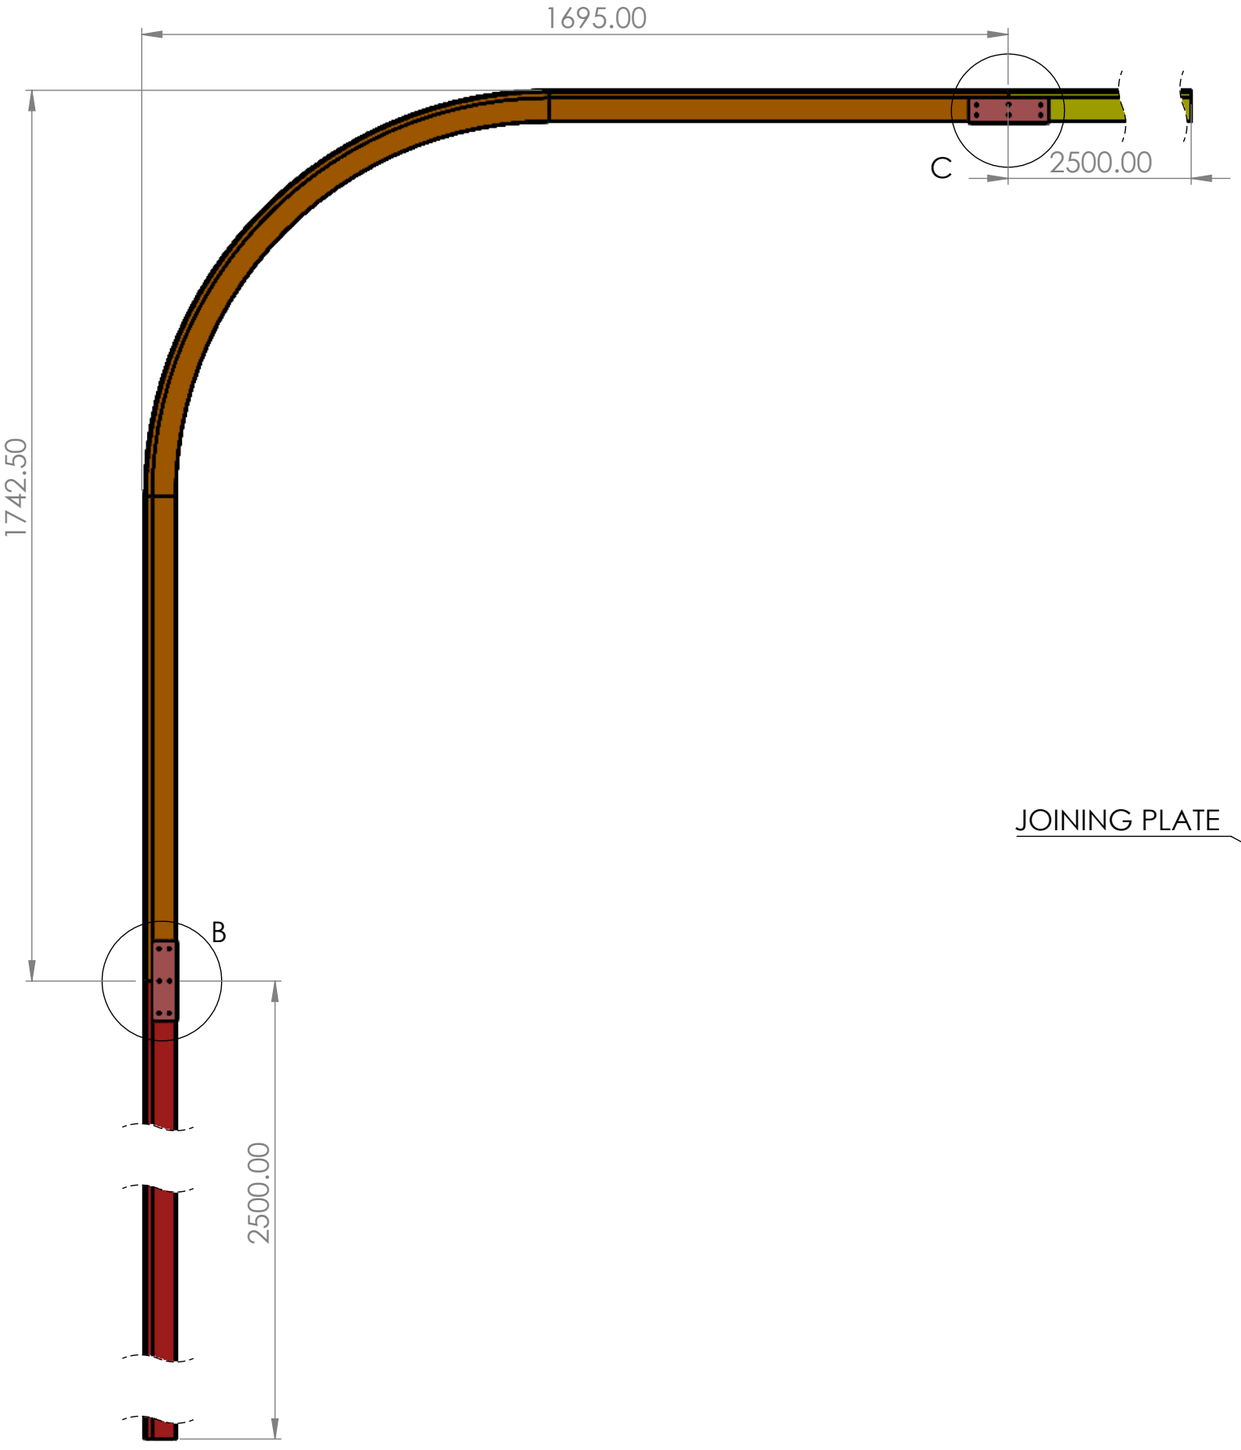

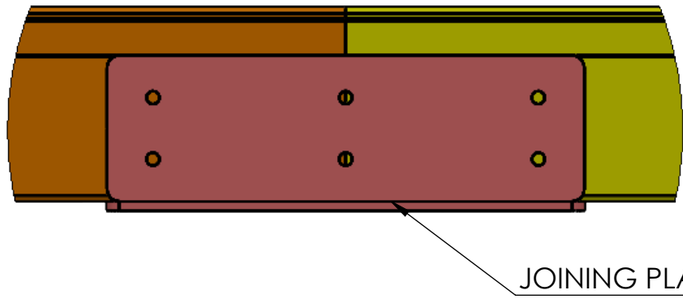

DETAIL C
SCALE 1 : 2

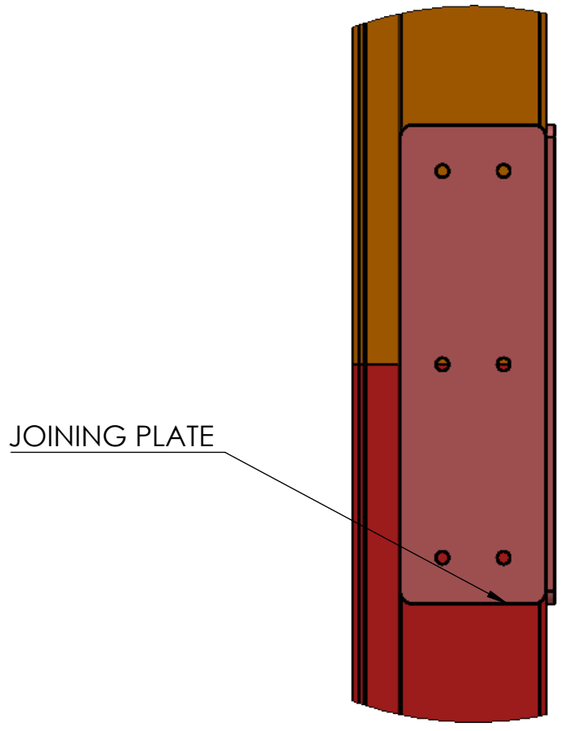

DETAIL B
SCALE 1 : 2

TITLE - BALCONY ENCLOSER				NIHVA TECHNOLOGIES PVT.LTD.PUNE Website - www.nihva.com
DWG NO - NTPL263-PM			QTY - 1	
	NAME	SIGNATURE	DATE	PROJECT NO - NTPL263-PM
DRAWN	S.W		30-01-2025	PRODUCT - BALCONY ENCLOSURE
CHK'D	P.M.		30-01-2025	SITE LOCATION - MUMBAI
APPV'D	V.T.		30-01-2025	
if any queries contact - supportautomation@nihva.com				REVISION -
ALL DIMENSION ARE IN mm			A3	SCALE - SHEET 2 OF 2