

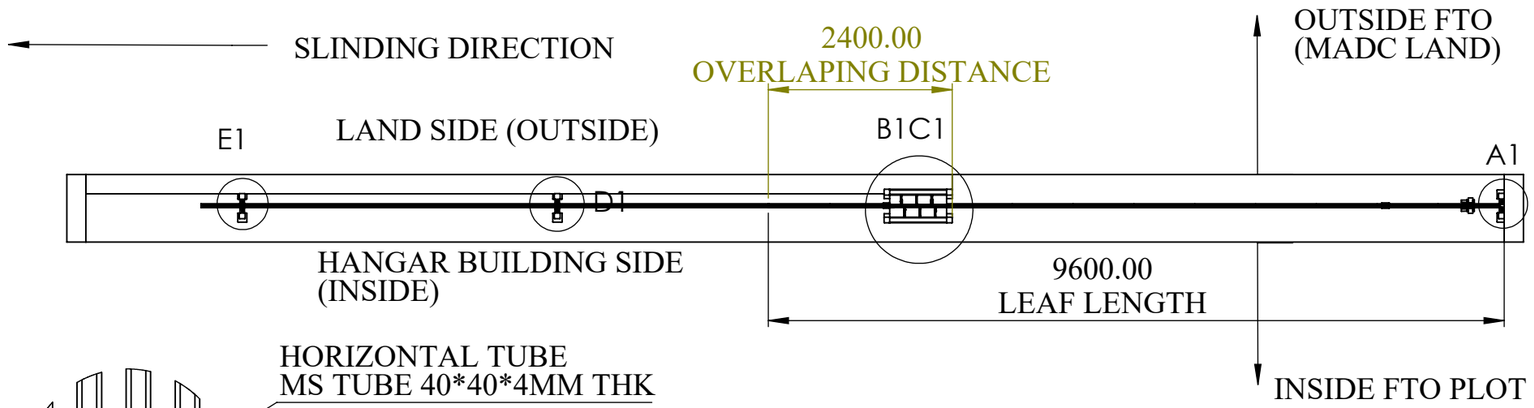


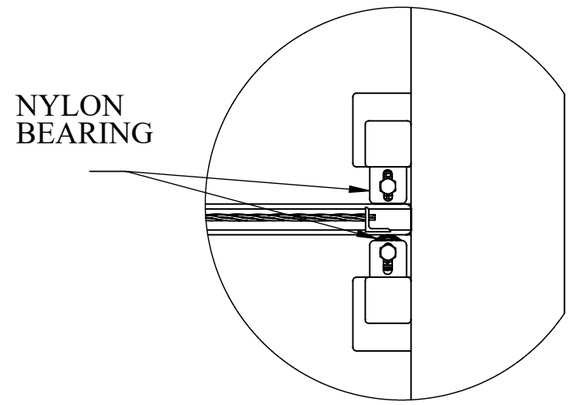



POST 1 AND NYLON
BEARING ASM

DETAIL A1
SCALE 1 : 10

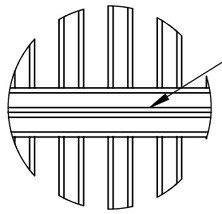


DETAIL E
SCALE 1 : 10

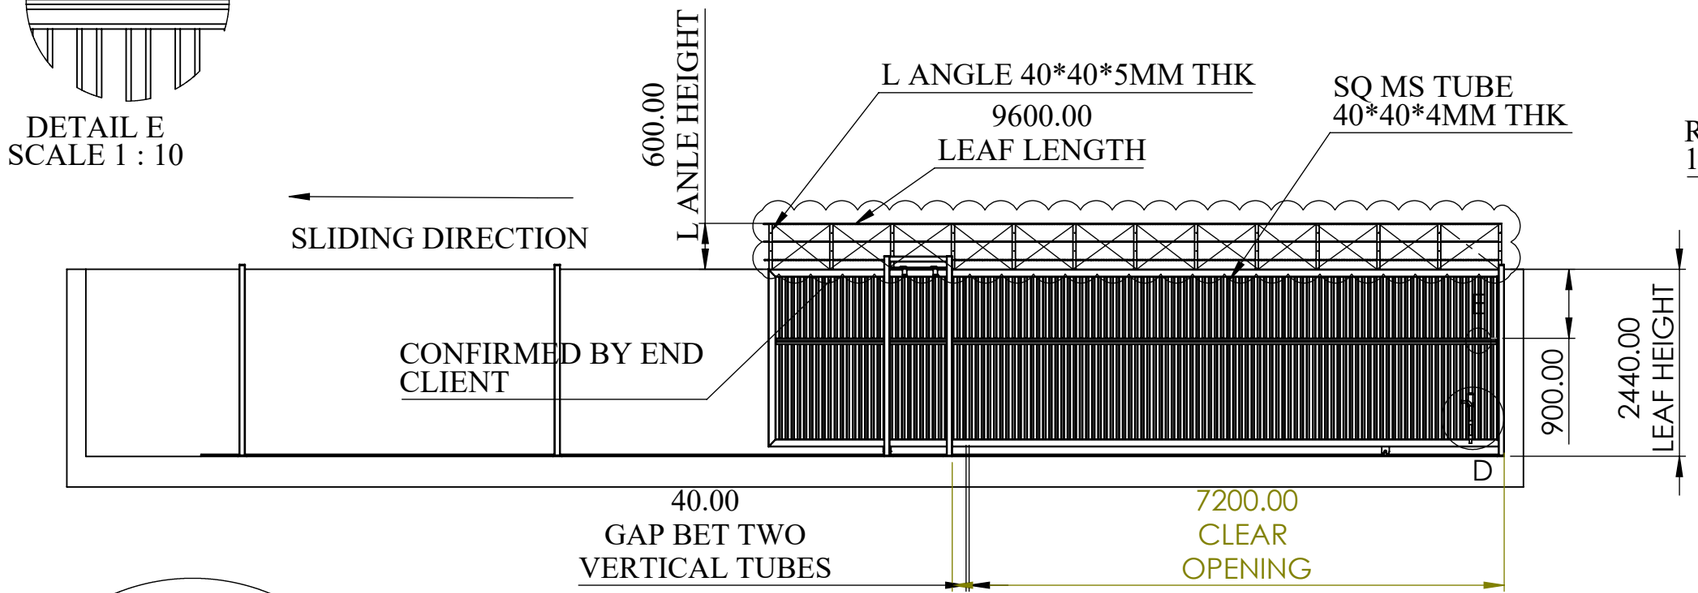

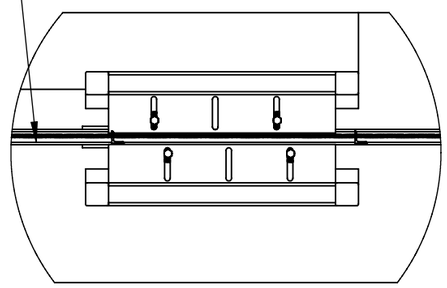


POST 2 AND NYLON
BEARING ASM

DETAIL B1C1
SCALE 1 : 20

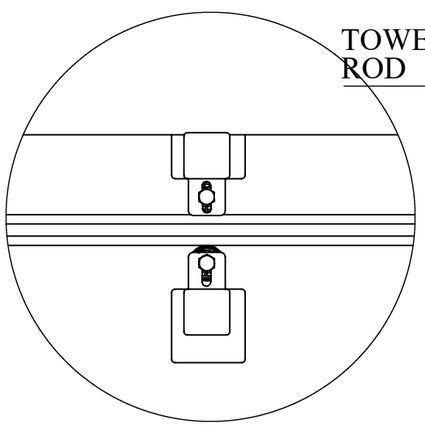


POST NO 4 &
NYLON ROLLER BERAING
ASM

DETAIL E1
SCALE 1 : 10

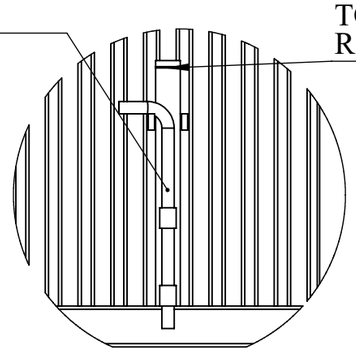

TOWER BOLT LOCKING
ARRANGEMENT.

DETAIL D
SCALE 1 : 15

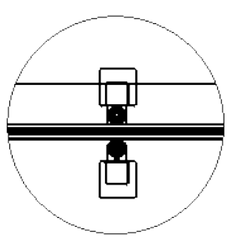

DETAIL D1
SCALE 1 : 20

POST NO 3 &
NYLON ROLLER BERAING
ASM

NOTE :

1)GA DRAWING TYPE NO 01

2)Total column -05 (A1,B1,C1,D1,E1)

3) 03 column posts when the gates is in the closed position.(A1,B1,C1)

4) 04 column posts when the gates is in the fully open position.(B1,C1,D1,E1)

5) barbed wire design is zigzag pattern.

TITLE - GATE AUTOMATIOM				NIHVA TECHNOLOGIES PVT.LTD.PUNE
DWG NO - NTPL-000-PM-001-00-00-00				Website - www.nihva.com
	NAME	SIGNATURE	DATE	PROJECT NO - NTPL-000-PM
DRAWN	V.W		21-05-2025	PRODUCT - SINGLE SLIDING GATE
CHK'D	S.W.		21-05-2025	SITE LOCATION -
APPV'D	V.T.		21-05-2025	
if any queries contact - supportautomation@nihva.com				REVISION - 01 / QTY - 1
ALL DIMENSION ARE IN mm		A3		SCALE / SHEET 1 OF 1