


DRAWING

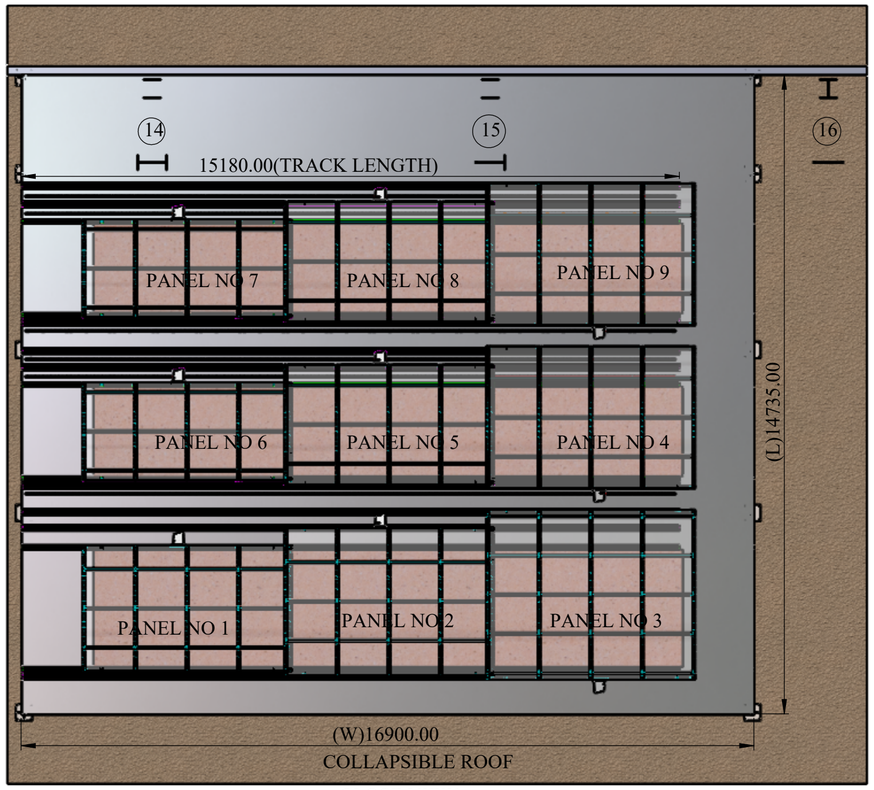



CLOSE VIEW

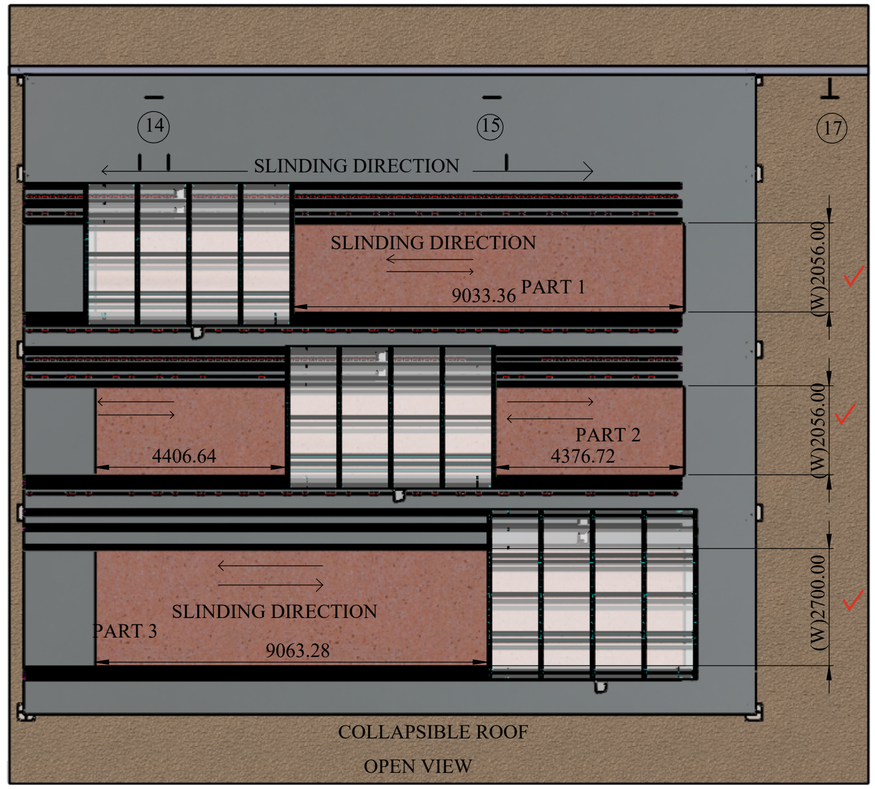


OPEN VIEW

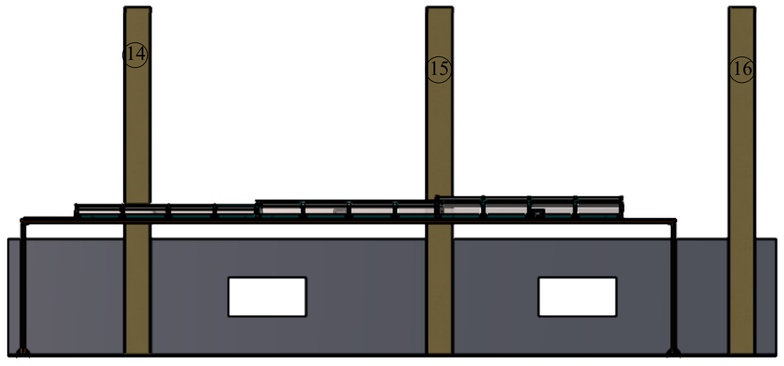

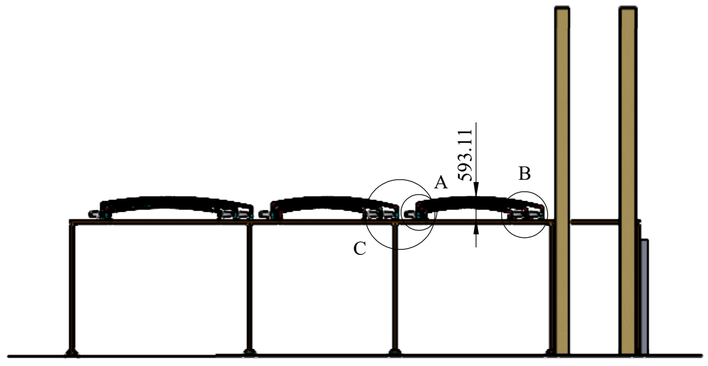


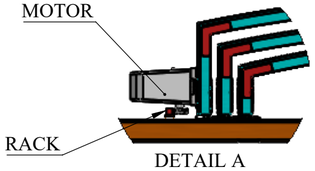

DETAIL A
SCALE 1 : 20

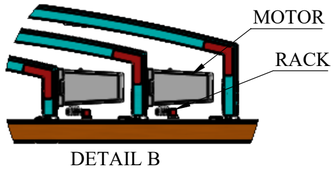

DETAIL B
SCALE 1 : 20

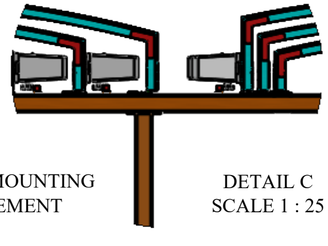

MOTOR MOUNTING ARRANGEMENT

DETAIL C
SCALE 1 : 25

REV DESCRIPTION	DATE	REV NO
	17-06-2026	REV 00
1. ROOF ORIENTATION CHANGES. ROOF SLINDING DIRECTION CHANGES.	22-06-2026	REV 01
2. CUTOUT WIDTH CHANGES.	04-07-2026	REV 02

This arrangement is OK .

So please proceed with this arrangement

Regards

P. Naresh Reddy

NOTE :

THIS DRAWING IS FOR CLIENT APPROVAL
BASE STRUCTURE IN CLIENT SCOPE

SPECIAL INSTRUCTION'S :

This drawing & design is the property of NIHVA TECHONOLOGIES PVT. LTD. Not to be sold or copied to any other concern

TITLE - COLLAPSIBLE CCA ROOF

DWG NO - NTPL-002-PM-05


NIHVA TECHNOLOGIES PVT.LTD.PUNE
Website - www.nihva.com


	NAME	SIGNATURE	DATE
DRAWN	V.W.		17-06-2026
CHK'D	S.P.		18-06-2026
APPV'D	V.T.		18-06-2026

PRODUCT - RETRACTABLE ROOF
CLIENT NAME - NEOTRAFO SOLUTIONS
SITE LOCATION - HYDRABAD
MATRIAL -
QTY - 1
If any queries contact - info@nihva.com
PROJECTION METHOD:
SCALE :
ALL DIMENSION ARE IN mm
A2

DRAWING

REV DESCRIPTION	DATE	REV NO
	17-06-2026	REV 00
1.		

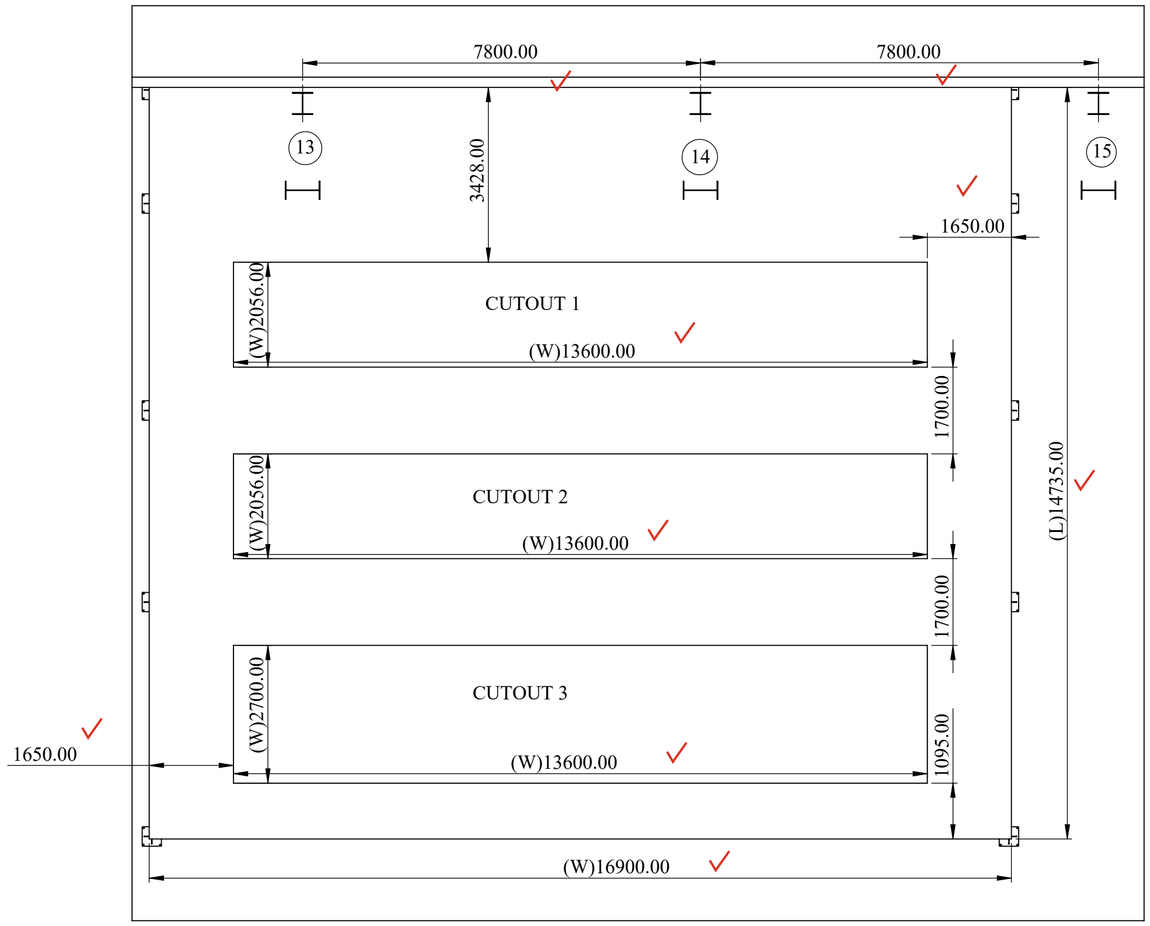

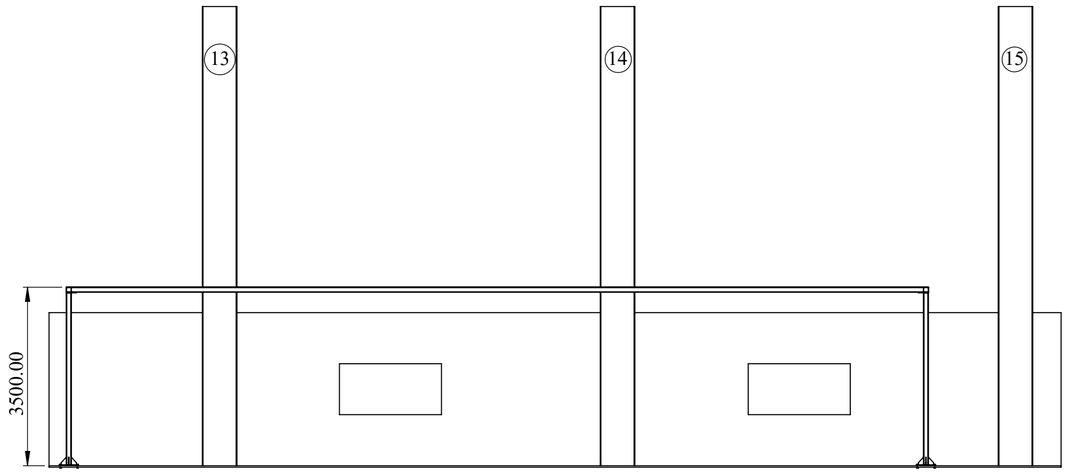

NOTE :

BASE STRUCTURE IN CLIENT SCOPE

SPECIAL INSTRUCTION'S :

This drawing & design is the property of NIHVA TECHONOLOGIES PVT. LTD. Not to be sold or copied to any other concern

TITLE - COLLAPSABLE CCA ROOF

DWG NO - NTPL-002-PM-05

NIHVA TECHNOLOGIES PVT.LTD.PUNE
Website - www.nihva.com

	NAME	SIGNATURE	DATE
DRAWN	V.W.		17-06-2026
CHK'D	S.P.		18-07-2026
APPV'D	V.T.		18-07-2026

PRODUCT - RETRACTABLE ROOF

CLIENT NAME - NEOTRAFO SOLUTIONS

SITE LOCATION - HYDRABAD

MATRIAL - QTY - 1

If any queries contact - info@nihva.com

ALL DIMENSION ARE IN mm A2

PROJECTION METHOD:

SCALE :