




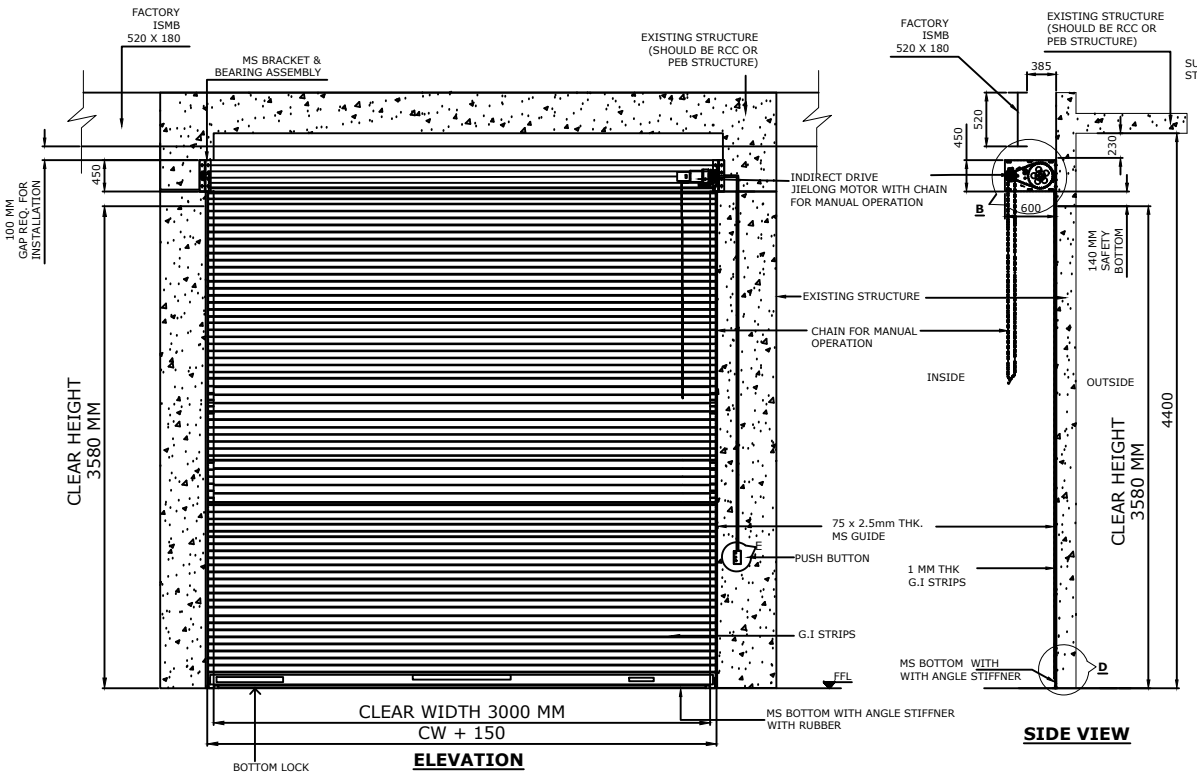


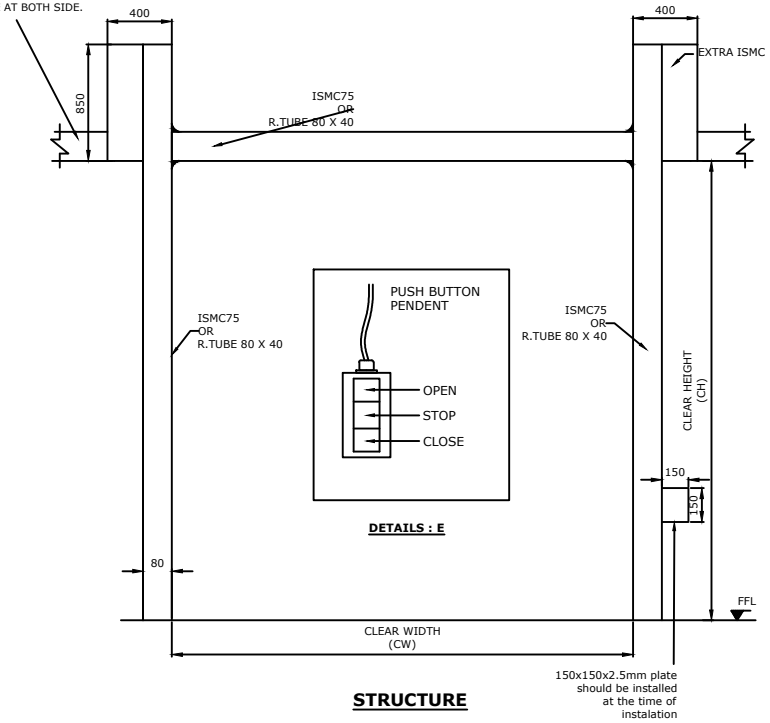


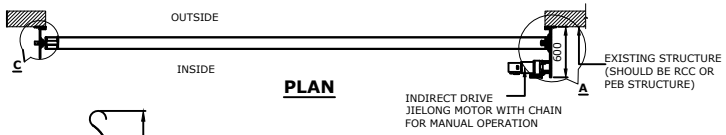

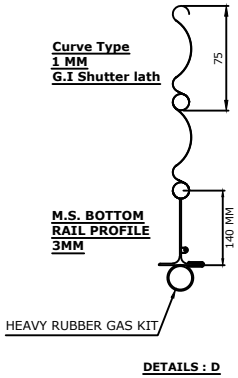

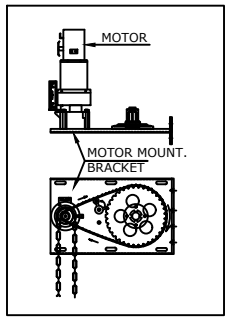

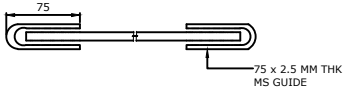

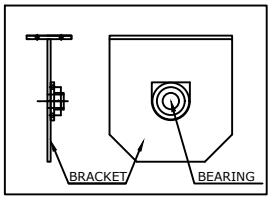

NOTE:
1.REQUIRED TECHNICAL STRUCTURE FOR SHUTTER IN CLIENT SCOPE.
2.RAL CODE WILL BE CONFIRM FROM CLIENT.

3000	3580	1	RAL -	
CLEAR WIDTH (CW)	CLEAR HEIGHT (CH)	QUANTITY	RAL COLOR	LOCATION

This drawing & design is the property of NIHVA TECHNOLOGIES. Not to be sold or copied to any other concern.

REV NO	DATE	DRAWN	REMARK
R01	20.05.20	P.A	1.CLEAR HEIGHT CHANGE

TITLE: MOTORIZED ROLLING SHUTTER

NIHVA TECHNOLOGIES PVT. LTD.
NIHVA TECHNOLOGIES PVT. LTD. PUNE
Tel : 020 66304033
Email:- info@nihva.com
Website:- www.nihva.com

	NAME	SIGN	DATE
DRAWN	P.A		18.03.2020
CHECK	G.J		18.03.2020
APPRD.			

CLIENT - MA ENGINEERING
PROJECT - JOHN DEERE
SITE LOCATION - SANASWADI, RANJANGAON
If any queries contact : design@nihva.com
DWG. NO. : NIHVA/19-20/0245/R01
REV- R01
ALL DIMENSION ARE IN mm
SCALE: NTS
WT:
SHEET: