

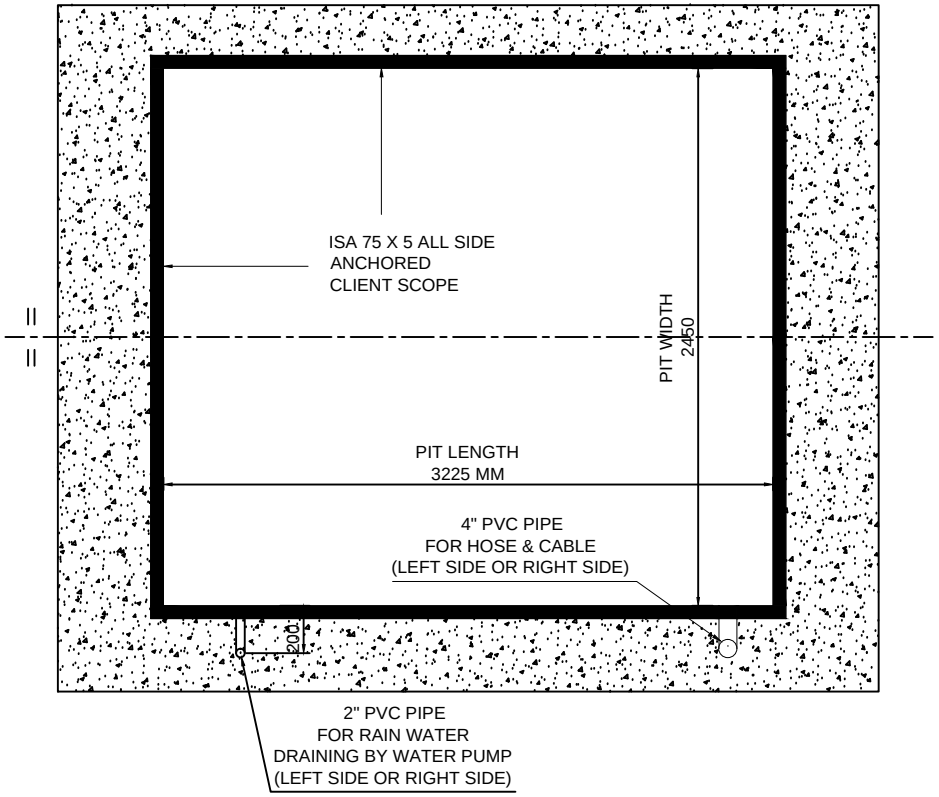


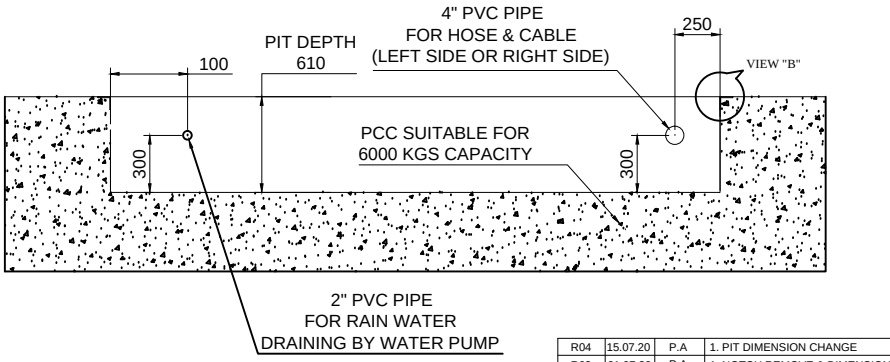

NOTE :

1. HYDRAULIC HOSE LENGTH : 12 MTR
2. ELECTRICAL CABLE : 12 MTR
3. PIT / CIVIL / PVC PIPE WILL BE IN CLIENT SCOPE.
4. COLOR : a. GOLDEN YELLOW.
   OR
   b. ULTRA MARINE BLUE.
5. INPUT SUPPLY : 3 PHASE 400 VOLT WITH NEUTRAL.
6. CLEAR PIT DIMENSIONS WITHOUT SKIRTING ISA 75 X 5 = 2460W X 3235L X 610H.

DETAILS B

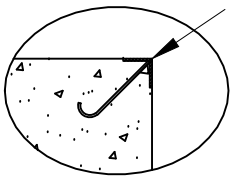

75x75x6 Angle -
Anchored in civil work
(Client scope)

REV NO	DATE	DRAWN	REMARK
R04	15.07.20	P.A	1. PIT DIMENSION CHANGE
R03	01.07.20	P.A	1. NOTCH REMOVE & DIMENSION CHANGE
R02	28.01.20	P.A	1. DETAILS ADDED.
R01	24.01.20	P.A	1. DRAIN ARRANGEMENT ADD

This drawing & design is the property of NIHVA TECHNOLOGIES. Not to be sold or copied to any other concern.

TITLE: ELECTRO HYDRAULIC SCISSOR LIFT PIT DRG

NIHVA TECHNOLOGIES PVT. LTD.
NIHVA TECHNOLOGIES PVT. LTD. PUNE
Tel : 020 66304033
Email:- info@nihva.com
Website:- www.nihva.com

	NAME	SIGN	DATE
DRAWN	P.V.A		15.11.2019
CHECK	V.M.T		15.11.2019
APPRD.			

CLIENT - IKEA
PROJECT -
SITE LOCATION - MUMBAI
If any queries contact : design@nihva.com
DWG. NO. : NIHVA/19-20/0153/R04
REV- R04
ALL DIMENSION ARE IN mm
SCALE: NTS
WT:
SHEET: 01 OF 01