
Abbrevation's:
WOW-Wall Opening Width
WOH-Wall Opening Height
UC-Under Cut
FFL-Finished Floor Level

ASSESORIES DETALES


(a) HINGES:
(b) PANIC BAR:
(c) DOOR CLOSER: 2 NOS.
(d) GLASS:Clear fire Vision Glass Clear 6mm of size 300x300mm.

Shutter thickness : 47 mm
Frame Sheet thick : 1.20mm
Shutter sheet thick : 0.80mm
Fixing : On Soliid Brick plasterd wall with Anchors


NOTE:- *All Dimensions are in mm.
*Tolerance:-All Linear Dimensions ±3mm,Others ±0.5mm.
*The Drawing Is For Location of Hardware only. Drawing Does Not Represent The Hardware For More Clarity, Please Go Through Hardware Broucher.

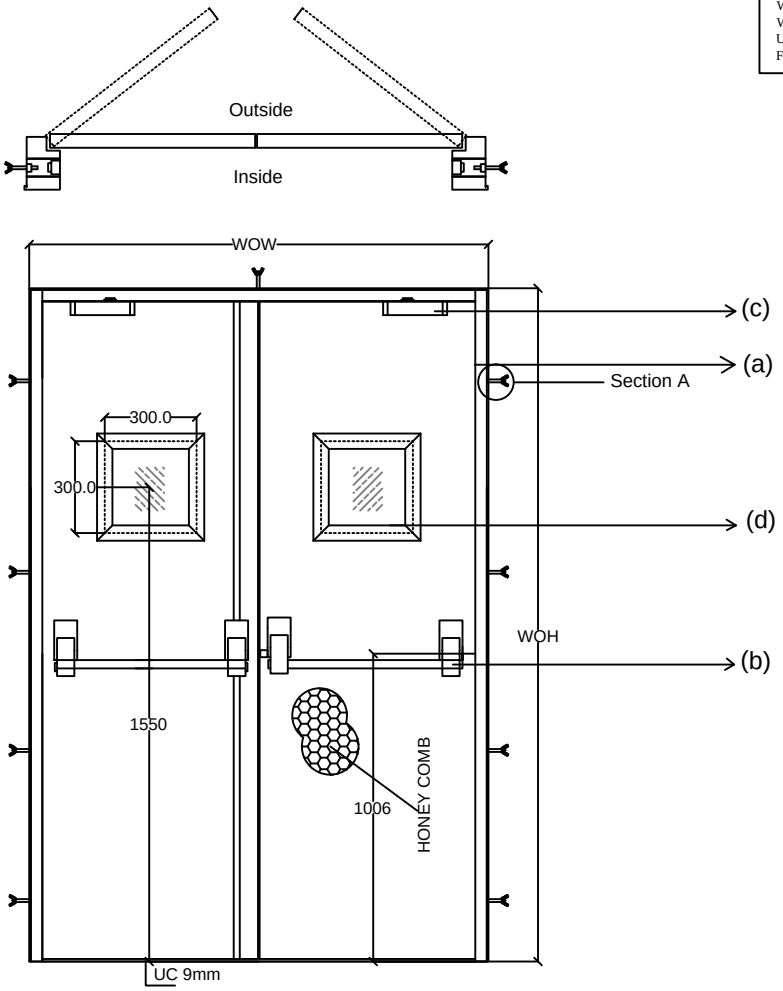

Inside Elevation

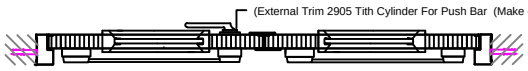

Top View

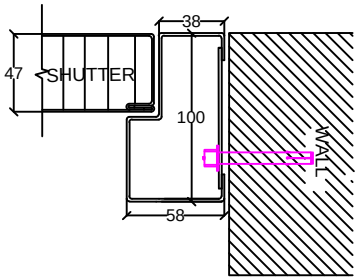

Detail view of Section A

NOTE-
1. CLIENT SHOULD SELECT DOOR TYPE FROM ATTACHED DOOR HANDLING SHEET & COLOR OF DOOR.
2. THIRD PARTY FIRE RATED CERTIFICATE.

FIRE DOOR SIZES			
WOW	WOH	QUANTITY	LOCATION
2000	2100	1	

This drawing & designing is the property of NIHVA TECHNOLOGIES. Not to be sold or copied to any other concern.

TITLE: STEEL DOOR

	NAME	SIGN	DATE
DRAWN	P.V.A		06.03.19
CHECK	V.M.T		06.03.19
APPROVAL			
MFG.			

If any queries contact : projects@nihva.com
ALL DIMENSION ARE IN mm

NIHVA TECHNOLOGIES PVT. LTD.
NIHVA TECHNOLOGIES PVT. LTD. PUNE
Tel : 020 66304033
Email:- info@nihva.com
Website:- www.nihva.com

CLIENT-
PROJECT -
SITE -.
DWG. NO. : NIHVA/18-19/VDR/414 REV. : 00
SCALE: NTS WT: SHEET: 01 OF 01