




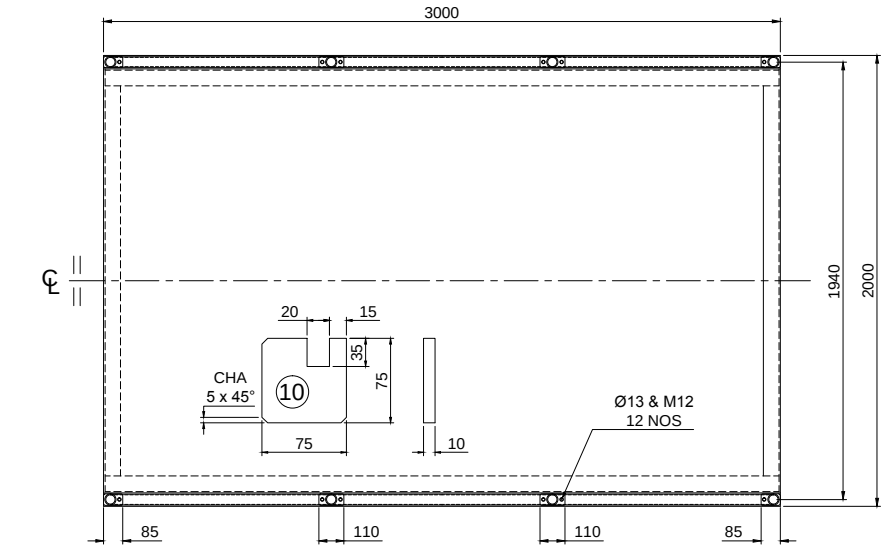


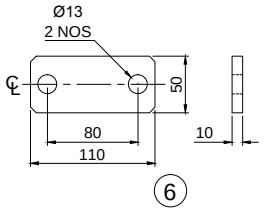


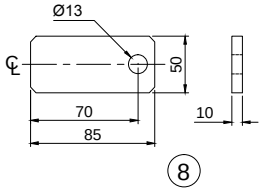


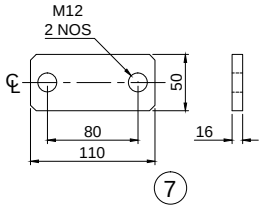

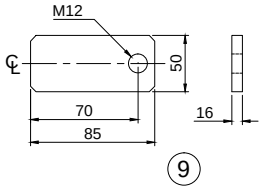

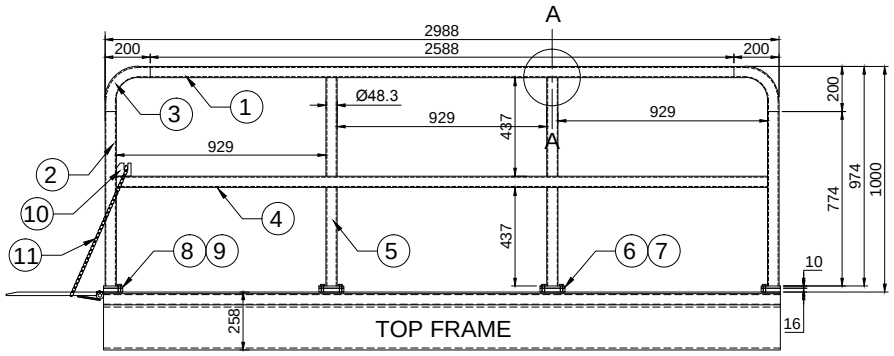

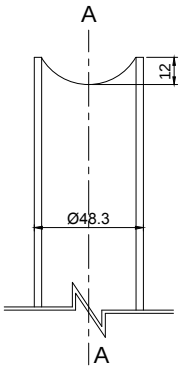

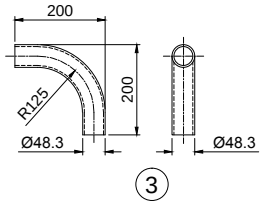

SR NO	PART NAME	SPECIFICATION	QTY	SR NO	PART NAME	SPECIFICATION	QTY
01	ERW PIPE	OD 48.3 X 3.25 THK X 2588L	2 NOS	07	M.S FLAT	50 X 16 X 110L	4 NOS
02	ERW PIPE	OD 48.3 X 3.25 THK X 774L	4 NOS	08	M.S FLAT	50 X 10 X 85L	4 NOS
03	ELBOW PIPE	OD 48.3 X 3.25 THK X 200L	4 NOS	09	M.S FLAT	50 X 16 X 85L	4 NOS
04	ERW PIPE	OD 48.3 X 3.25 THK X 2890L	2 NOS	10	M.S FLAT	75 X 10 X 75L	2 NOS
05	ERW PIPE	OD 48.3 X 3.25 THK X 450L	8 NOS	11	PLATED CHAIN	DIA 8 X 1000 MM	2 NOS
06	M.S FLAT	50 X 10 X 110L	4 NOS				

This drawing & design is the property of NIHVA TECHNOLOGIES. Not to be sold or copied to any other concern.

TITLE

RAILING ASSLY & DETAILS

NIHVA TECHNOLOGIES PVT. LTD.
NIHVA TECHNOLOGIES PVT. LTD. PUNE
Tel : 020 66304033
Email:- info@nihva.com
Website:- www.nihva.com

	NAME	SIGN	DATE
DRAWN	P.A		19.11.2018
CHECK	R.D		19.11.2018
APPRD.	V.T		19.11.2018

CLIENT -

PROJECT -

SITE LOCATION -

If any queries contact : design@nihva.com

DWG. NO. : NIHVA/18-19/MFG/NSL1002/09 | REV- 0

ALL DIMENSION ARE IN mm | SCALE: NTS | WT: | SHEET: 01 OF 01