

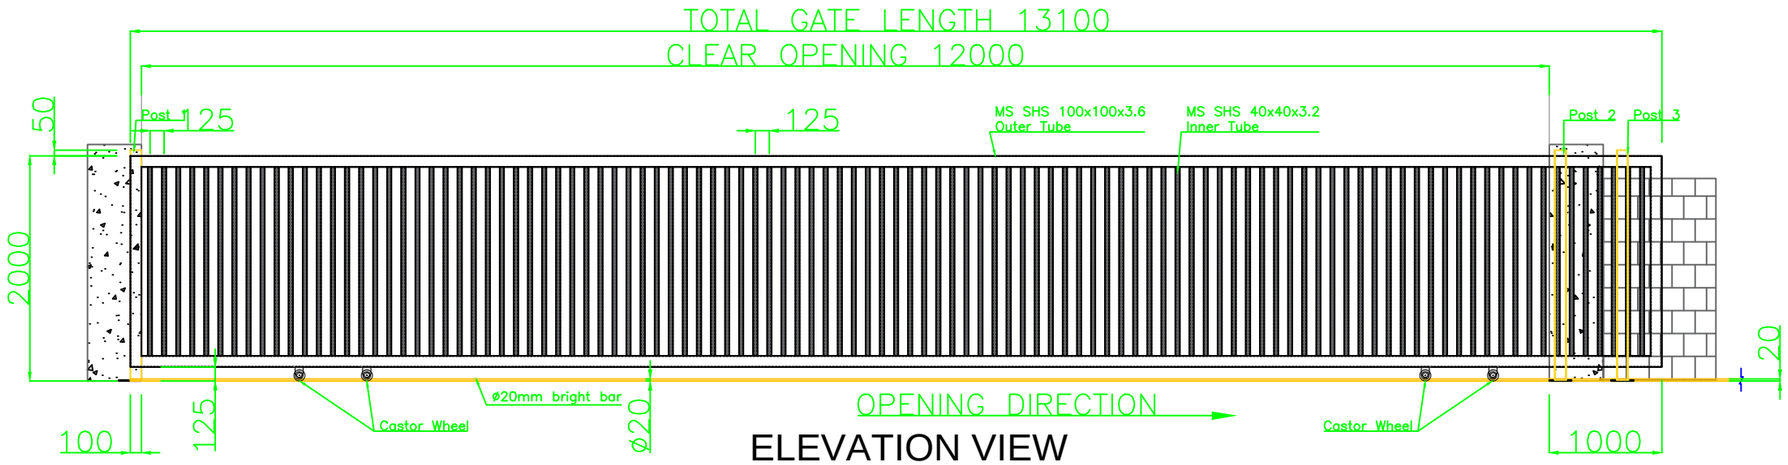



ELEVATION VIEW

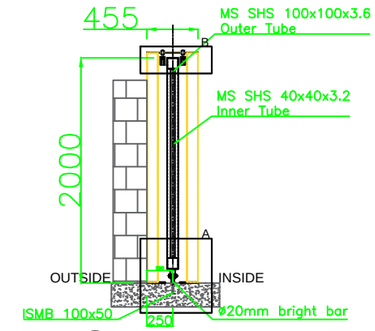


SIDE VIEW

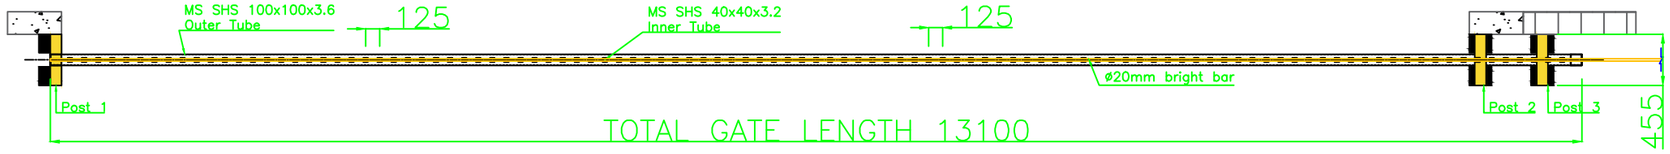

PLAN

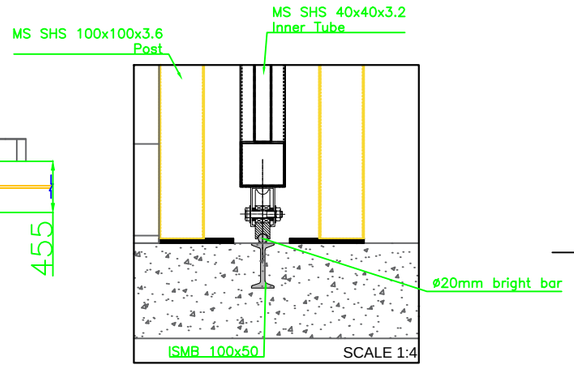

DETAIL A

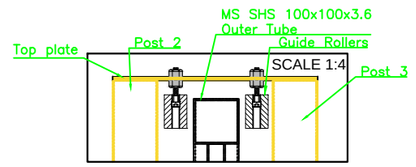

DETAIL B

Note-

1. All dimension are in mm.
2. All civil work is under client scope.


Technical Specs of Motorized Sliding Gate

1. Opening length - 12000mm
2. Gate Height - 2000mm
3. Parking length required - 13100mm
4. Outer tube size - MS SHS 100x100x3.6mm
5. Inner tube size - MS SHS 40x40x3.2mm
6. Pitch between tube - 125mm
7. Bottom Rail - Bright bar Ø20mm
8. Post size - MS SHS 100x100x3.6mm
9. Total leaf weight ≈1100 kg


This drawing & design is the property of NIHVA TECHNOLOGIES. Not to be sold or copied to any other concern.

TITLE				
MANUAL SLIDING GATE				
	NAME	SIGN	DATE	
DRAWN	G.P.		25.12.21	CLIENT -M/s FUJI SILVERTECH CONCRETE P. LTD.
CHECK	A.K.		25.12.21	LOCATION - AURANGABAD
APPRD.	V.T.		25.12.21	PRODUCT - MANUAL SLIDING GATE
If any queries contact : projectsautomation@nihva.com				NIHVA\21-22\CLT\0292 / REV- 0
ALL DIMENSION ARE IN mm				SCALE: NTS / SHEET: 01 OF 01

NIHVA TECHNOLOGIES PVT. LTD.
NIHVA TECHNOLOGIES PVT. LTD. PUNE
Tel : 020 66304033
Email:- info@nihva.com
Website:- www.nihva.com

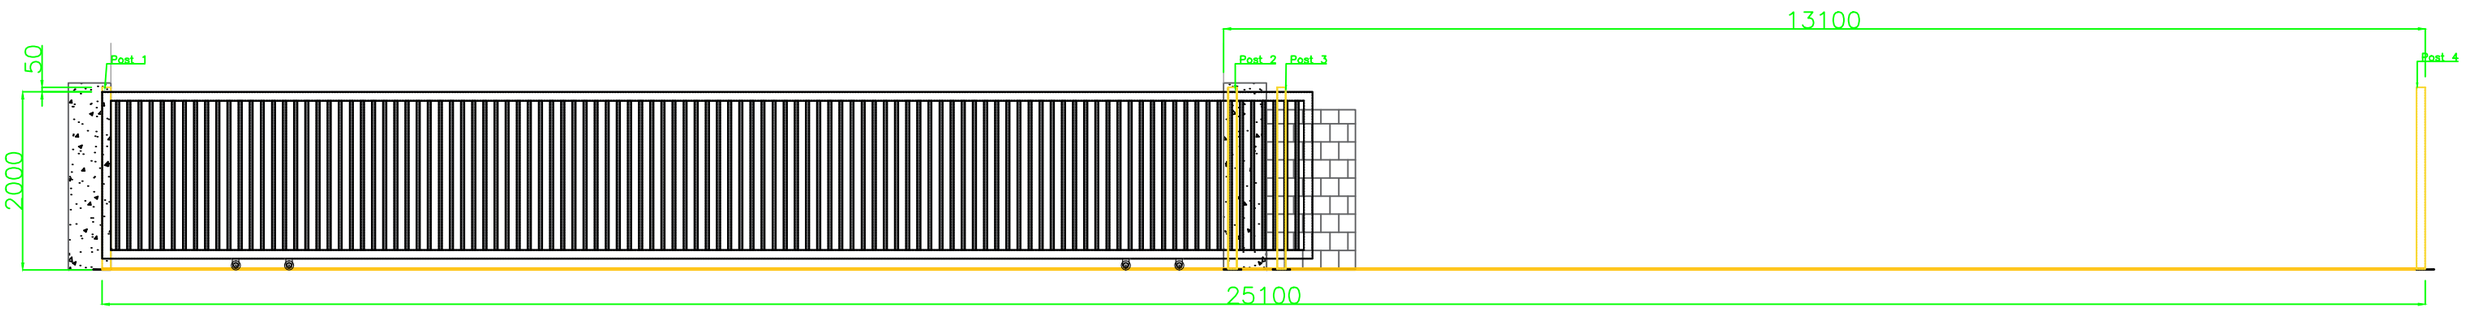

CLOSED GATE ELEVATION

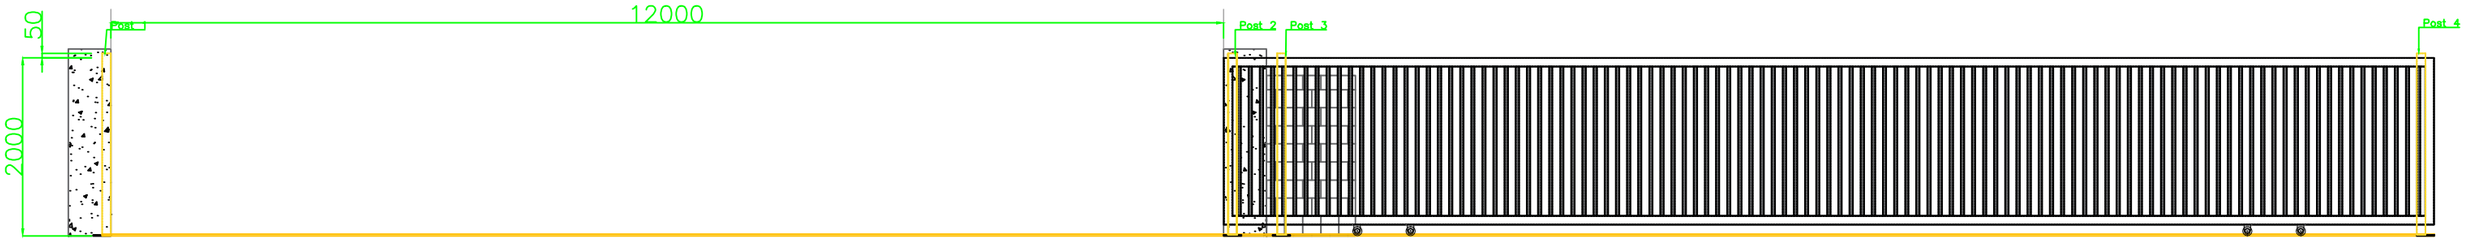

STACKED GATE ELEVATION