


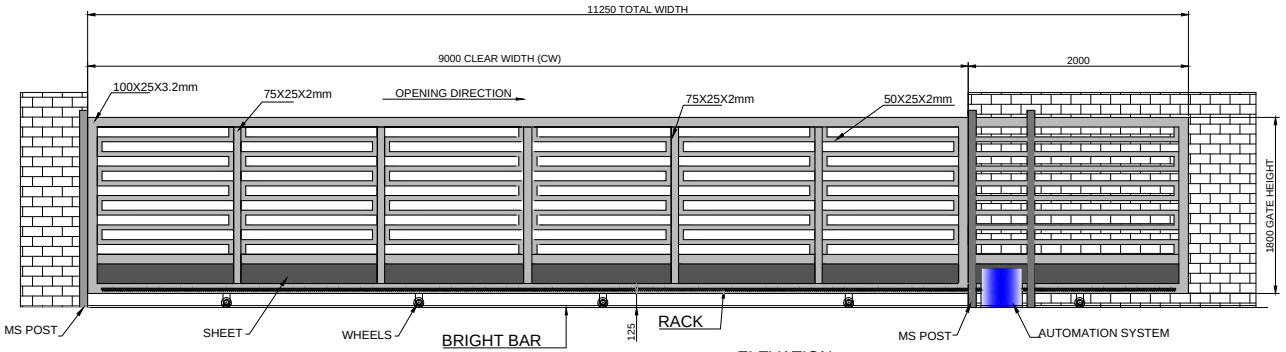


ELEVATION

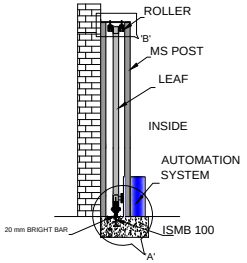


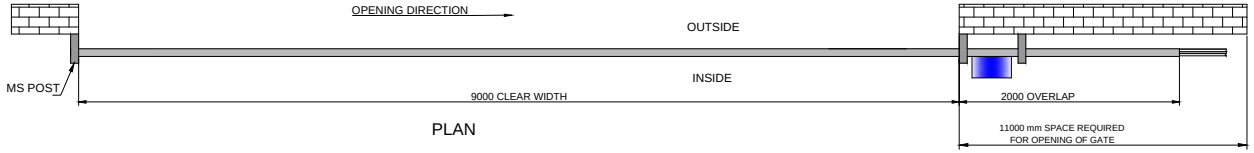

PLAN

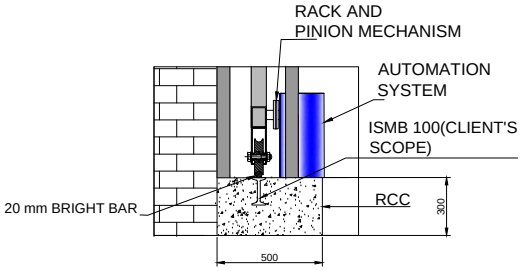

DETAIL VIEW OF A

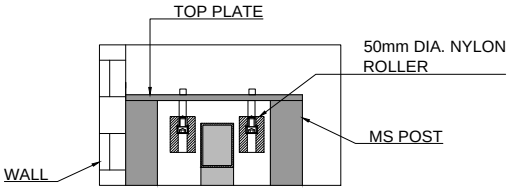

DETAIL VIEW OF B

SR NO	TUBE SPECIFICATION	
1	100X25X3.2mm	OUTER FRAME
2	50X25X2mm	INNER PATTERN
3	75X25X2mm	INNER PATTERN
4	400 X 14GAUGE	MS SHEET

CLEAR WIDTH (CW)	CLEAR HEIGHT (CH)	QUANTITY
9000mm	1800mm	1 NOS

DIMENSION :

CLEAR WIDTH	CLEAR HEIGHT	QUANTITY
9000mm	1800mm	1 NOS

MATERIAL:

THICKNESS :

NOTE-
1. ALL REQUIRED CIVIL WORK WILL BE IN CLIENTS SCOPE.

NIHVA TECHNOLOGIES PVT. LTD.
NIHVA TECHNOLOGIES PVT. LTD. PUNE
Email:- info@nihva.com
Website:- www.nihva.com

TITLE:

AUTOMATIC SINGLE LEAF SLIDING GATE

CLIENT'S APPROVAL :

CLIENT - SHILCHAR TECHNOLOGIES LTD.

PROJECT -

SITE LOCATION -VADODARA

DWG. NO. : NIHVA/17-18/0157

SCALE: NTS	WT:	SHEET:1 OF 1
DRAWN BY: SURAJ		DATE: 21-08-2017
CHECK BY : SAGAR P		DATE: 21-08-2017
APPROVED BY :SHEKHAR		DATE: 21-08-2017

If any queries contact : projects@nihva.com

NOTE: ALL DIMENSIONS ARE IN mm

THIS DRAWING & DESIGN IS THE PROPERTY OF NIHVA TECHNOLOGIES. NOT TO BE SOLD OR COPIED TO ANY OTHER CONCERN.