
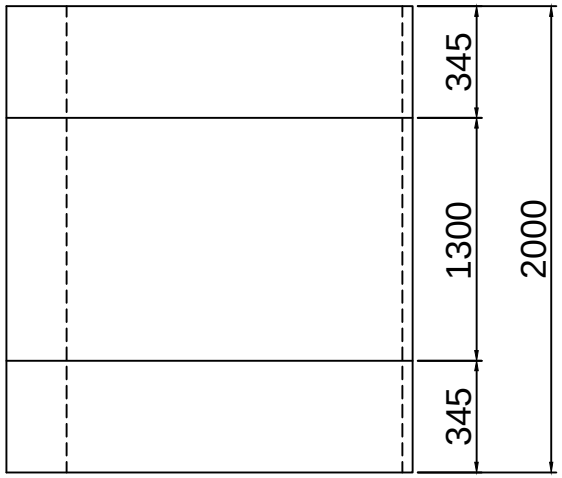


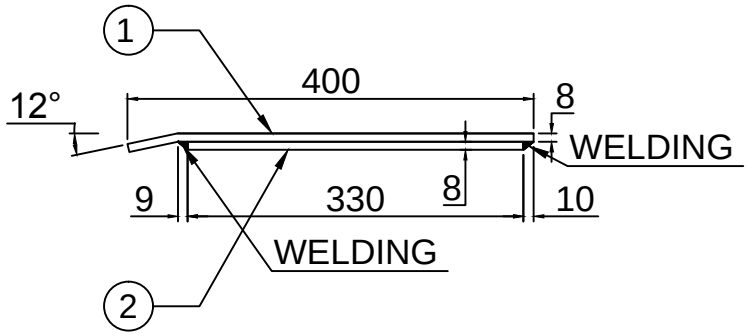

1. CHEQ. SHEET 400 X 8 THK X 2200L = 3 NOS
2. CHEQ. SHEET 330 X 8 THK X 2200L = 3 NOS

This drawing & design is the property of NIHVA TECHNOLOGIES. Not to be sold or copied to any other concern.

TITLE				
LIP PLATE DRG				
	NAME	SIGN	DATE	
DRAWN	PRADEEP		05.09.2018	CLIENT -
CHECK	PRADEEP		05.09.2018	PROJECT - DLSD1009
APPRD.	PRADEEP		05.09.2018	SITE LOCATION -
If any queries contact : design@nihva.com				DWG. NO. : NIHVA/18-19/MFG/DLSD1009/007
ALL DIMENSION ARE IN mm				SCALE: NTS / WT: / REV- 00

NIHVA TECHNOLOGIES PVT. LTD.
NIHVA TECHNOLOGIES PVT. LTD. PUNE
Tel : 020 66304033
Email:- info@nihva.com
Website:- www.nihva.com