
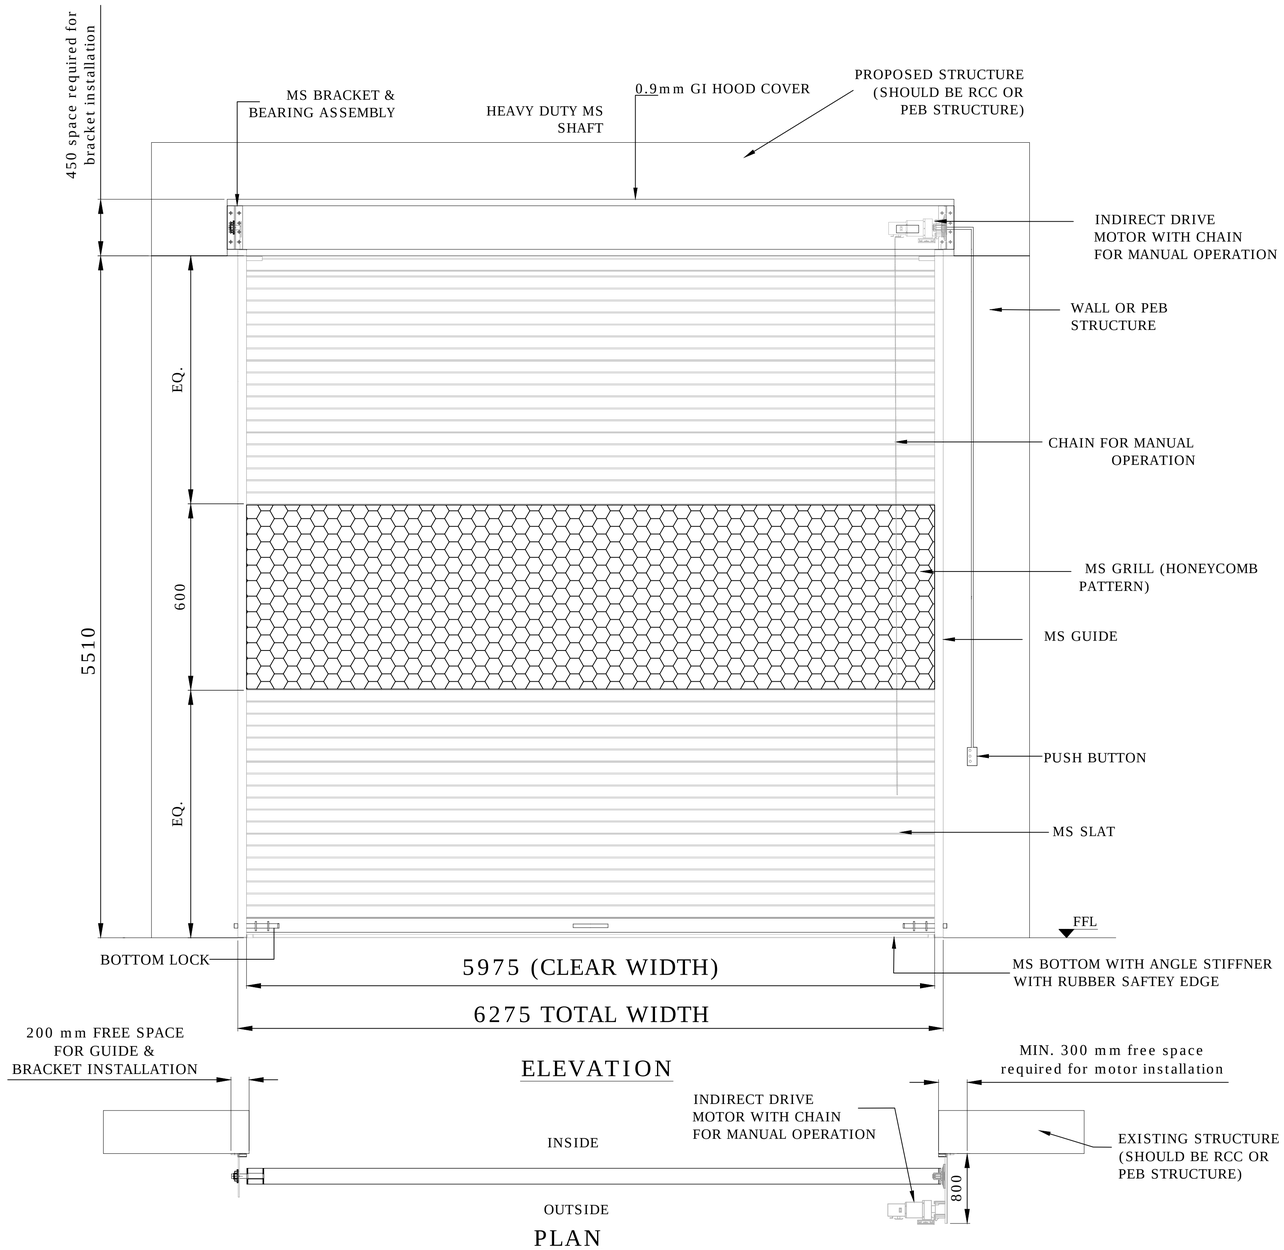



ELEVATION

PLAN

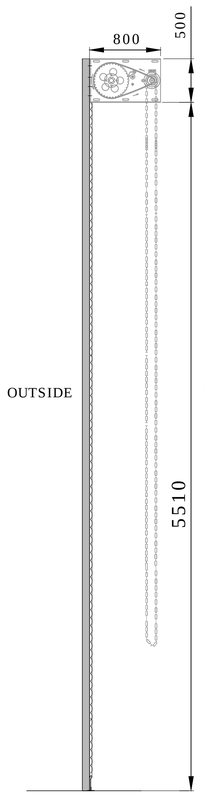



SIDE VIEW

1mm Thk.Curve Type MS Shutter lath AT TOP & BOTTOM

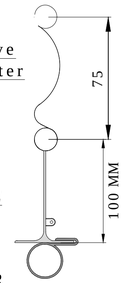

M.S. BOTTOM RAIL PROFILE 2.5MM THK WITH ANGLE STIFFNER & EPDM RUBBER

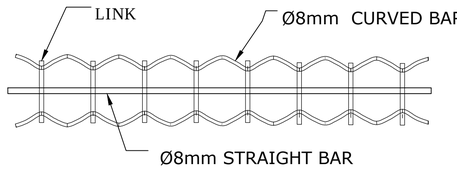

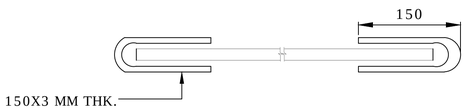

DIMENSION :

CLEAR WIDTH	CLEAR HEIGHT	QUANTITY
5975	5510	1

MATERIAL :

THICKNESS :

NOTE-
1.ONE COAT OF RED OXIDE WILL BE GIVEN SHUTTER (ONLY MS PART).
2. HOOD COVER WILL BE IN GI.
3.SINGLE PHASE SUPPLY SHOULD BE GIVEN TO THE SHUTTER.
4. REQUIRED STRUCTURE FOR SHUTTER SHALL BE IN CLIENT'S SCOPE.
5. ALL CIVIL WORK WILL BE IN CLIENT'S SCOPE.
6. TOLERANCE FOR GRILL SIZE SHALL BE PLUS/MINUS 15mm

NIHVA TECHNOLOGIES PVT. LTD.
NIHVA TECHNOLOGIES PVT. LTD. PUNE
Email:- info@nihva.com
Website:- www.nihva.com

TITLE:

MOTORIZED GRILLED ROLLING SHUTTER

CLIENT'S APPROVAL :

CLIENT - VAICHAL CONSTRUCTION

PROJECT - TAGMA CENTRE

SITE LOCATION - CHAKAN

DWG. NO. :NIHVA/17-18/0124

SCALE: NTS	WT:	SHEET:1 OF 1

DRAWN BY: OMKAR	DATE: 11-07-2017
CHECK : SHEKHAR	DATE: 11-07-2017
APPROVED : SHEKHAR	DATE: 11-07-2017

If any queries contact : projects@nihva.com

NOTE: ALL DIMENSIONS ARE IN mm

CLEAR WIDTH	CLEAR HEIGHT	QUANTITY
5975	5510	1

THIS DRAWING & DESIGN IS THE PROPERTY OF NIHVA TECHNOLOGIES. NOT TO BE SOLD OR COPY TO ANY OTHER CONCERN.