NIHVA TECHNOLOGIES

Weight Estimation Sheet

CLIENT	AVM							DATE	30-01-2024
PROJECT	Motorised Sliding Gate							LOCATION-	Pune
FINISH SIZE	12 M X 10 M								
	Sizes (In mm)								
Description	Material Grade	Sp.Gravity	Dia	Width	Height	Thickness	Length	QUANTITY	WEIGHT (KG)
A.Square Tube-outer	MS	7.85		72	72	2.5	129696	1	707.6
B.Square Tube-inner	MS	7.85		72	72	2.5	66000	1	360.1
MS cladding Sheet 1 MM	MS	7.85		2500	1200	1		42	989.1
MS BAR (Track) (in metre)	MS	7.85	25				31	1	77.5
Square Tube (TOP TRACK)	MS	7.85		60	60	5	31	1	356.5
							Weight For Single Quantity		2490.8
							Weight For Single Quantity(Including Safety factor)	1.2	2988.9
							Weight For Required Quantity(Including safety Factor)	2	5977.8

Cladding Sheet considered at one side only (Front)


Safety Factor Considered 1.2

Cladding sheet weight can be reduce upto by using wooden sheet / shera wood / plywood / HPL sheet

leaf sizes : Master leaf (07 metre)+ Slave Leaf(05 metre)= 12 metre

Weight for Leaf= 2056.8 kg | Motor Consideration=3tonn (Including safety Factor)

Reference Image :

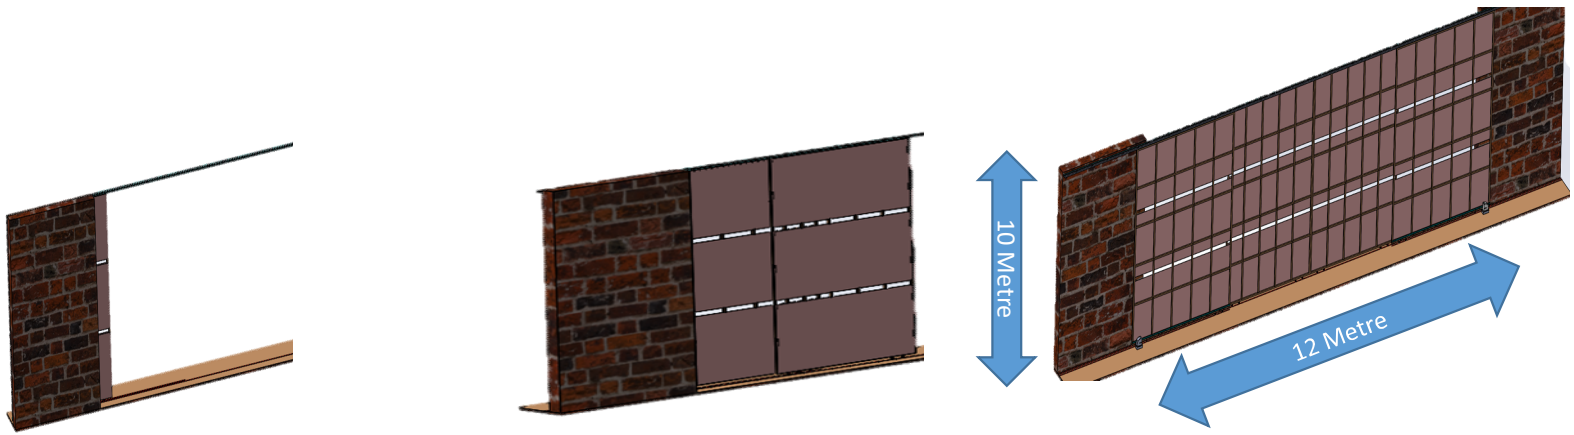

Open condition	Operating Condition	close condition

Prepared By
Sumit