

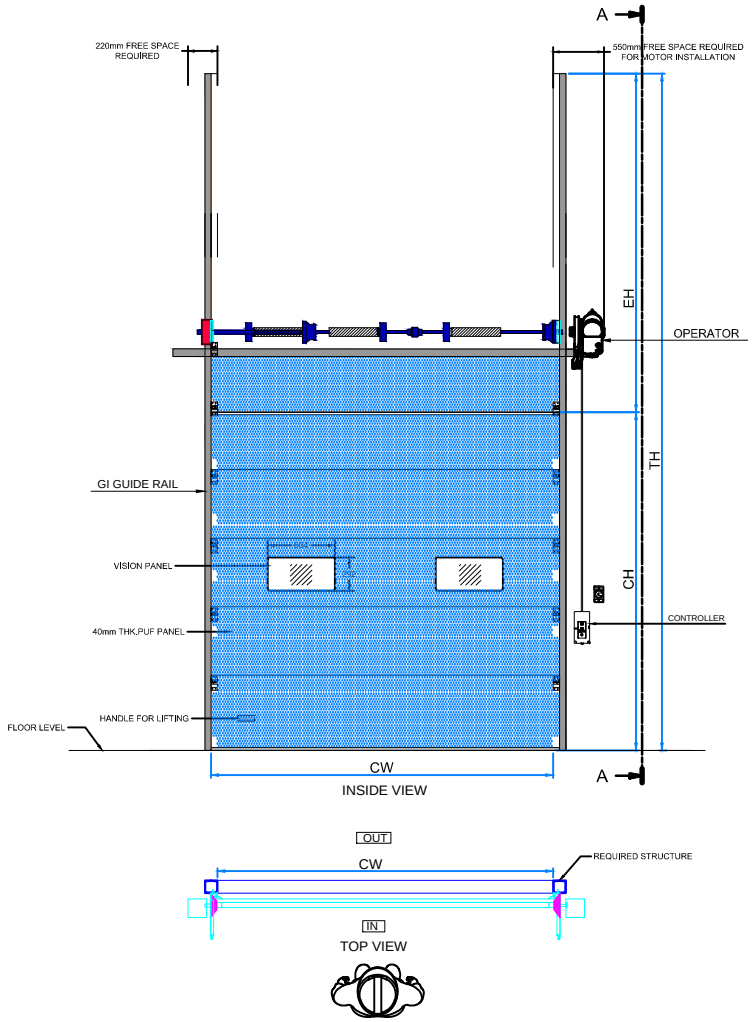


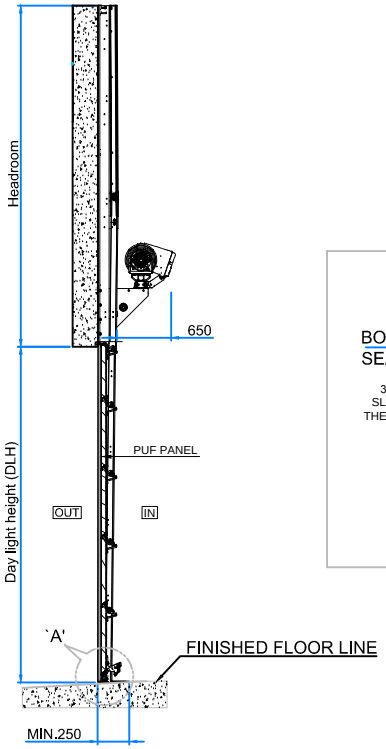

SECTION A-A

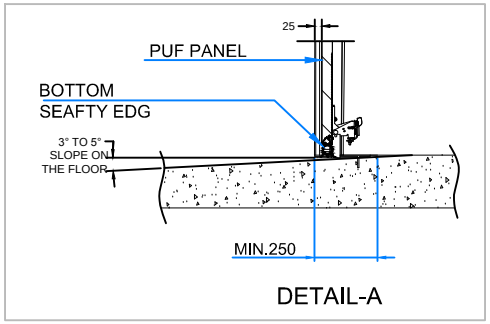

DETAIL-A

NOTE
1. ALL REQUIRED STRUCTURE WORK WILL BE IN CLIENTS SCOPE.

SR NO	CLEAR WIDTH	CLEAR HEIGHT	QTY	TH
01	4500 mm	4500 mm	03	9365

TOLERANCE: ±10mm

This drawing & design is the property of NIHVA TECHNOLOGIES. Not to be sold or copied to any other concern.

TITLE				
SECTIONAL DOOR (VL)				NIHVA TECHNOLOGIES PVT. LTD. PUNE Tel : 020 66304033 Website:- www.nihva.com Email:- info@nihva.com
	NAME	SIGN	DATE	
DRAWN	P.V.A		22.03.19	CLIENT - UNITED ARCHITECT
CHECK	V.M.T		22.03.19	PROJECT - ESR
APPROVAL				LOCATION - BHIWANDI
If any queries contact : design@nihva.com				DWG. NO. : NIHVA/18-19/0303 REV: 00
ALL DIMENSION ARE IN mm				SCALE: NTS WT: SHEET: 01 OF 01