



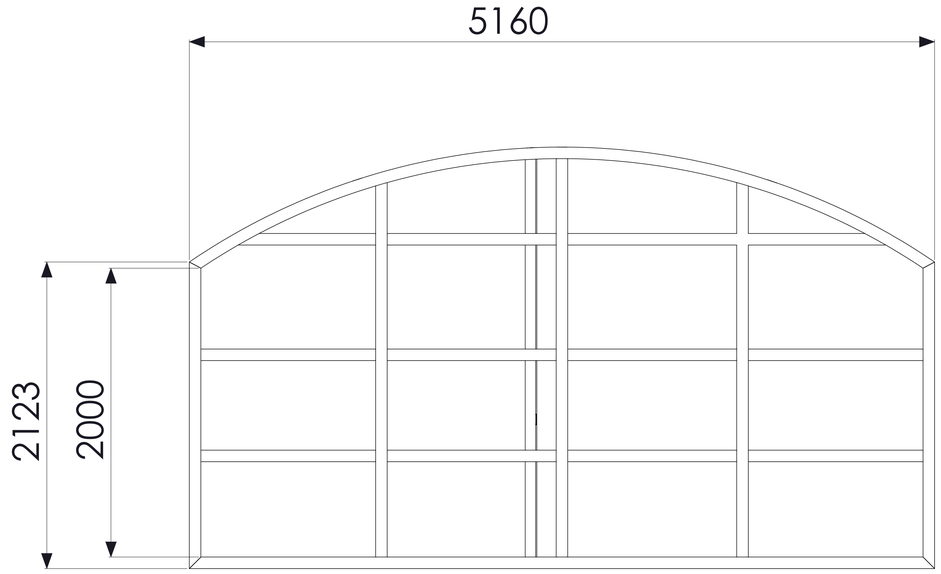


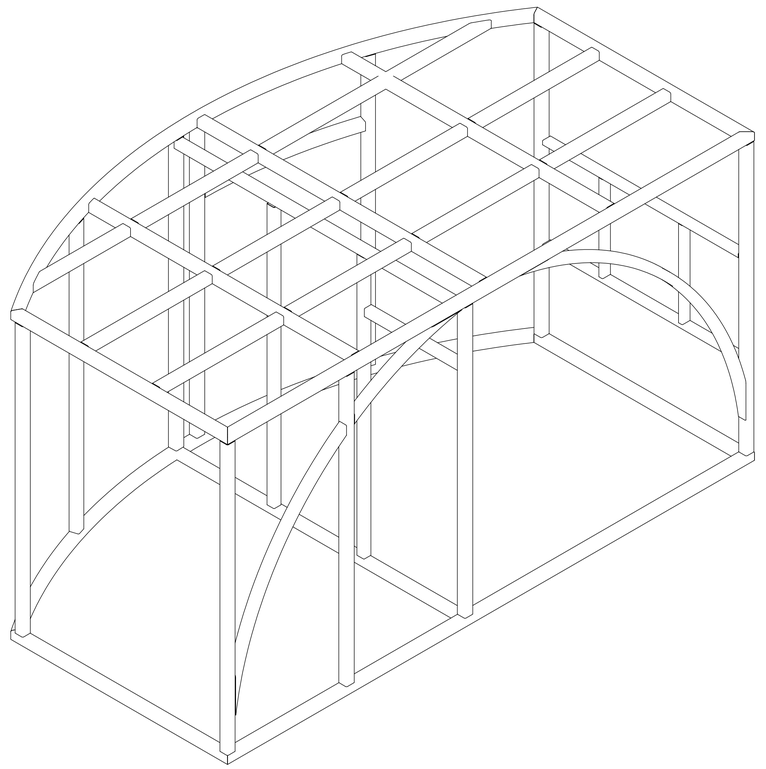

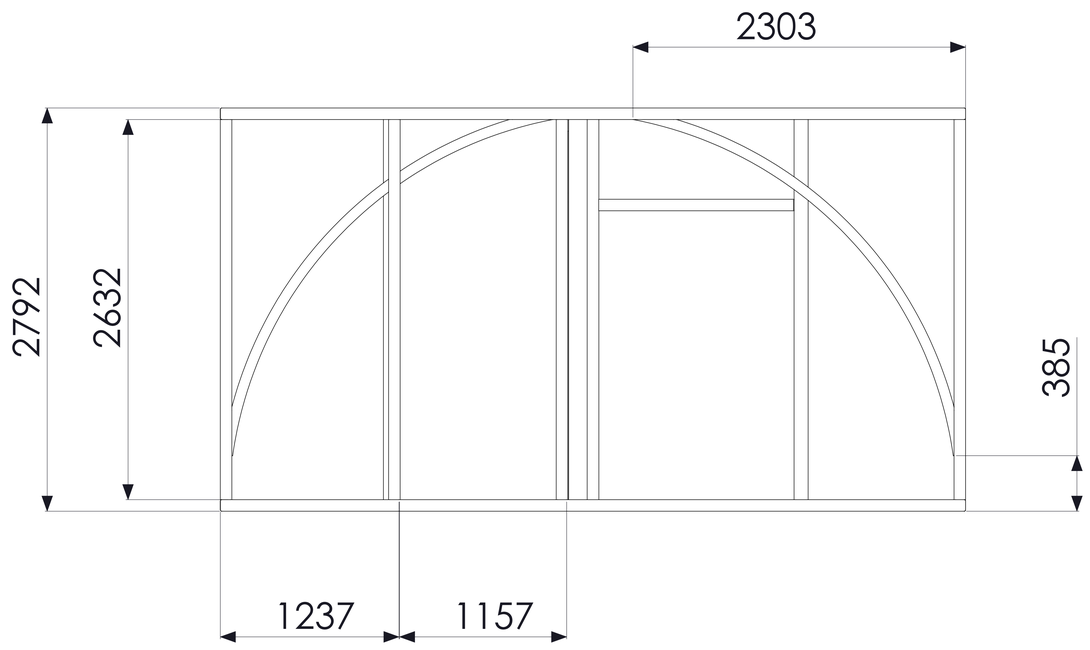

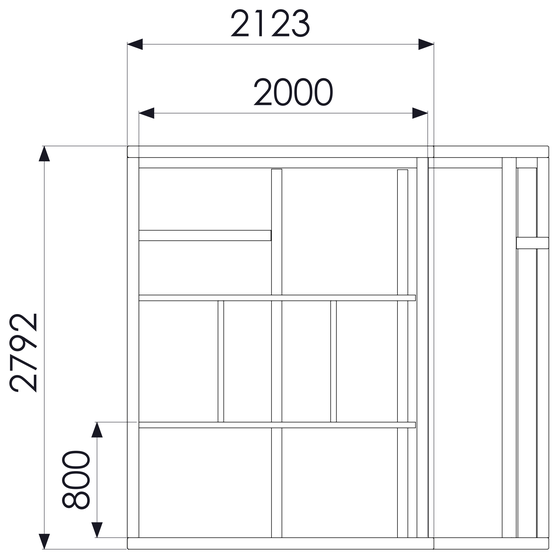


TITLE -	MS ROOM		
QTY -	1		
PROJECT -	MV DOME		
DWG NO -	MVD-3		REV- 1
DATE -	15-7-2023		SHEET: 1/10

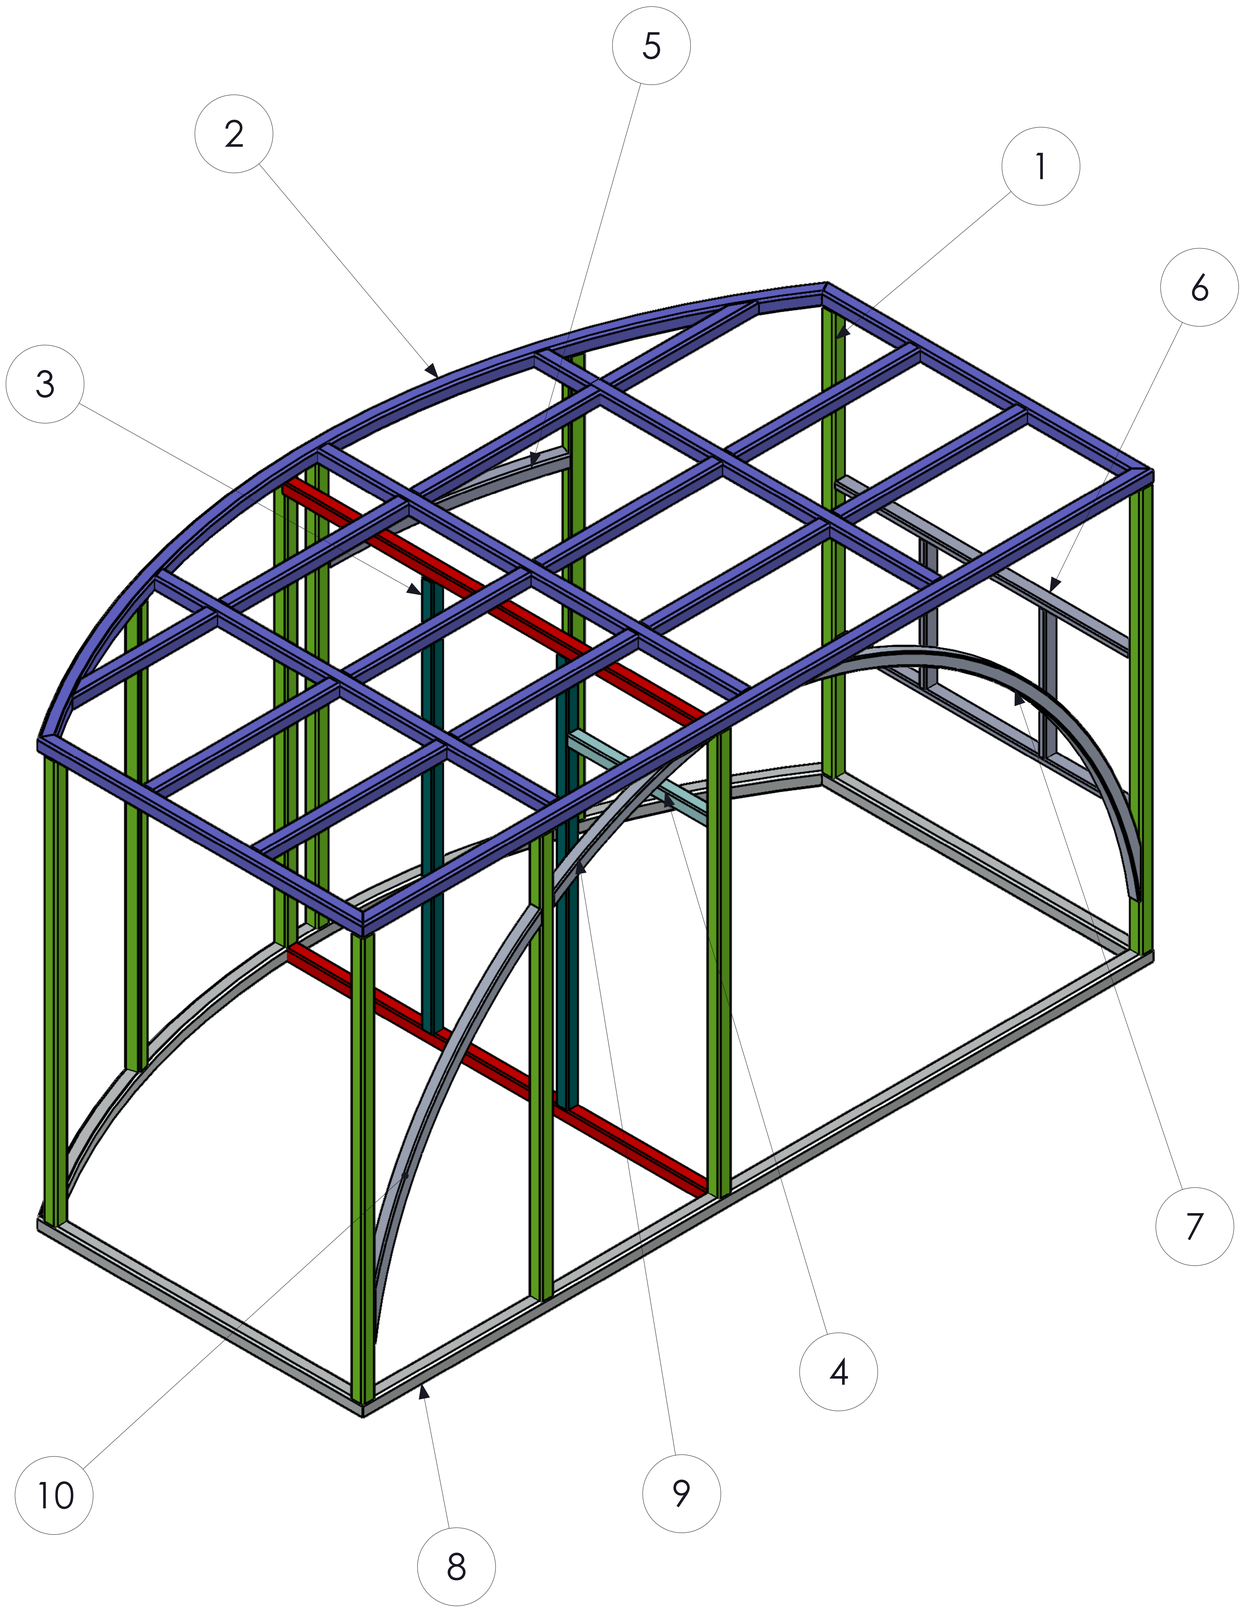

SR NO	NAME	DESCRIPTION	LENGTH	QTY
1	SQARE TUBE 1	80X80X4 MM THK	2632 MM	10
2	SQARE TUBE FRAME	80X80X4 MM THK	APD MVD-3-2	1
3	SQAURE TUBE-2	72X72X3 MM THK	2552 MM	2
4	SQUARE TUBE-3	80X80X4 MM THK	915 MM	1
5	SQUARE TUBE CURVED 1	72X72X3 MM THK	APD MVD -3 -5	1
6	WINDOW FRAME	80X40X3 MM THK	APD MVD-3-6	1
7	SQUARE TUBE CURVED 2	72X72X3 MM THK	APD MVD-3-7	1
8	SQARE TUBE FRAME BTM	80X80X4 MM THK	APD MVD-3-8	1
9	SQUARE TUBE CURVED 3	72X72X3 MM THK	APD MVD -3-9	1
10	SQUARE TUBE CURVED 4	72X72X3 MM THK	APD MVD-3-10	1

DRAWING NO: MVD-3


SHEET: 2/10

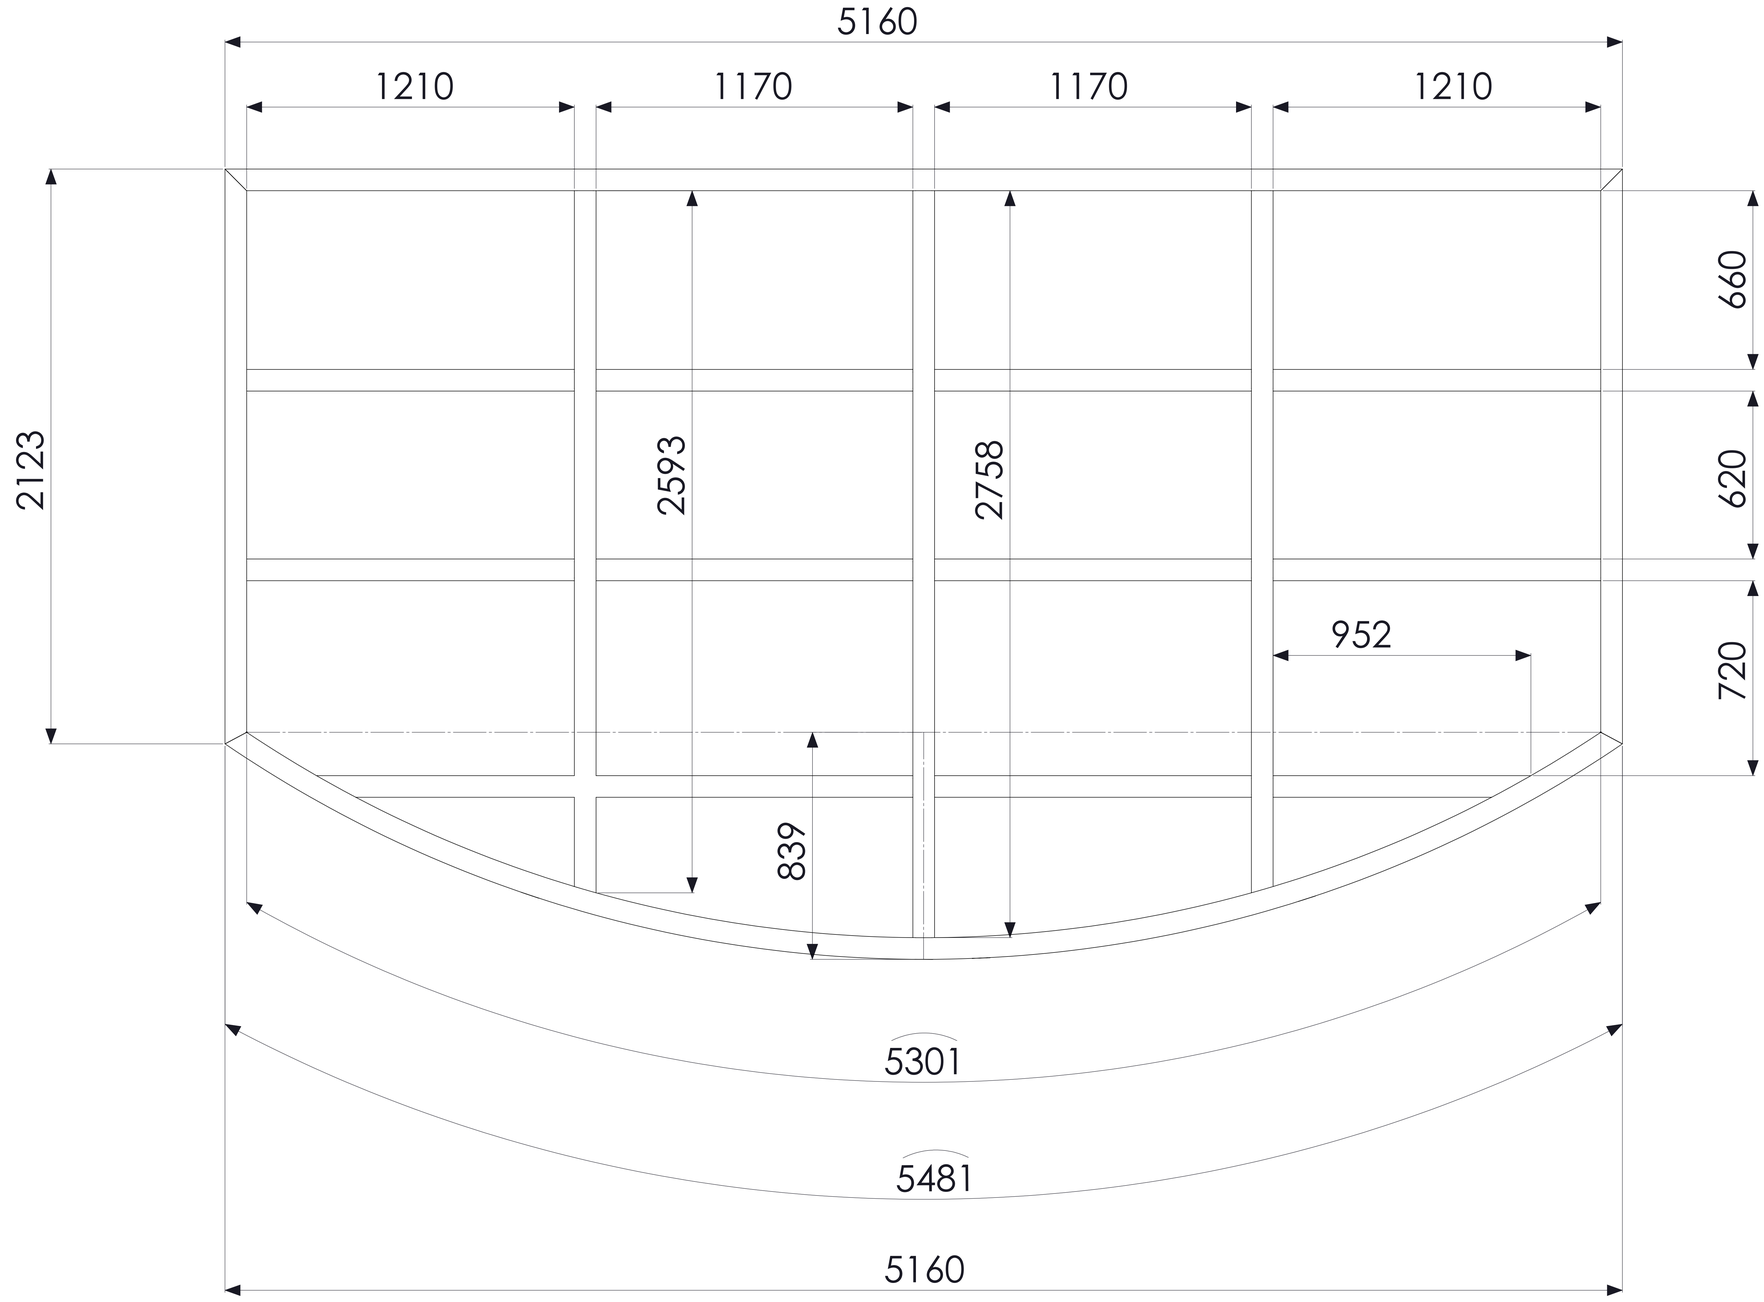

SQAURE TUBE FRAME

DRAWING NO: MVD-3-2	SHEET: 3/10


SR NO	NAME	DESCRIPTION	LENGTH	QTY
1	TUBE 1	SQ TUBE 80X80X4 MM	5160 MM	1
2	TUBE 2	SQ TUBE 80X80X4 MM	2123 MM	2
3	CURVE TUBE	SQ TUBE 80X80X4 MM	5481 MM	1
4	INTERMEDIATE TUBE 1	SQ TUBE 80X80X4 MM	2758 MM	1
5	INTERMEDIATE TUBE 2	SQ TUBE 80X80X4 MM	2593 MM	2
6	INTERMEDIATE TUBE 3	SQ TUBE 80X80X4 MM	1210 MM	4
7	INTERMEDIATE TUBE 4	SQ TUBE 80X80X4 MM	1170 MM	12
8	INTERMEDIATE TUBE 5	SQ TUBE 80X80X4 MM	952 MM	2

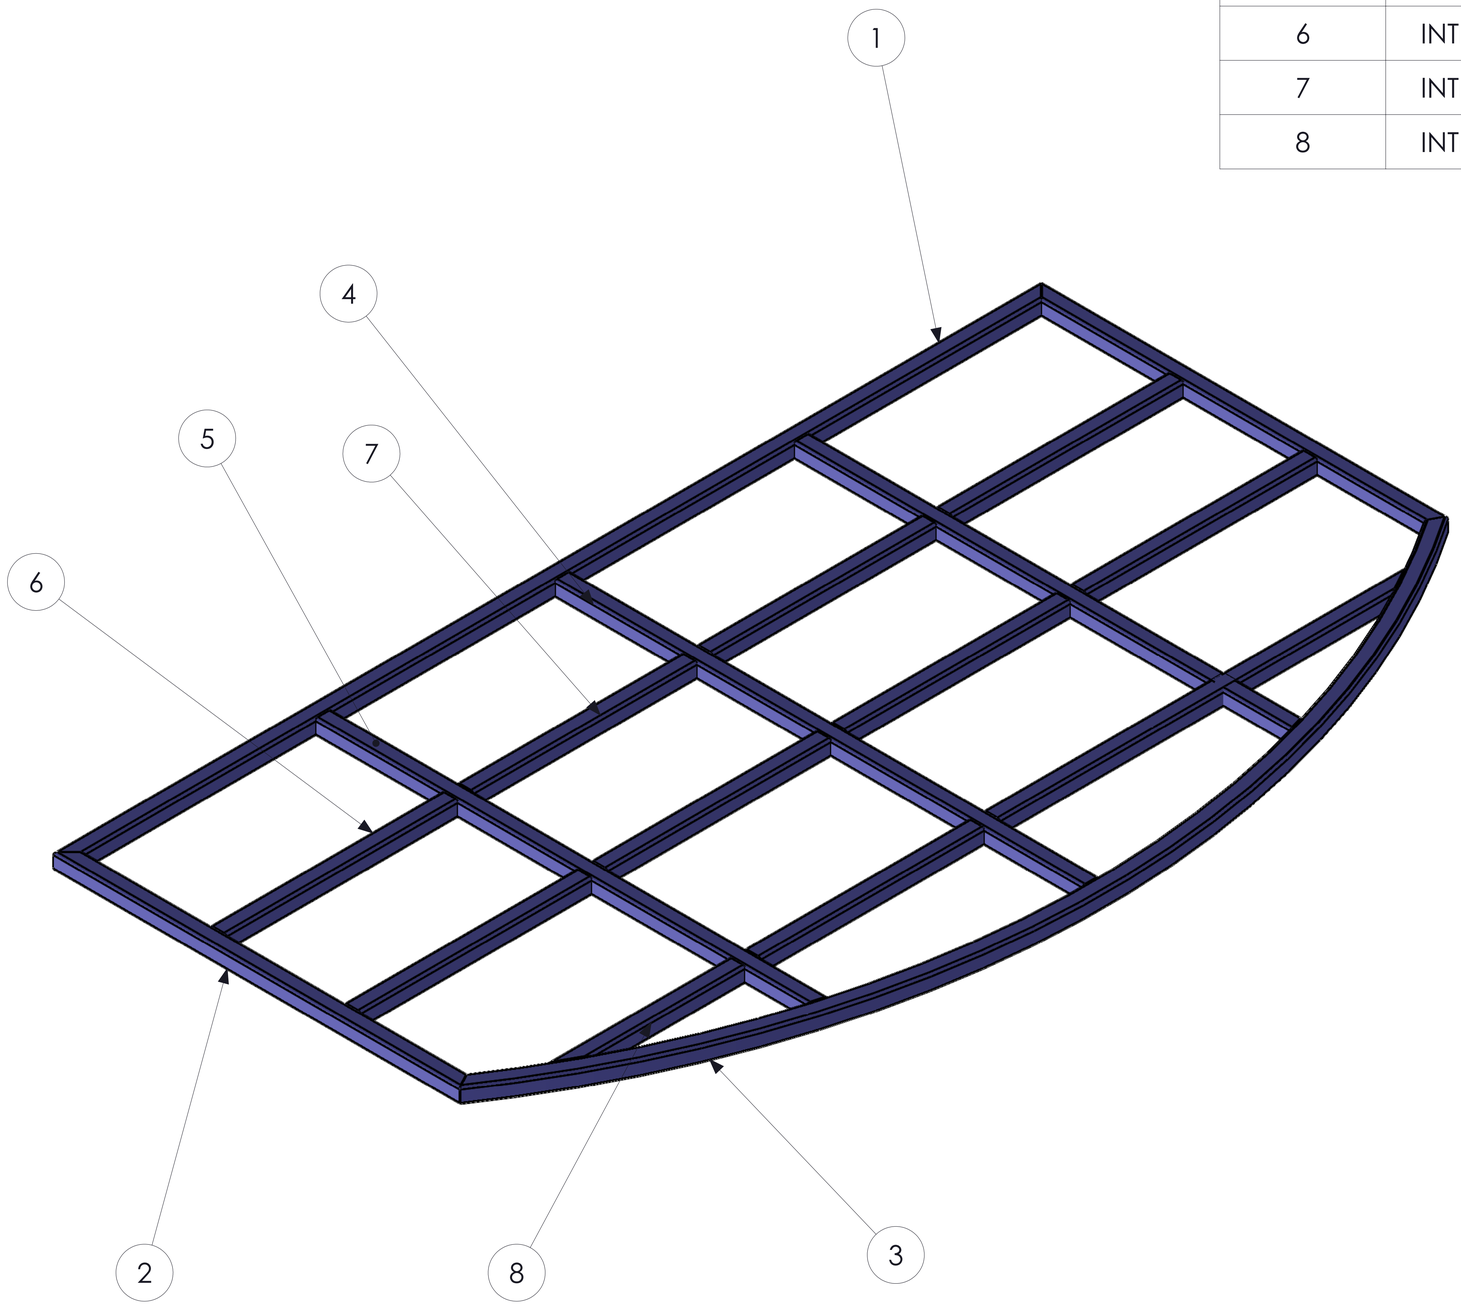


DRAWING NO: MVD-3-2-1

SHEET: 4/10

sr no	name	Description	Length	qty
1	TUBE CURVED 1	SQ TUBE 80X80X4 MM	1392 mm	1

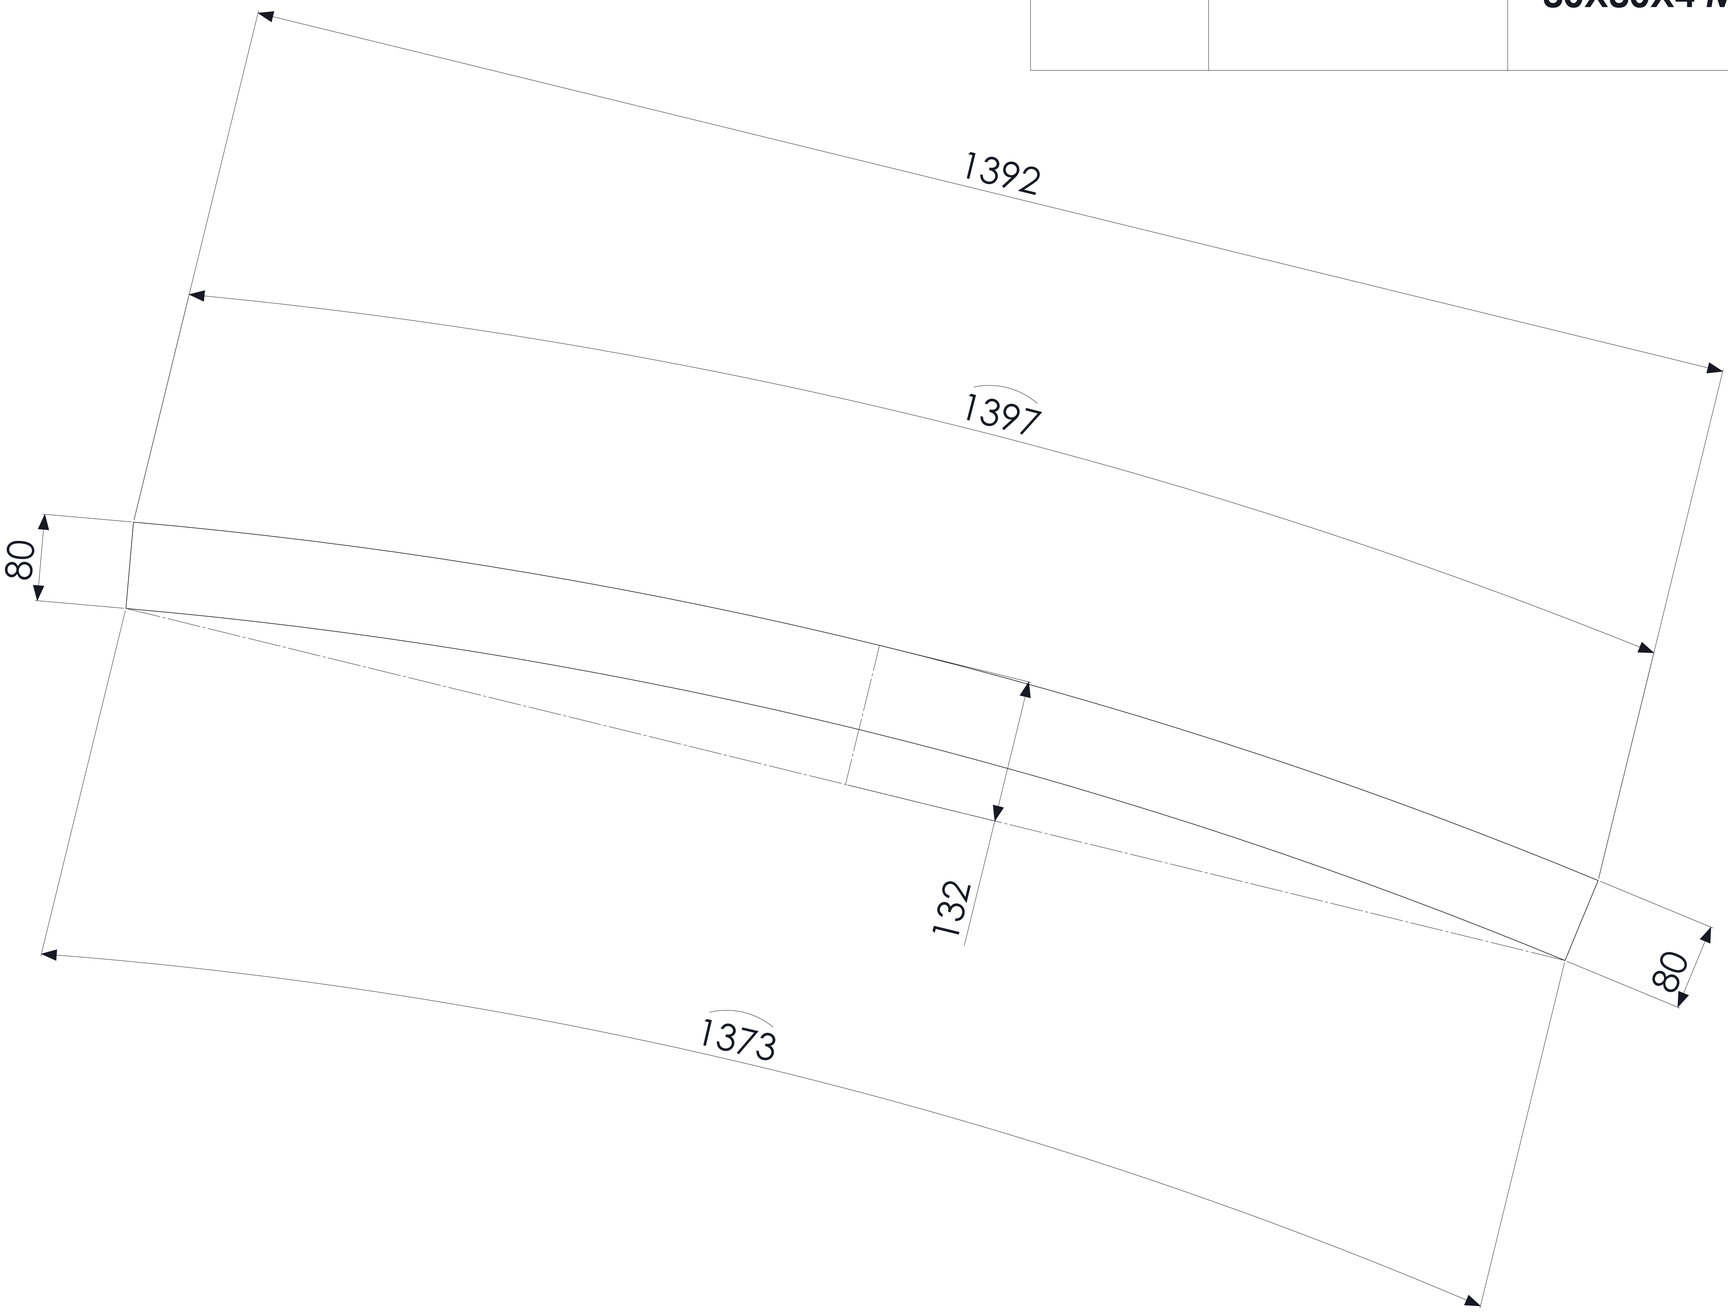


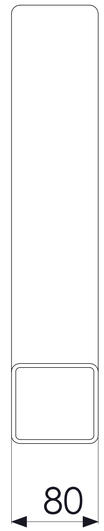

TUBE CURVED 1

DRAWING NO: MVD-3-5	SHEET: 5/10

SR NO	PART NAME	DESCRIPTION	LENGTH	QTY
1	SQUARE TUBE HORIZHONTAL	80X40X3 MM THK	1915 MM	2
1	SQUARE TUBE VERTICAL	80X40X3 MM THK	840 MM	2

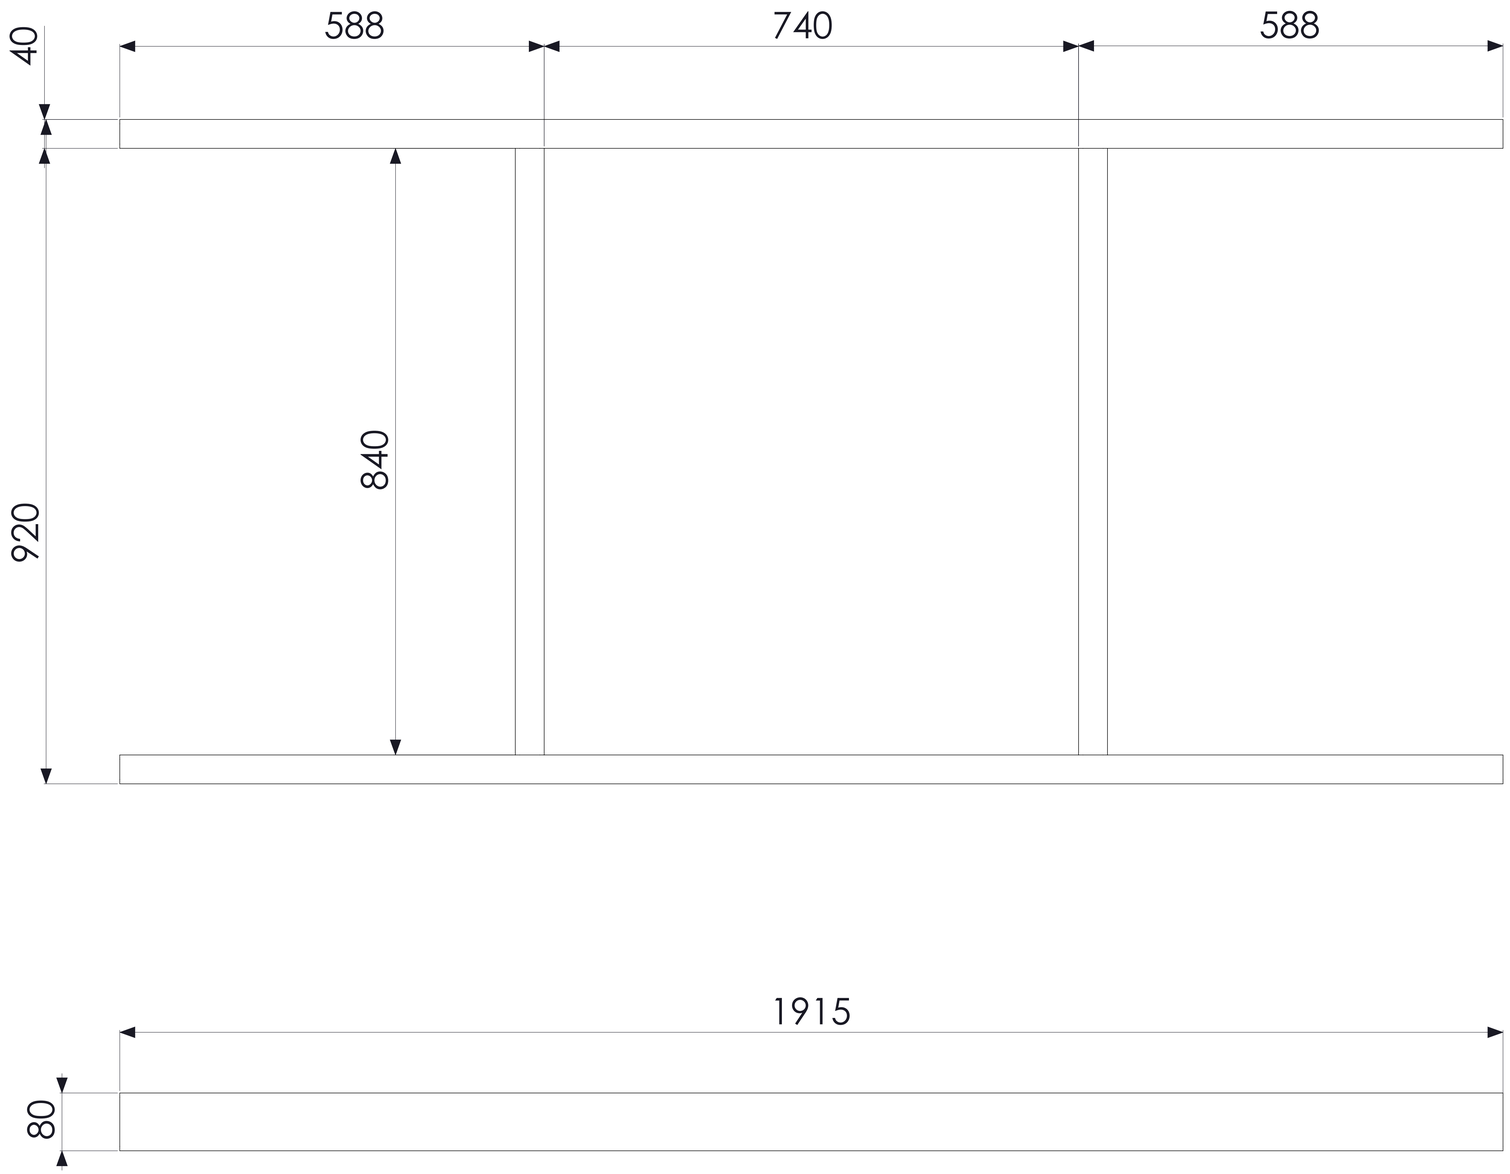


WINDOW FRAME

DRAWING NO: MVD-3-6

SHEET: 6/10

SR NO	PART NAME	DESCRIPTION	LENGTH	QTY
1	CURVE SECTION	72X72X3 MM THK	3521 MM	1

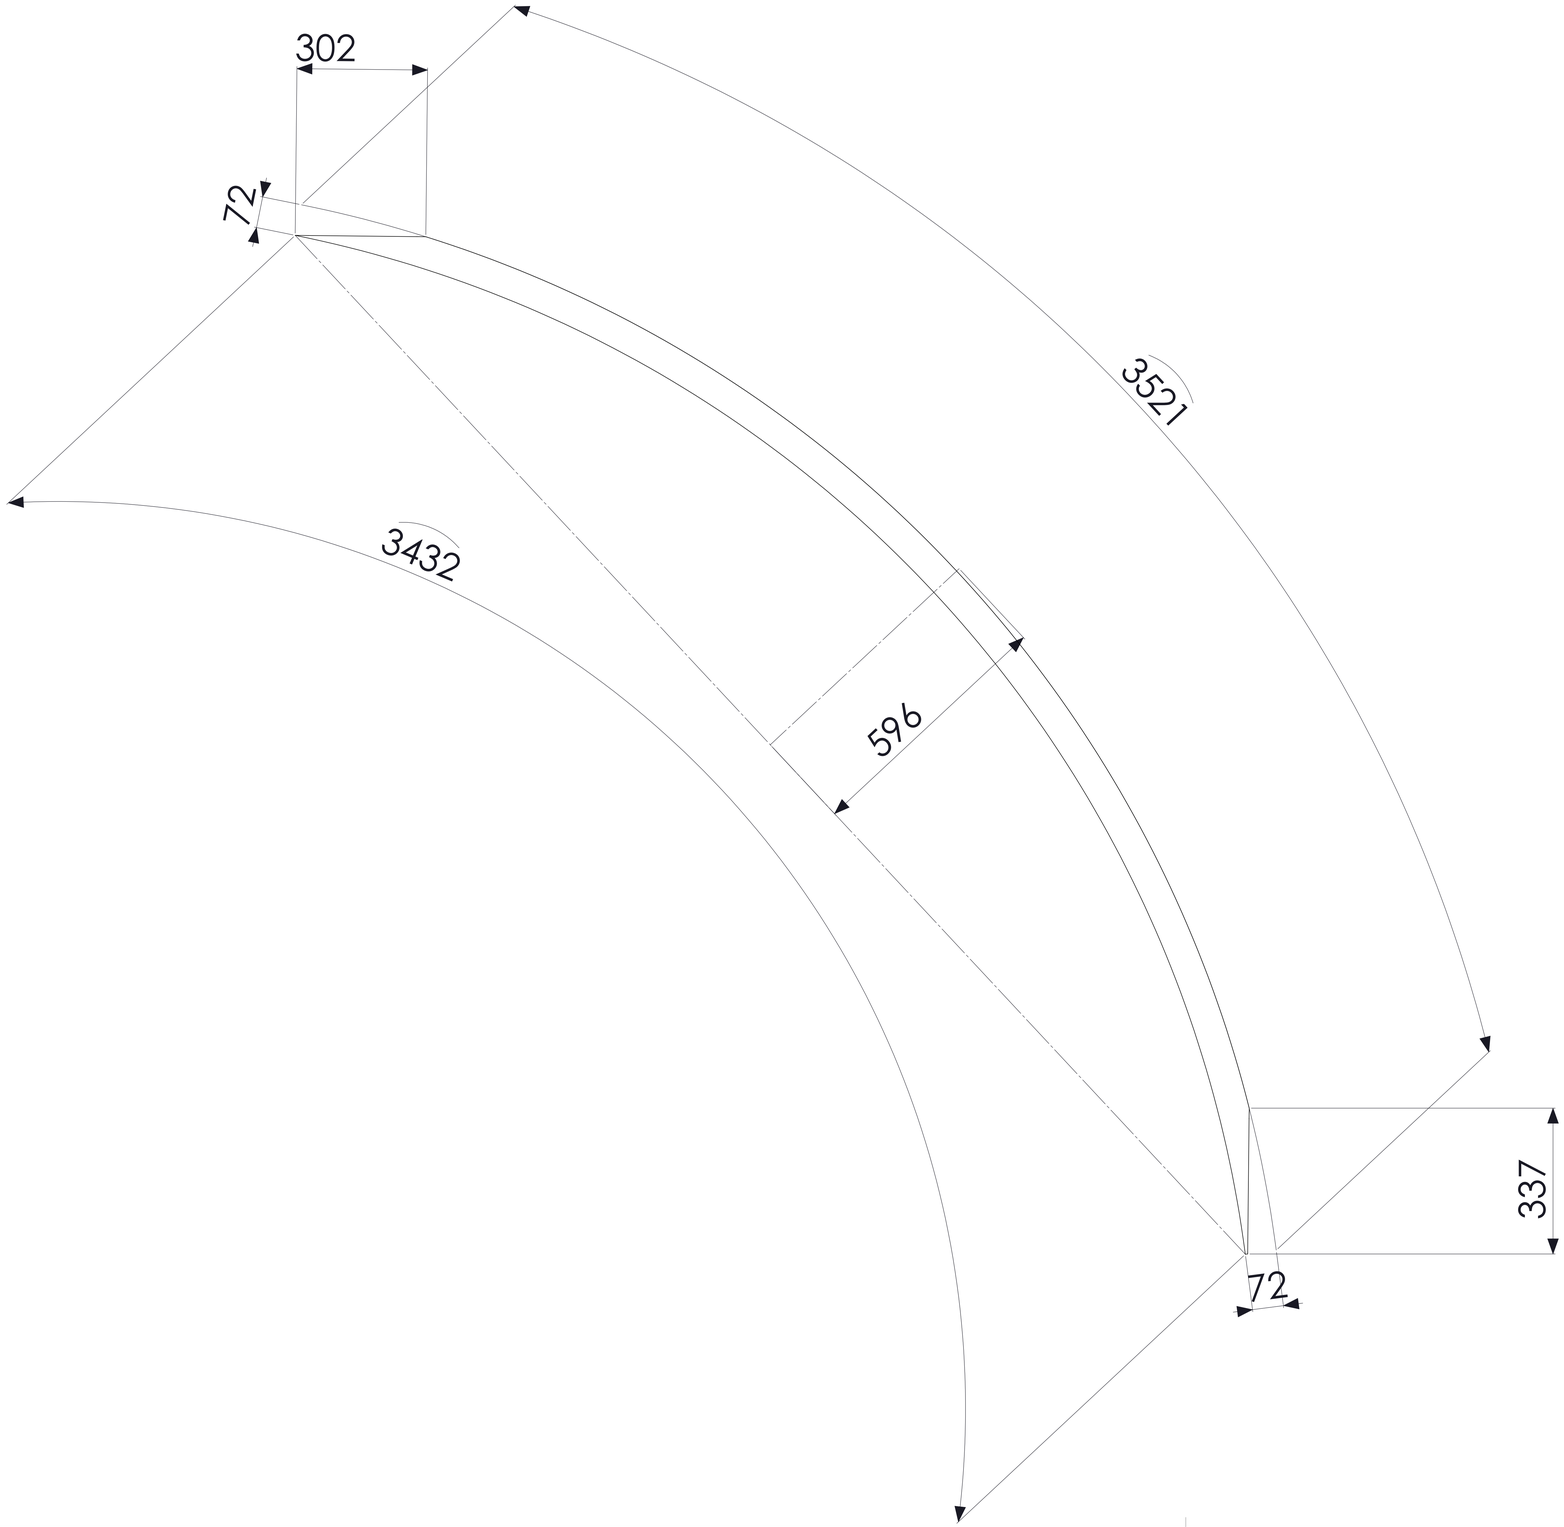


CURVE SECTION

DRAWING NO: MVD-3-7

SHEET: 7/10

sr no	name	description	length	qty
1	TUBE 1	SQ TUBE 80X80X4 MM	5160 MM	1
2	TUBE 2	SQ TUBE 80X80X4 MM	2123 MM	2
3	CURVE TUBE	SQ TUBE 80X80X4 MM	5481 MM	1

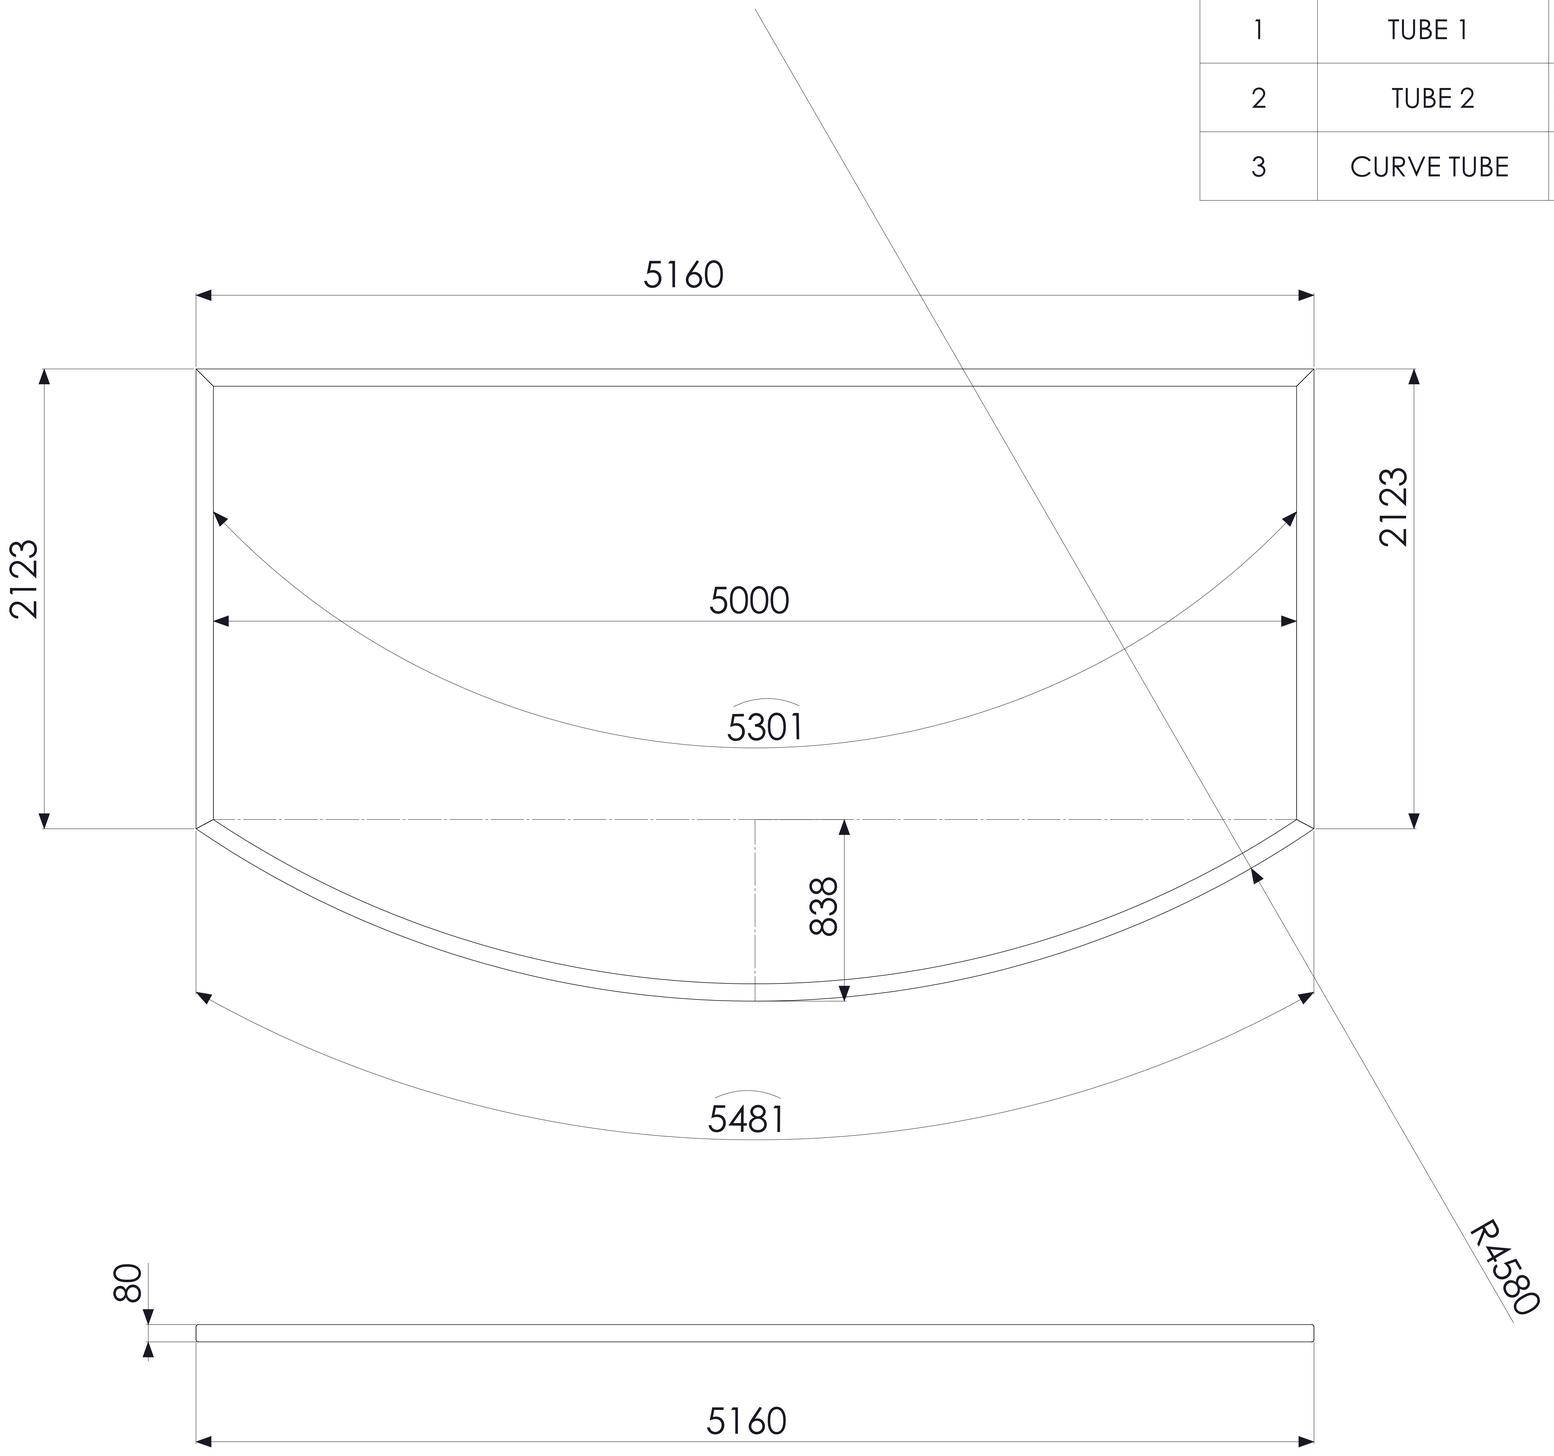


BTM FRAME

DRAWING NO: MVD-3-8

SHEET: 8/10


SR NO	PART NAME	DESCRIPTION	LENGTH	QTY
1	CURVE SECTION 3	72X72X3 MM THK	2288 MM	1

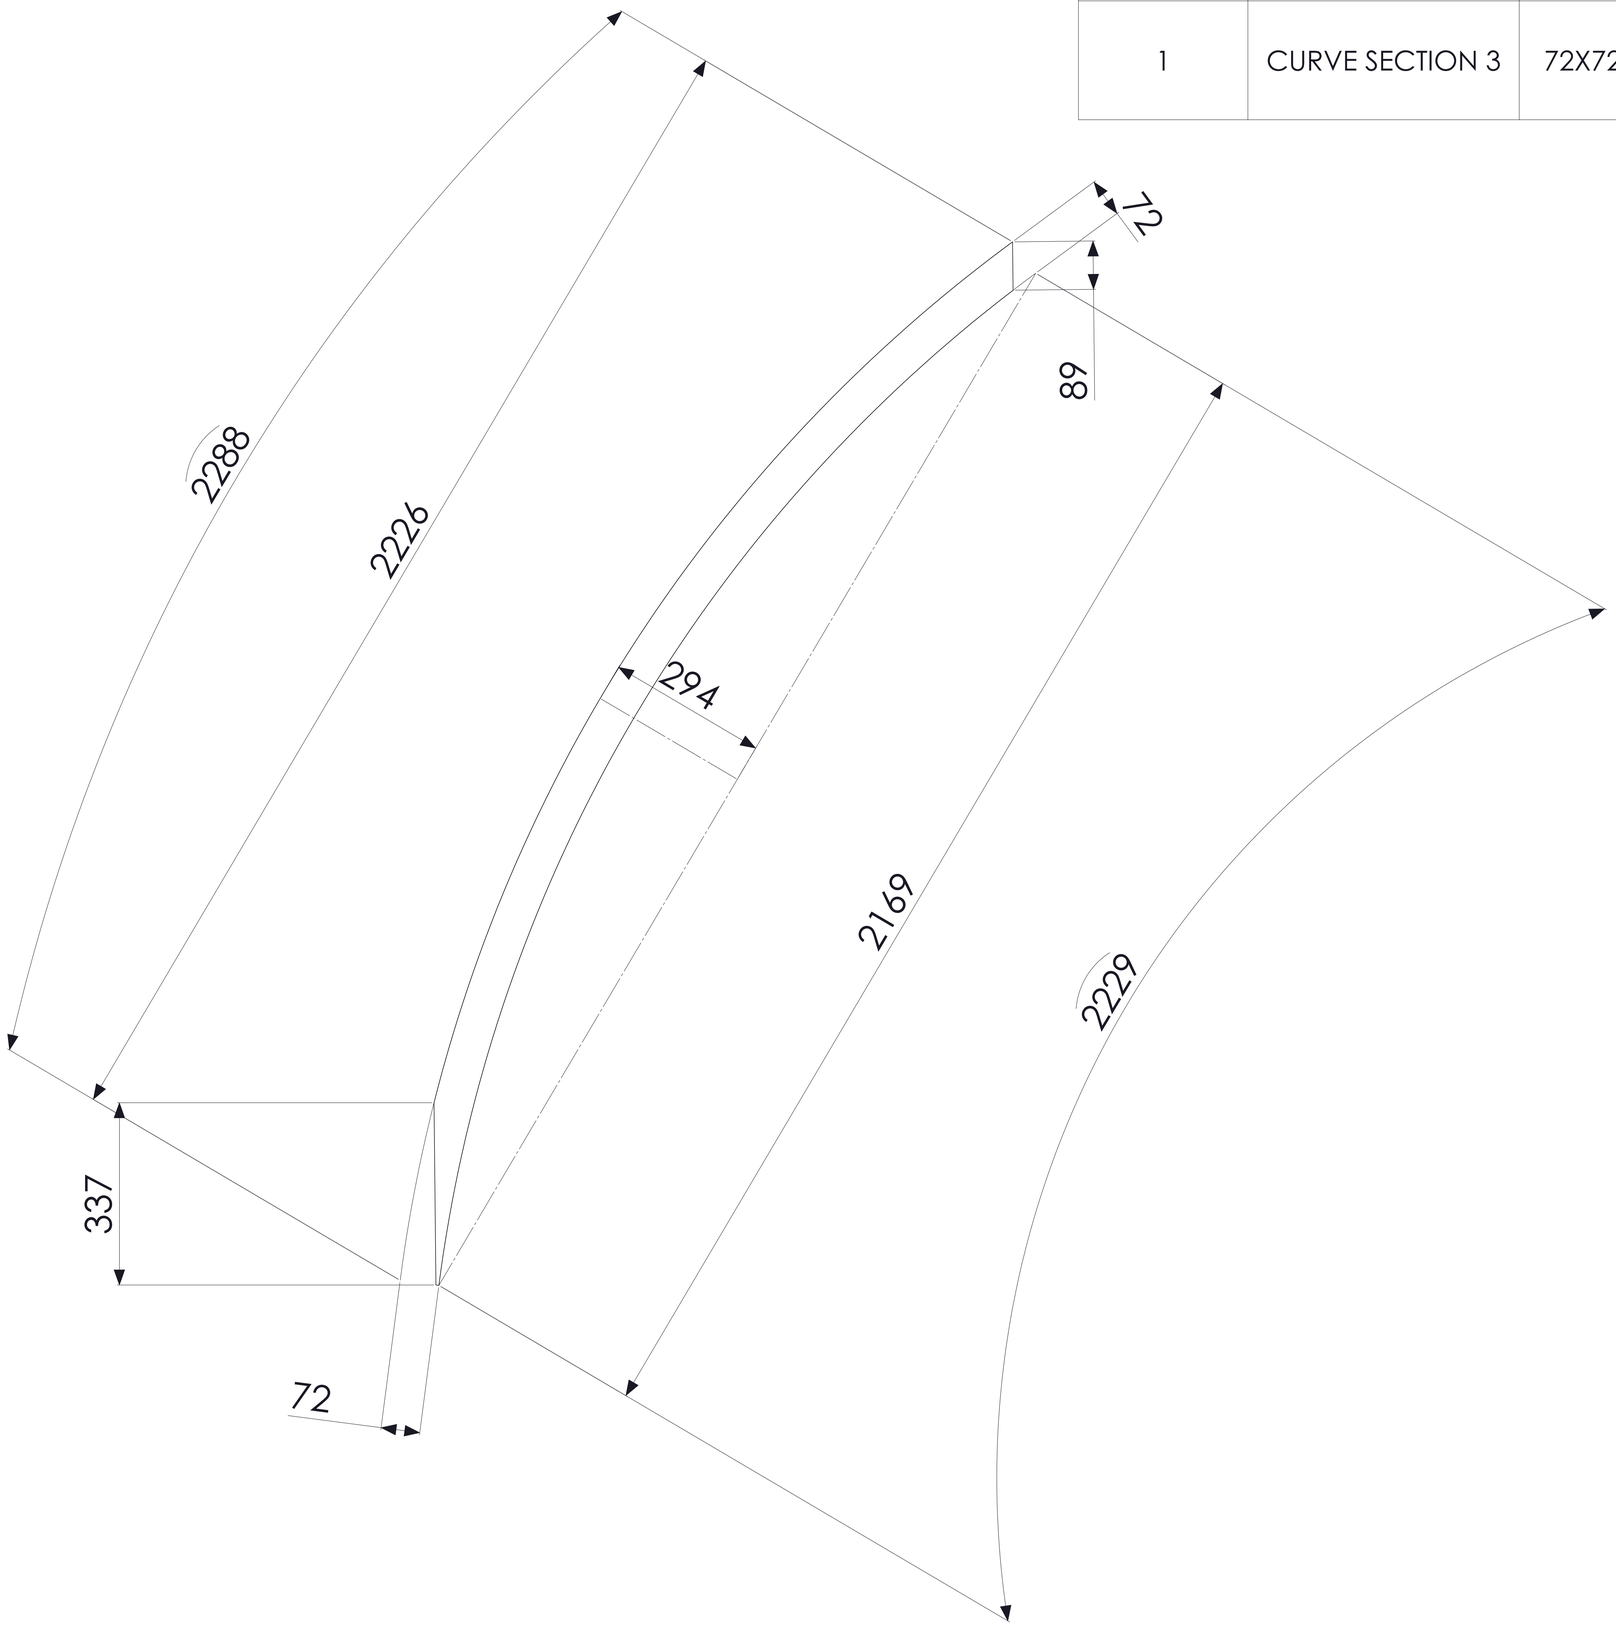

DRAWING NO: MVD-3-9

SHEET: 9/10

SR NO	PART NAME	DESCRIPTION	LENGTH	QTY
1	CURVE SECTION 4	72X72X3 MM THK	1190 MM	1

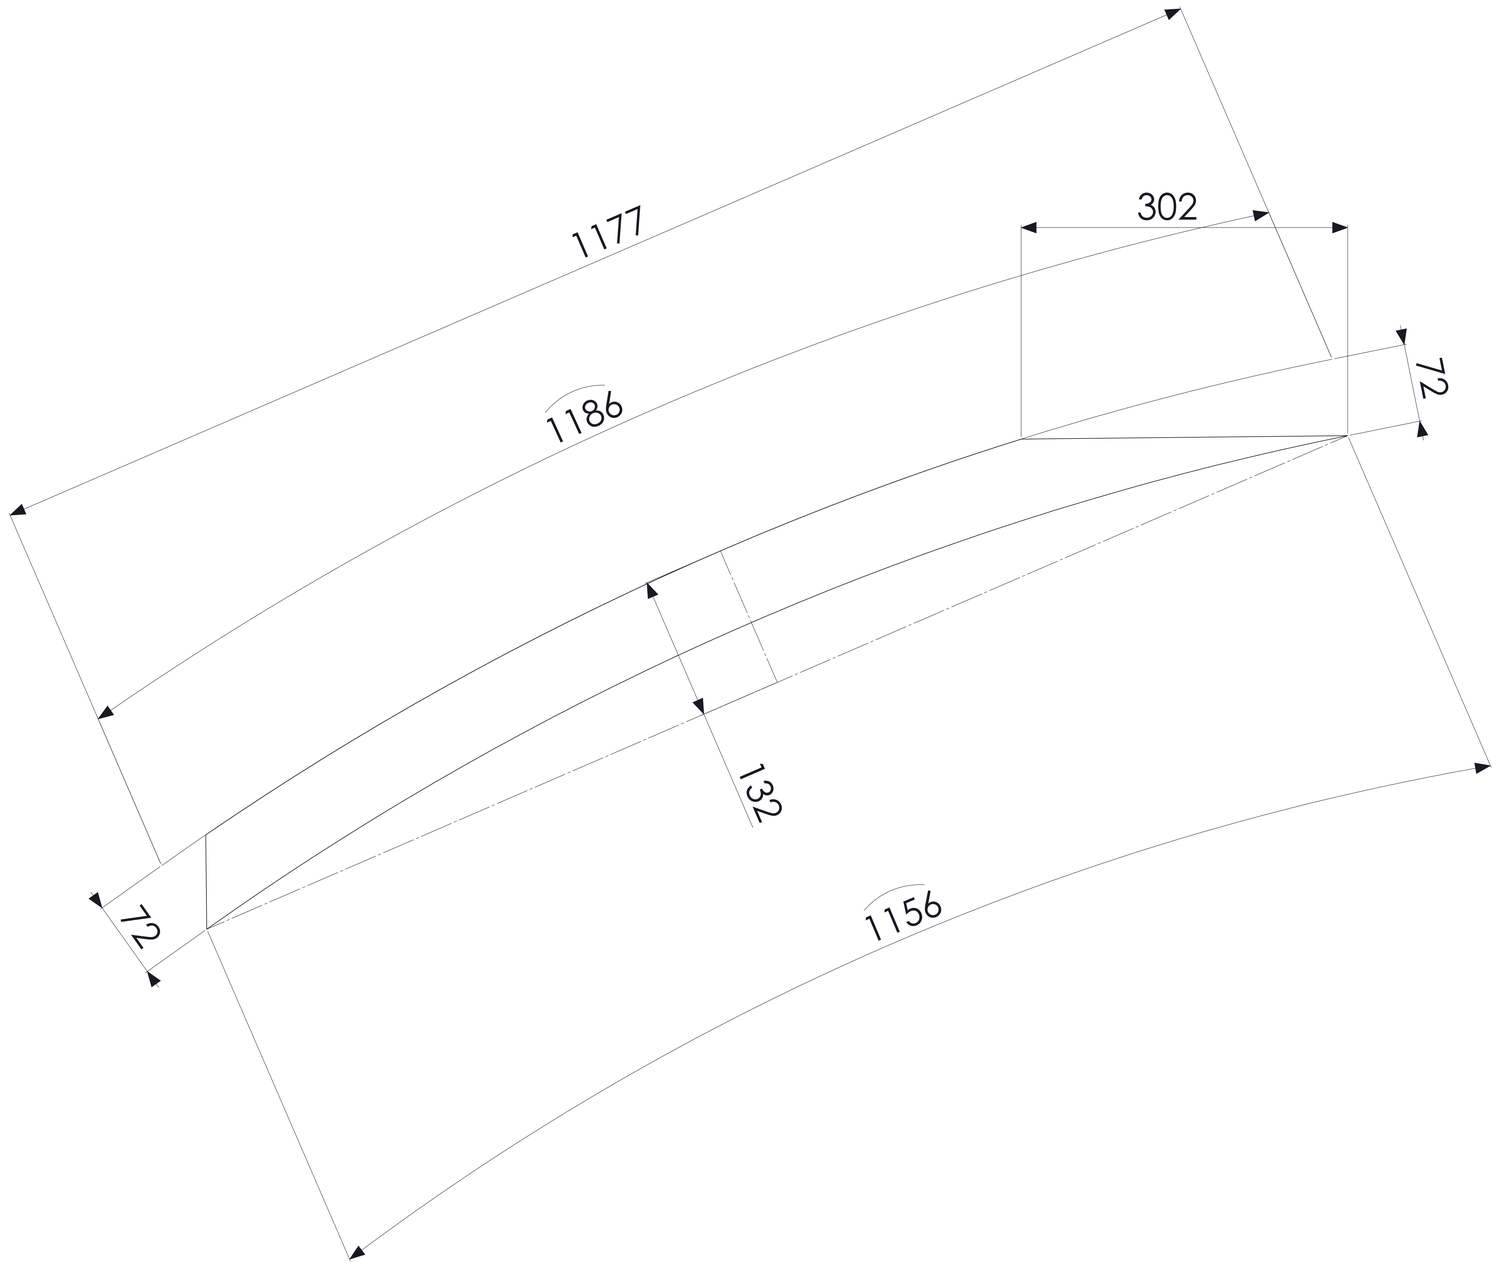

DRAWING NO: MVD-3 -10	SHEET: 10/10