
DO NOT SCALE

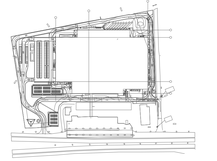

GENERAL NOTES:

ALL DIMENSIONS ARE IN MILLIMETERS & LEVELS ARE IN METERS.

DO NOT SCALE DRAWINGS: ALL DIMENSIONS SHALL HAVE PREFERENCE OVER SCALE AND BE FIELD VERIFIED AND COORDINATED WITH WORK OF ALL TRADES. IF NO DIMENSIONS ARE GIVEN OR DISCREPANCIES FOUND, THE CONTRACTOR SHALL NOTIFY THE ARCHITECT FOR CLARIFICATION BEFORE BIDDING OR COMMENCING THE WORK.

ALL WORKS TO BE CARRIED OUT IN STRICT ACCORDANCE WITH LOCAL AUTHORITY REQUIREMENTS, NATIONAL BUILDING REGULATIONS & RELEVANT STANDARDS.

ARCHITECTURAL DRAWINGS SHOULD BE READ IN CONJUNCTION WITH PROJECT SPECIFICATIONS, STRUCTURAL, MECHANICAL, ELECTRICAL, PLUMBING, FIRE & LANDSCAPE DRAWINGS AND ARCHITECTURE TECHNICAL SPECIFICATION DOCUMENT (PJNAB-ATK-ARC-SPC-NA-0001)

FOR ALL DETAILS OF CIVIL & STRUCTURAL WORKS, REFER STRUCTURAL DRAWINGS.

FOR ALL MECHANICAL EQUIPMENT, FIXTURES, SERVICES & RELATED WORKS, REFER MECHANICAL DRAWINGS.

FOR ALL ELECTRICAL EQUIPMENT, FIXTURES, SERVICES & RELATED WORKS, REFER ELECTRICAL DRAWINGS.

FOR ALL PLUMBING EQUIPMENT, FIXTURES, SERVICES & RELATED WORKS, REFER PLUMBING DRAWINGS.

FOR ALL FIRE EQUIPMENT, FIXTURES, SERVICES & RELATED WORKS, REFER FIRE DRAWINGS.

FOR ALL LANDSCAPE ELEMENTS, TREES LOCATION, MATERIALS & RELATED WORKS, REFER LANDSCAPE DRAWINGS.

FOR NOTES, SYMBOLS & LEGENDS REFER PJNAB-ATK-ARC-DWG-NA-0006.

THE CONTRACTOR SHALL COMPARE THE ARCHITECTURAL, STRUCTURAL, MECHANICAL, ELECTRICAL, PLUMBING, FIRE & LANDSCAPE DRAWINGS. THE CONTRACTOR MUST REPORT ANY DISCREPANCIES BETWEEN EACH SET OF DRAWINGS TO THE ARCHITECT BEFORE COMMENCEMENT OF WORK.

THE BUILDING SHALL BE CONSTRUCTED IN FULL COMPLIANCE WITH ALL APPLICABLE CODES, ORDINANCES AND REGULATIONS AS WELL AS THE DRAWINGS AND SPECIFICATIONS. ANY CODE DEFICIENCIES IN THE DRAWINGS RECOGNIZED BY THE CONTRACTOR SHOULD BE BROUGHT TO THE ATTENTION OF THE ARCHITECT FOR CLARIFICATION.

THE CONTRACTOR SHALL BE RESPONSIBLE FOR THE ACCURATE PLACEMENT OF THE BUILDING ON THE SITE AND VERIFY ALL DIMENSIONS AND EXISTING CONDITIONS. DISCREPANCIES BETWEEN DRAWINGS AND ACTUAL SITE CONDITIONS SHALL BE BROUGHT TO THE ATTENTION OF THE ARCHITECT BEFORE BEGINNING THE PROJECT OR THE COMMENCEMENT OF WORK. THE OWNER SHALL NOT BE RESPONSIBLE FOR CHANGES TO THE WORK DUE TO THE FAILURE OF THE CONTRACTOR TO FAMILIARIZE HIMSELF WITH EXISTING CONDITIONS.

THE CONTRACTOR SHALL PROVIDE ALL PERMITS AND INSPECTION NECESSARY FOR THE PROPER EXECUTION OF THE WORK IN ACCORDANCE WITH APPLICABLE CODES AND GOVERNING REGULATIONS.

THE DRAWINGS HAVE BEEN PREPARED BASED ON THE APPROVED DESIGN FROM THE CLIENT. BASIS THE FOLLOWING STANDARDS & REGULATIONS:

- IKEA ENGINEERING & CONSTRUCTION MANUAL (IKEA Ind-TRANSMIT-000027)
- IKEA STANDARDS (IKEA Ind-TRANSMIT-000027)
- IKEA REFERENCES
- IKEA GROUP SAFETY & SECURITY MANUAL - RETAIL
- IKEA SHE MANUAL
- NATIONAL BUILDING CODE (NBC) 2016
- BANGALORE MAHANAGARA PALIKE BUILDING BYE-LAWS 2003
- REVISED MASTER PLAN 2015, BANGALORE, 2007 - VOLUME - III
- BUREAU OF INDIAN STANDARDS (BIS)
- ALL EXTERNAL DOORS FOR DAYCARE SHALL BE PROVIDED WITH DOOR THRESHOLD AND WEATHER SEAL.
- ALL OTHER EXTERNAL DOOR SHALL BE PROVIDED WITH WEATHER SEAL.

UNDERCUT FOR DOORS IS 10 MM EXCEPT FOR THE FOLLOWING DOORS WHERE UNDERCUT IS 15 MM AS PER HVAC DRAWINGS FOR FOLLOWING ROOMS:
-TOILETS
-DWC
-POWER DISTRIBUTION ROOM
-MECHANICAL AND ELECTRICAL ROOMS.
-JANITOR ROOMS

FOR JOINERY SCHEDULES REFER SHEET NO. PJNAB-ATK-ARC-SCH-NA-0011

NOTE;

UP TO 1000MM - 3 HINGES
> THAN 1000MM - 4 HINGES

REVISION CLOUD CHANGES

1. DEADLOCKS UPDATED TO COIN LATCHES FOR TOILET DOORS
2. AUTO LOCKING MECHANISM FOR ALL JANITOR DOORS ADDED
3. ALLEN KEY LOCKSET ADDED TO ACCESS PANEL DOORS
4. NEW IRONMONGERY ADDED FOR E.E. DOORS WITHOUT PANIC TRIMS AND E.E. DOORS WITH HANDLES

NOTE:
ELEVATIONS UPDATED AS PER DOOR SCHEDULE

Drawing Status

ISSUED FOR CONSTRUCTION

Rev.	Date	Description	By	Chk'd	Appd
R1	29/03/2019	ISSUED FOR CONSTRUCTION	BS	CTK	SD
R0	27/02/2019	ISSUED FOR CONSTRUCTION	LH	CTK	SD

SAFETY, HEALTH AND ENVIRONMENTAL INFORMATION

In addition to the hazards/risks normally associated with the types of work detailed on this drawing, note the following:

CONSTRUCTION

MAINTENANCE/CLEANING

DECOMMISSIONING/DEMOLITION

It is assumed that all works will be carried out by a competent contractor working, where appropriate, to an approved method statement

Client

IKEA India Private Limited
DLF Infinity Tower- A
8th Floor, Cyber City Sector 25,
Gurgaon- 122002
Haryana, India

This document/drawing is the property of Inter IKEA Systems B.V. and may, in no way other than for the agreed purpose, be used, copied, reproduced, or in any other manner made known to a third party, and shall after its intended use be returned to Inter IKEA Systems B.V.
© Inter IKEA Systems B.V., [2016]

ATKINS
18th and 19th Floor
Tower C, DLF Cyber Greens,
DLF Cyber City,
DLF Phase- III, Gurgaon,
Haryana- 122 002, India

Tel: +(91) 124 384 7199
Fax: +(91) 124 455 2475

www.atkinsglobal.com

Copyright © Atkins Limited (2013)

Project Title

IKEA
BENGALURU

Drawing Title

JOINERY LEGEND IRONMONGERY
SHEET 2 OF 9
DOORS


Scale	Designed	Drawn	Checked	Authorised
1 : 25	BS	SM	AD	SD

Original Size	Date	Date	Date	Date
A0	22/12/2017	15/07/2018	28/08/2018	07/12/2018


Drawing Number: PJNAB-ATK-ARC-SCH-NA-0013a

Revision: R1


Millimetres 0 10 100

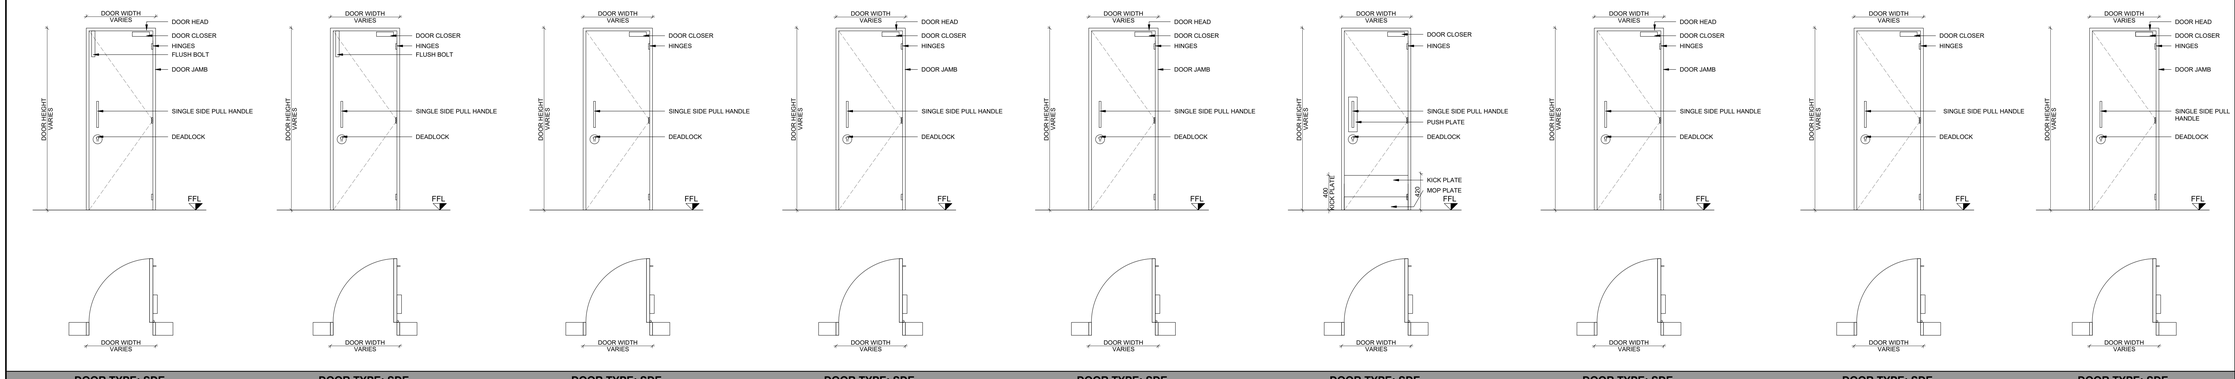


DOOR TYPE: SDE | IRONMONGERY SET: B1
DOOR TYPE: SDE | IRONMONGERY SET: B3
DOOR TYPE: SDE | IRONMONGERY SET: C
DOOR TYPE: SDE | IRONMONGERY SET: C1
DOOR TYPE: SDE | IRONMONGERY SET: C3
DOOR TYPE: SDE | IRONMONGERY SET: C4
DOOR TYPE: SDE | IRONMONGERY SET: C5
DOOR TYPE: SDE | IRONMONGERY SET: E
DOOR TYPE: SDE | IRONMONGERY SET: E1

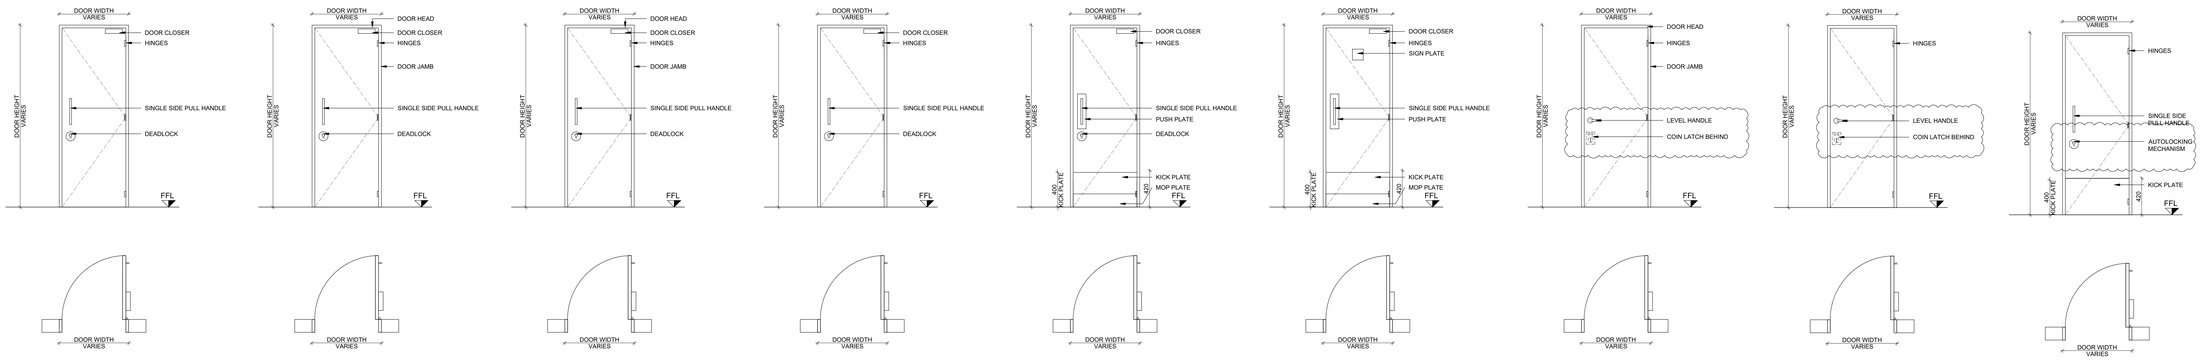

DOOR TYPE: SDE | IRONMONGERY SET: F
DOOR TYPE: SDE | IRONMONGERY SET: F1
DOOR TYPE: SDE | IRONMONGERY SET: F3
DOOR TYPE: SDE | IRONMONGERY SET: F4
DOOR TYPE: SDE | IRONMONGERY SET: G
DOOR TYPE: SDE | IRONMONGERY SET: H
DOOR TYPE: SDE | IRONMONGERY SET: I
DOOR TYPE: SDE | IRONMONGERY SET: I1
DOOR TYPE: SDE | IRONMONGERY SET: J

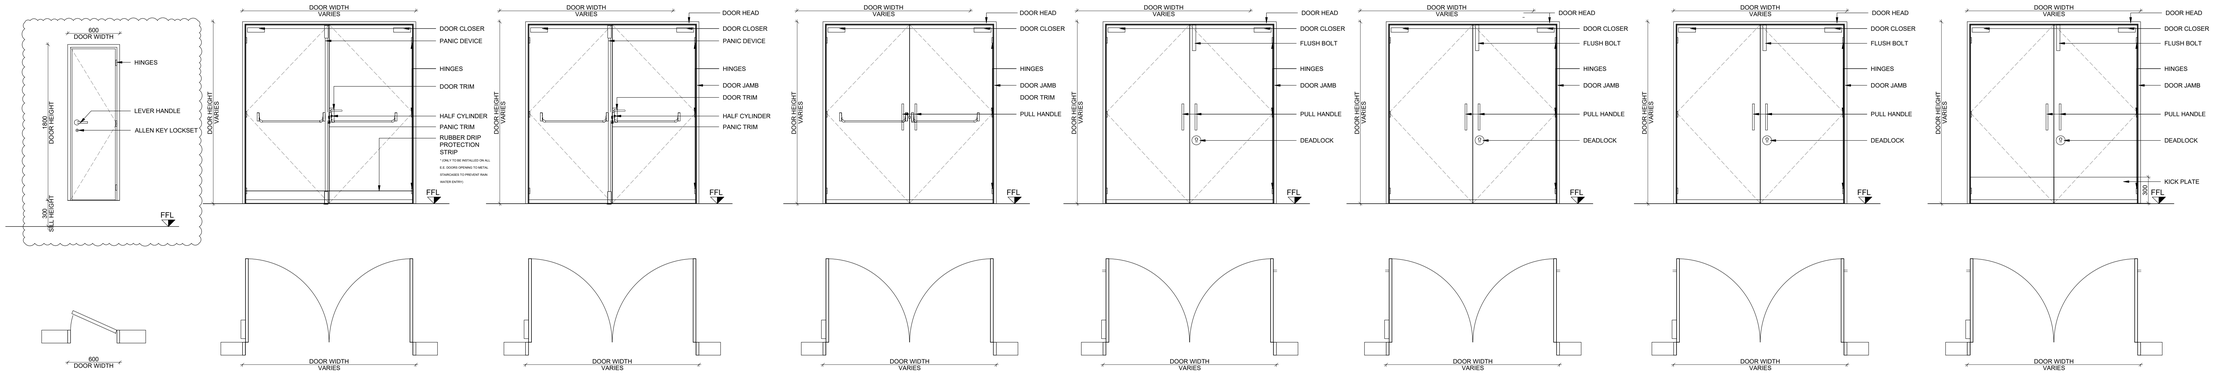

DOOR TYPE: AP | IRONMONGERY SET: K
DOOR TYPE: DDE | IRONMONGERY SET: A
DOOR TYPE: DDE | IRONMONGERY SET: A2
DOOR TYPE: DDE | IRONMONGERY SET: A3
DOOR TYPE: DDE | IRONMONGERY SET: B1
DOOR TYPE: DDE | IRONMONGERY SET: B2
DOOR TYPE: DDE | IRONMONGERY SET: B3
DOOR TYPE: DDE | IRONMONGERY SET: B6

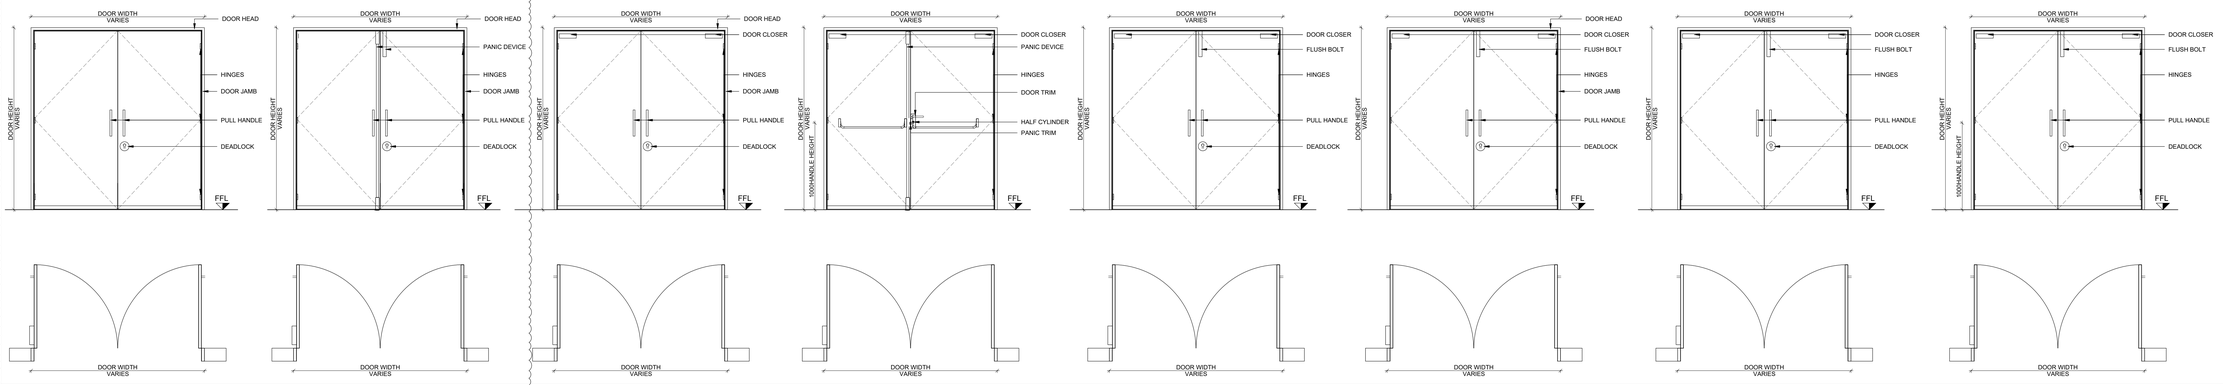

DOOR TYPE: DDE | IRONMONGERY SET: B7
DOOR TYPE: DDE | IRONMONGERY SET: B8
DOOR TYPE: DDE | IRONMONGERY SET: C1
DOOR TYPE: DDE | IRONMONGERY SET: D
DOOR TYPE: DDE | IRONMONGERY SET: D1
DOOR TYPE: DDE | IRONMONGERY SET: D2
DOOR TYPE: DDE | IRONMONGERY SET: D3
DOOR TYPE: DDE | IRONMONGERY SET: D4