


DETAIL VIEW A

NOTES:–
ALL DIMENSIONS ARE IN MM.

NOTES:–
ALL DIMENSIONS ARE IN MM.

A. ABBREVIATION
Wall Opening Width : WOW
Wall Opening Height : WOH
Frame Opening Height : FOH
Frame Opening Width : FOW
Shutter Opening Height : SOH
Shutter Opening Width : SOW

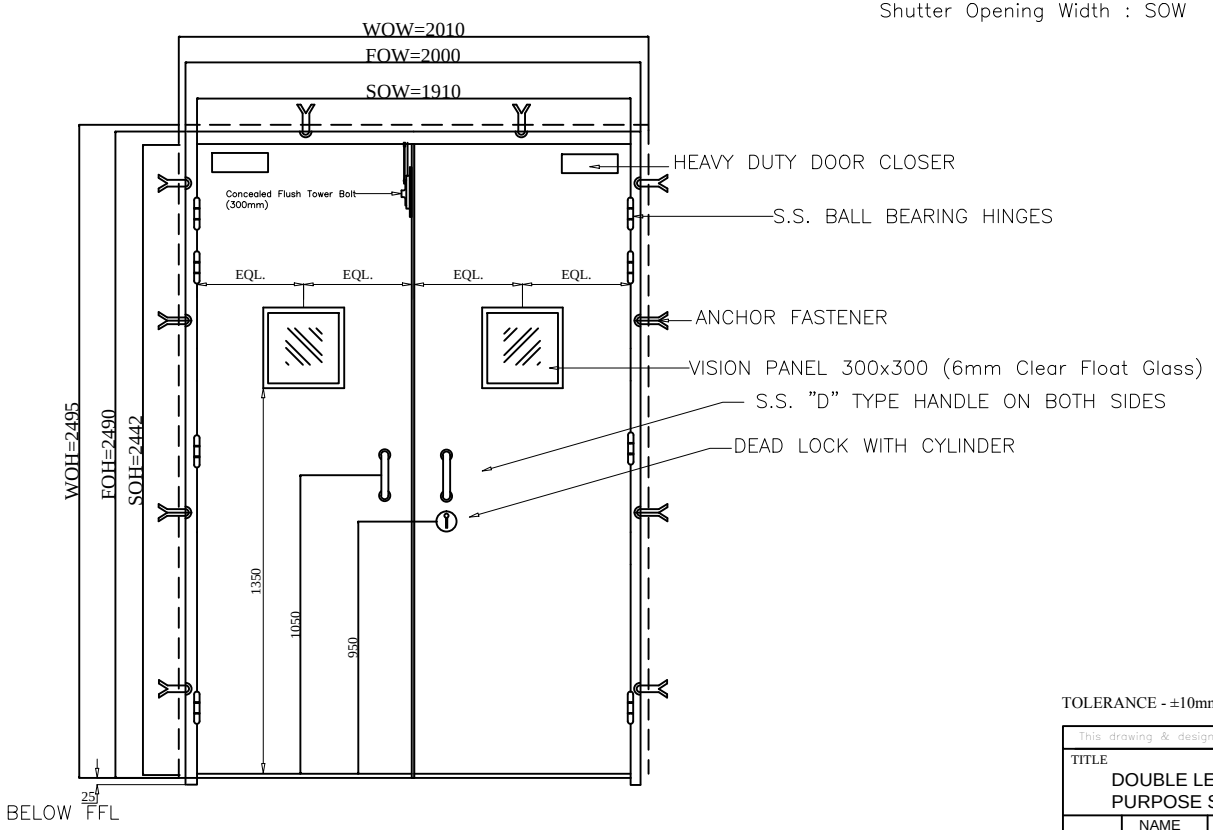

FRAME : G.I. 1.20mm Sheet
SHUTTER : G.I. 0.80mm Sheet

SHUTTER THICKNESS : 40mm
INFILL MATERIAL : MINERAL WOOL
DENSITY 48kg/cm3

PAINT: RAL 9010 (PURE WHITE)
POWDER COATED (DFT 80 Microns min)

SCHEDULE OF HARDWARE

1) S.S. Ball Bearing Hinges - Yale Make - 8 Nos.
2) Dead Lock with Cylinder - Yale Make - 1 Nos.
3) S.S. "D" Type Handle - 2 Sets
4) Heavy Duty Door Closer Yale Make - 2 Nos.
5) Anchor Fastener - 8 x 80mm.
6) Vision Panel with Non - Fire Glass of Size: 300 x 300mm - Clear Float Glass 6mm Thick - 2 Nos.
7) Concealed Flush Tower Bolt - 1 Nos.

TOLERANCE - ±10mm

This drawing & design is the property of NIHVA TECHNOLOGIES. Not to be sold or copied to any other concern.

TITLE				
DOUBLE LEAF GENERAL PURPOSE STEEL DOOR				NIHVA TECHNOLOGIES PVT. LTD. PUNE Tel : 020 66304033 Email:- info@nihva.com Website:- www.nihva.com
	NAME	SIGN	DATE	
DRAWN	P.A		05.06.2020	CLIENT - SYNERGY
CHECK	G.J		05.06.2020	PROJECT-EMBASSY INDUSTRIAL PARKS PVT. LTD.
APPRD.				SITE LOCATION - CHAKAN
If any queries contact : design@nihva.com				DWG. NO. : NIHVA/20-21/0014 REV- 00
ALL DIMENSION ARE IN mm				SCALE: NTS WT: SHEET: 01 OF 01