
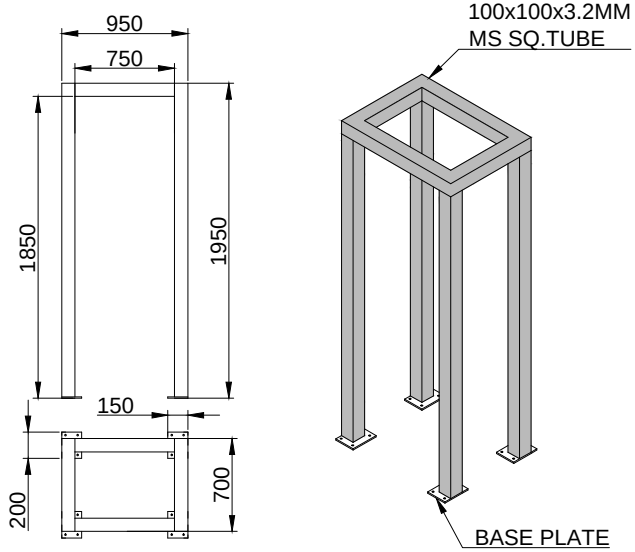



MS POST 1

QTY- 2 NOS

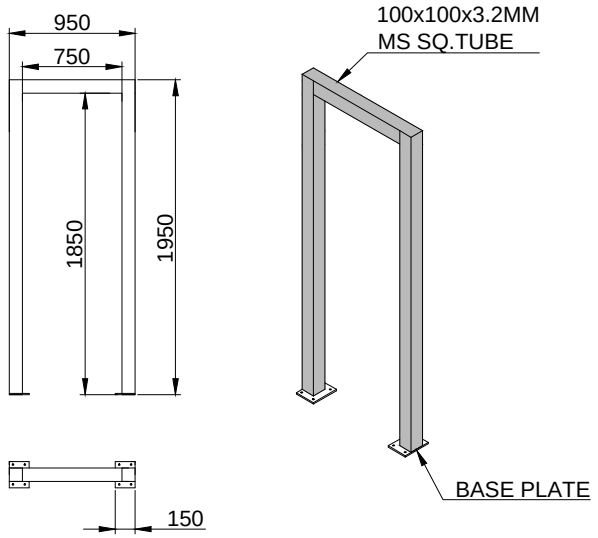


MS POST 2

QTY- 2 NOS

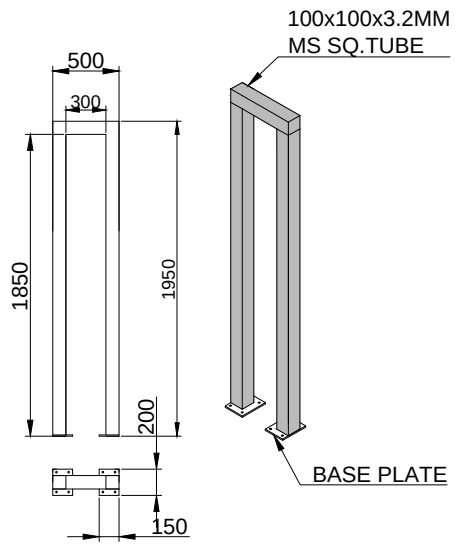


MS POST 3

QTY- 3 NOS

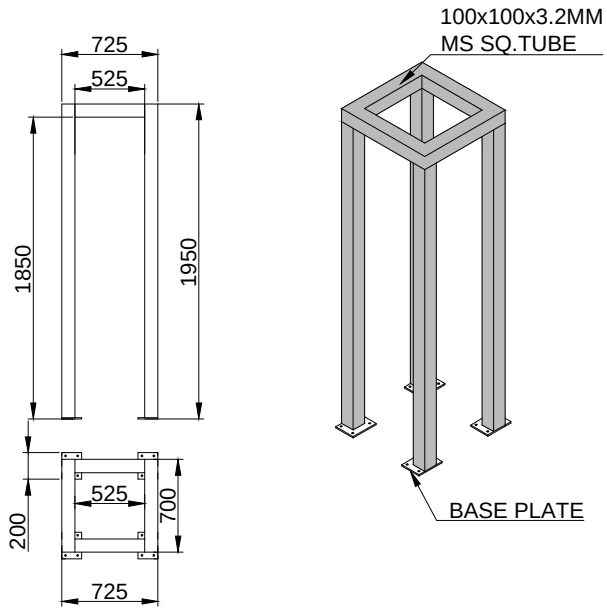

MS POST 4

QTY- 1 NOS

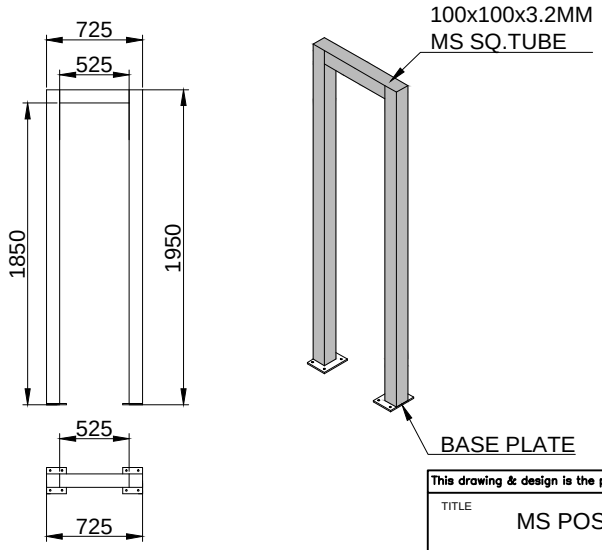

MS POST 5

QTY- 1 NOS

REV NO	DATE	DESCRIPTION
REV -0	31/10/17	INITIAL DRAWING
REV -1	08/11/17	HEIGHT REVISED FROM 2375mm TO 2075mm.
REV -2	09/11/17	HEIGHT REVISED FROM 2075mm TO 1950mm.

TOLERANCE - ±5mm

This drawing & design is the property of NIHVA TECHNOLOGIES. Not to be sold or copied to any other concern.

TITLE: MS POST

	NAME	DATE
DRAWN	OMKAR	31/10/17
CHECK	SHEKHAR	31/10/17
REV.		
APPROVAL	SHEKHAR	31/10/17

If any queries contact : design@nihva.com

ALL DIMENSION ARE IN mm

NIHVA
NIHVA TECHNOLOGIES PVT. LTD.
NIHVA TECHNOLOGIES PVT. LTD. PUNE
Tel : 020 66304033
Email:- info@nihva.com
Website:- www.nihva.com

CLIENT -

PROJECT -

SITE LOCATION -

DWG. NO. : NIHVA/17-18/VDR/0150/R02 | REV- 2

SCALE: NTS | WT: | SHEET: 01 OF 01