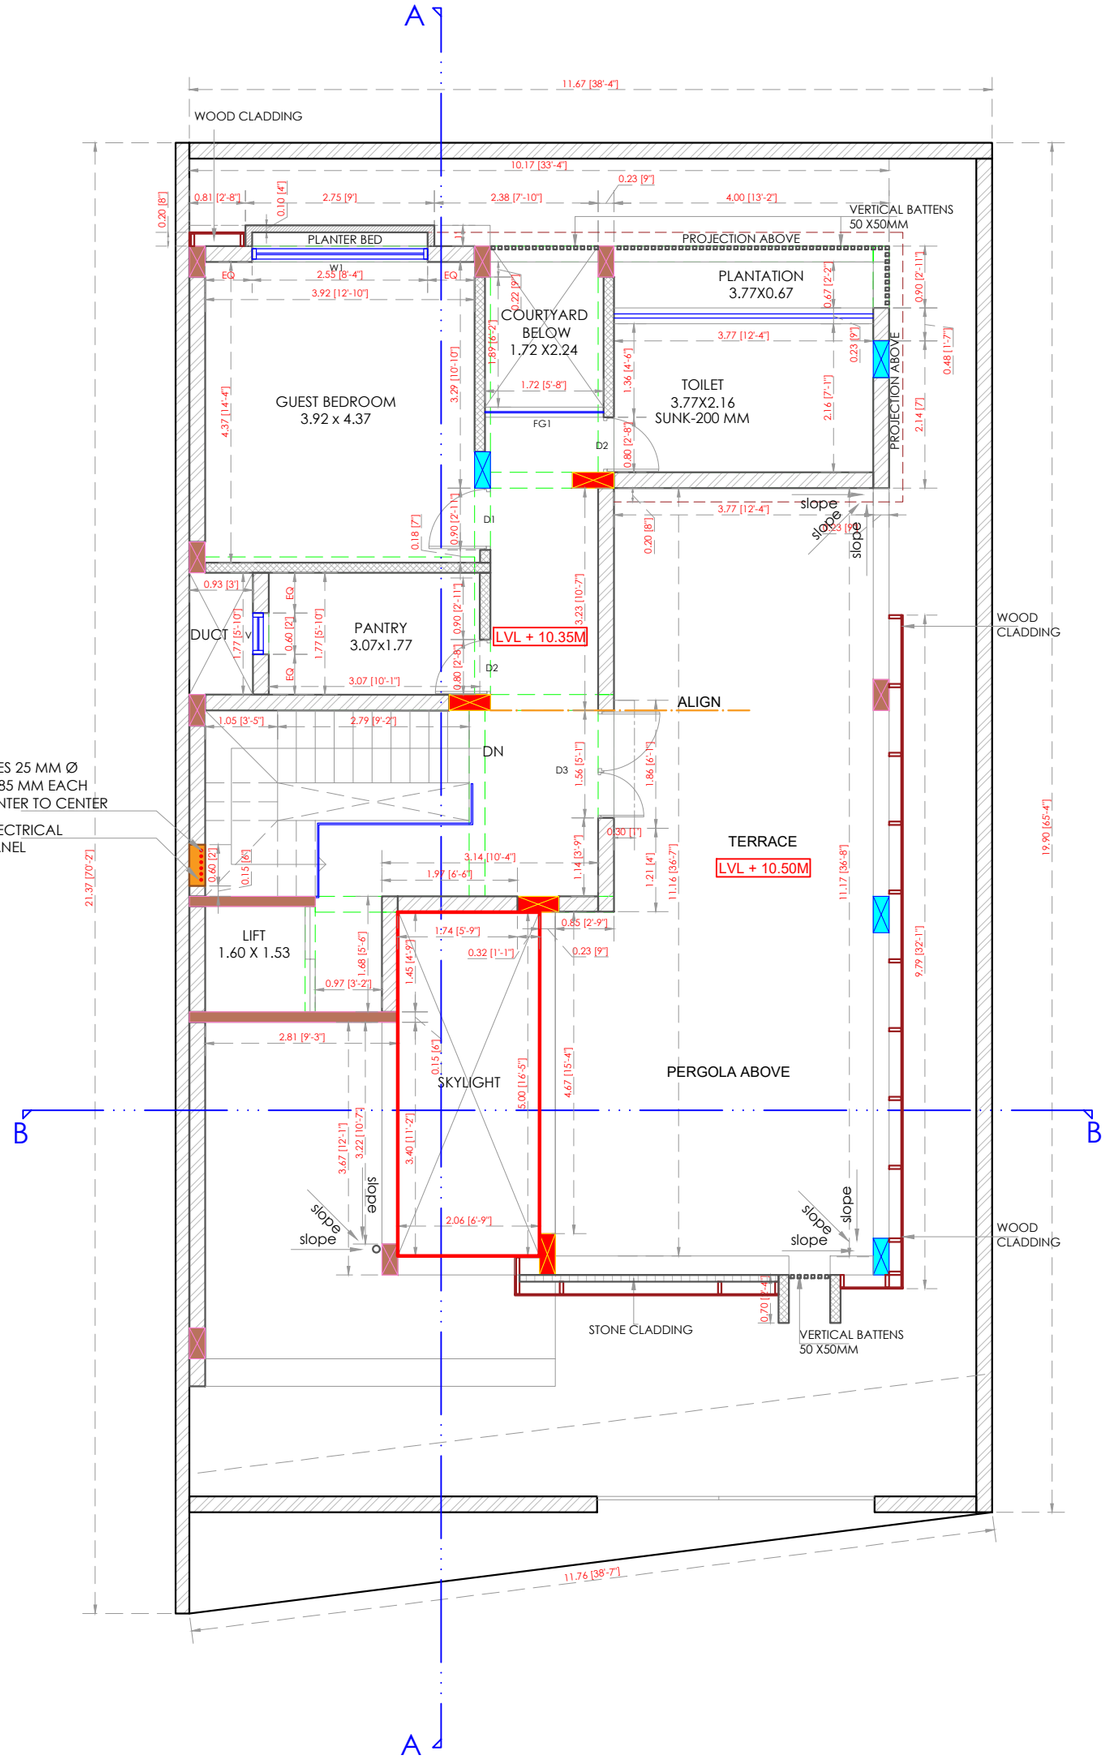


WINDOW SCHEDULE

	SIZE	SILL	LINTEL	LOCATION
W	2.40 X 1.75	0.65	2.40	DINING
W1	2.55 X 1.90	0.50	2.40	PARENT'S,MASTER & GUEST
W2	1.52 X 1.35	1.05	2.40	KITCHEN
W3	0.75 X 1.45	0.95	2.40	STORE
W4	0.75 X 1.75	0.65	2.40	SON'S ROOM
W5	0.60 X 1.90	0.50	2.40	MASTER BEDROOM

VENTILATOR SCHEDULE

	SIZE	SILL	LINTEL	LOCATION
V	0.60 X 0.75	1.65	2.40	TOILETS
V1	0.90 X 1.75	0.65	2.40	SON'S ROOM TOILET

DOOR SCHEDULE

	SIZE	SILL	LINTEL	LOCATION
MD	1.22 X 2.40	0.00	2.40	LIVING ROOM
D	0.95 X 2.40	0.00	2.40	PARENT'S ROOM
D1	0.90 X 2.40	0.00	2.40	LIFT LOBBY,SON'S, MASTER,GUEST
D2	0.80 X 2.40	0.00	2.40	TOILETS,STORE, PANTRY
D3	1.56 X 2.40	0.00	2.40	TERRACE
D4	0.70 X 2.40	0.00	2.40	DUCT ON G.F
SD	2.95 X 2.40	0.00	2.40	LIVING ROOM
SD1	2.55 X 2.40	0.00	2.40	SON'S ROOM
FG	0.60 X 2.40 (fixed glass)	0.00	2.40	SON'S ROOM
FG1	1.72 X 2.40 (fixed glass)	0.00	2.40	PASSAGE (3RD FLOOR)
GD	1.05 X 2.40 (glass door)	0.00	2.40	MASTER ROOM

LOCATION PLAN

LEGENDS

- 230 MM BRICK WALL
- 150 MM BRICK WALL
- 100 MM BRICK WALL
- SUNK

REVISION LIST

SR.NO.	REV NO.	DATE	DESCRIPTION

NOTE

1)THIS DRAWING UNDER COPY-RIGHT OF ARCHITECT AND SHOULD NOT BE USED IN PART OR FULL WITHOUT THE WRITTEN PERMISSION OF ARCHITECT
2)THIS DRAWING,DETAIL,SPECIFICATIONS,QUANTITIES ETC.,ARE BASED ON THE INFORMATION SUPPLIED BY THE OWNER OWNER OF ATTORNEY OLDER,BUILDER,PROMOTOR ETC.
3) ALL PLAN ARE SUBJECT TO SANCTION OF CONCERNED AUTHORITIES.
4) ANY DISCREPANCIES IN THE DRAWING SHOULD BE IMMEDIATELY BROUGHT TO THE NOTICE OF THE ARCHITECT.
5) ALL WORK TO BE CARRIED OUT STRICTLY AS PER DRAWING AND INSTRUCTION GIVEN ON SITE.
6) THE ARCHITECT WILL NOT BE RESPONSIBLE FOR INCORRECT,BAD OR DEFECTIVE WORK.
7) ALL TOILET SLAB TO BE TAKEN SUNK.
8) ALL PROJECTED TERRACE SLAB TO BE TAKEN SUNK.
9) NO COLUMNS,BEAMS,R.C.C. WORK TO BE CHISELLED BROKEN FOR
1)LIFT INSTALLATION.
2)PLUMBING & SANITATION.
3)ELECTRICAL CONDUCING.
4)LEVELING OF SURFACES ANY OTHER.

DRAWING NAME:
THIRD FLOOR PLAN


CLIENT:
MR. SHELKE

PROJECT TITLE :
PROPOSED BUNGALOW AT AURANGABAD.

CHECKED BY	YASH
DRAWN BY	ASMITA
SCALE	NTS
PROJECT CODE	P-AP-(22)-04
DATE	13/01/2023

N

ARCHITECT
Ar. Yash Chudiwal
Ar. Sejal Bamb Chudiwal
57/1, Dhole Patil Farm Road, Kharadi, Pune- 411014
Contact: +91-9890181691
Email: info@ysarchitects.in
Y:S ARCHITECTS

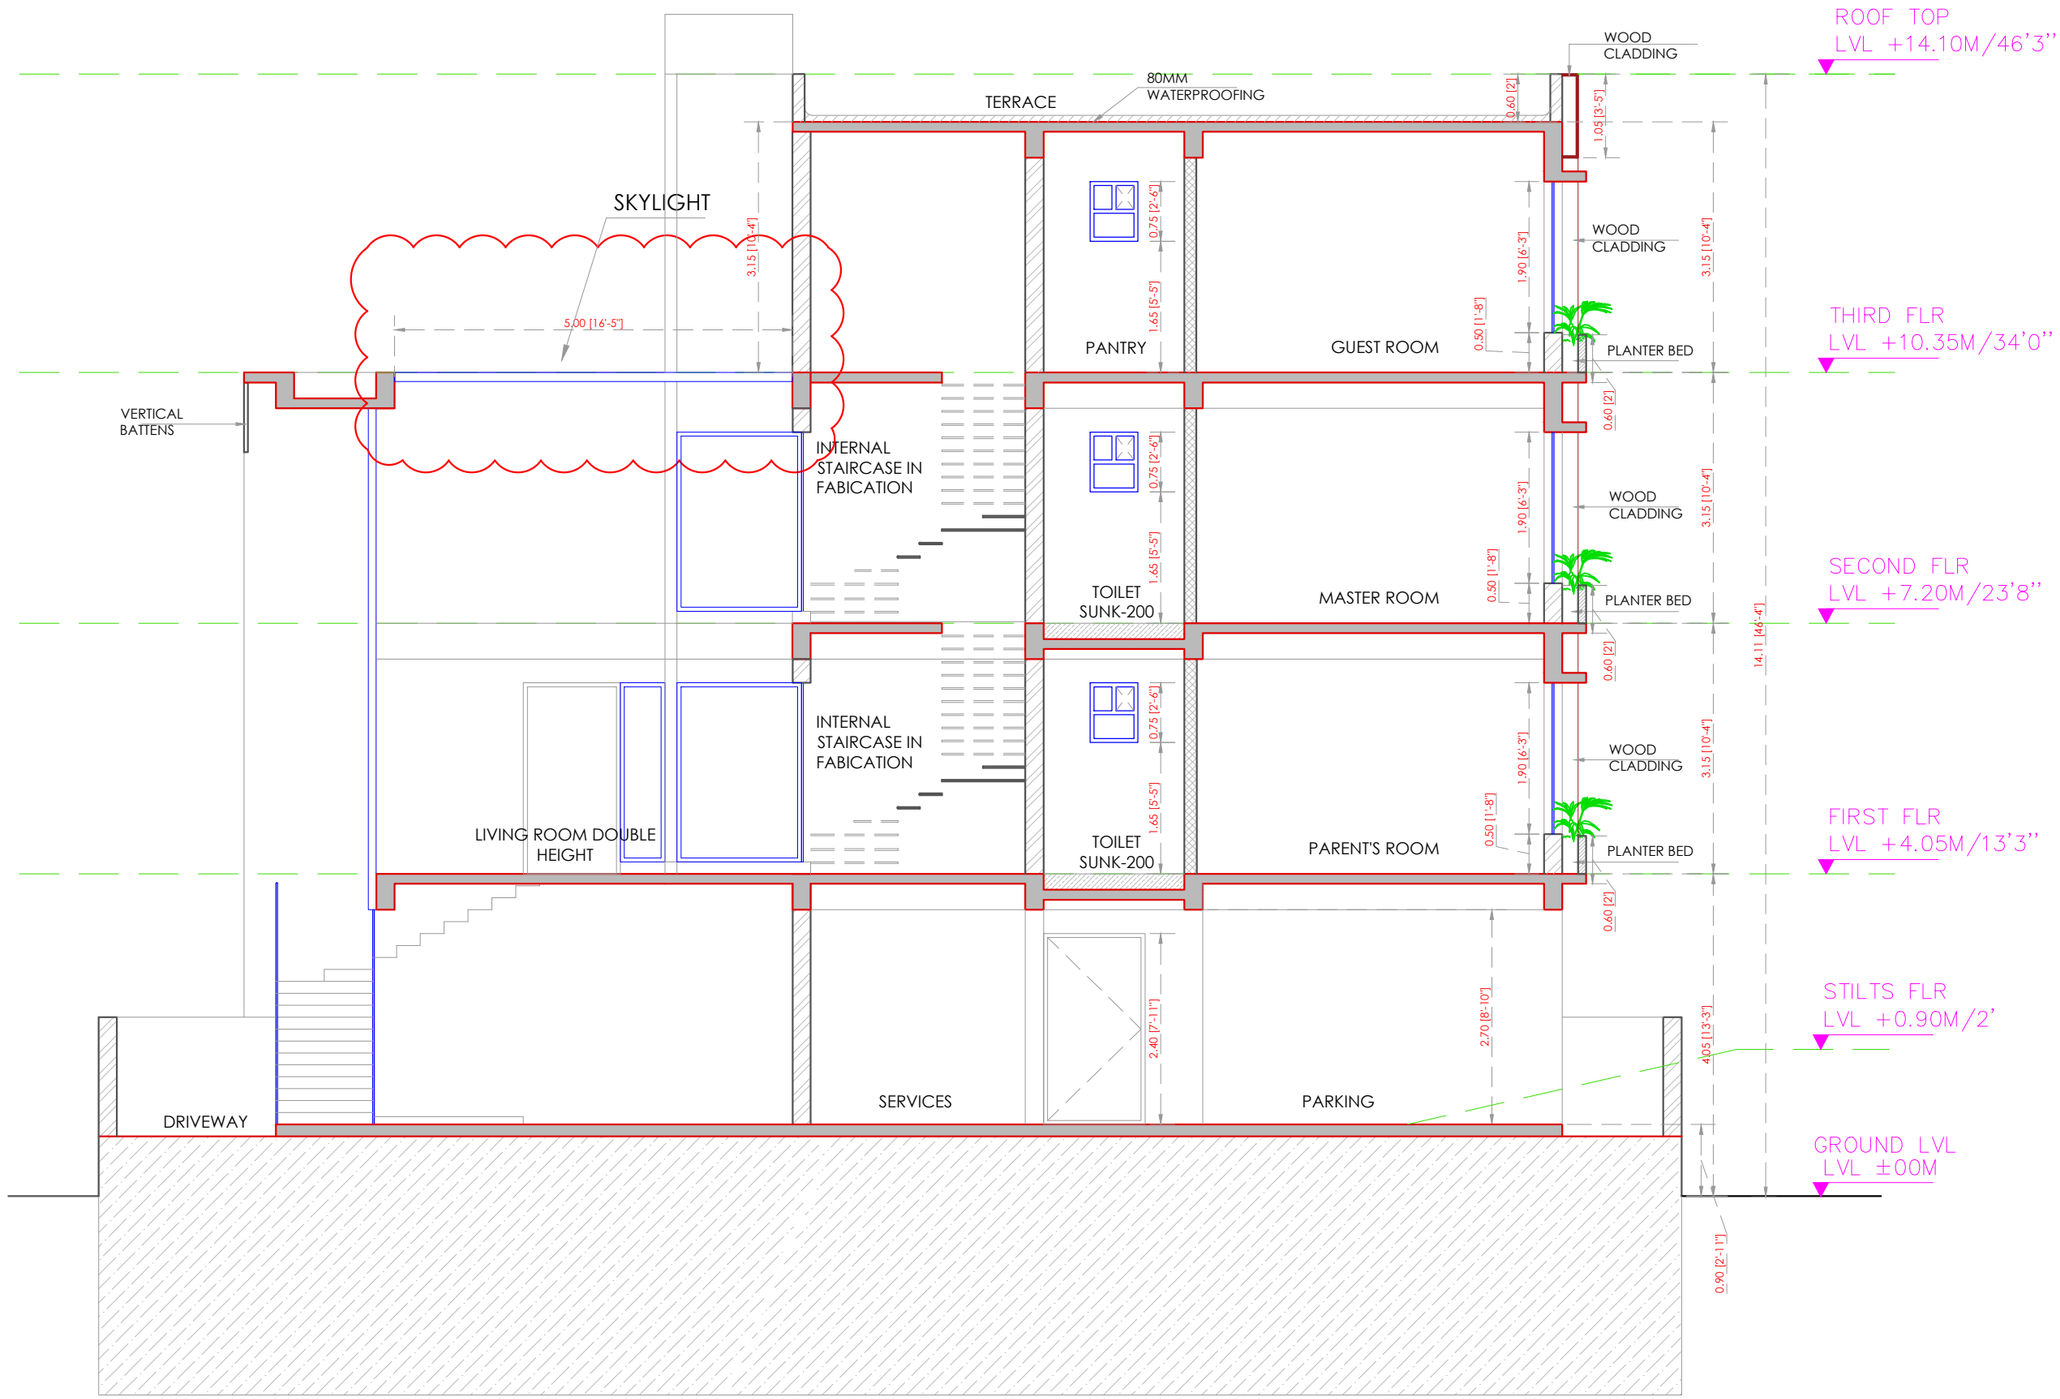

SECTION AA'

LOCATION PLAN

LEGENDS

- 230 MM BRICK WALL
- 150 MM BRICK WALL
- 100 MM BRICK WALL
- SUNK

REVISION LIST

SR.NO.	REV NO.	DATE	DESCRIPTION

NOTE

1) THIS DRAWING UNDER COPY-RIGHT OF ARCHITECT AND SHOULD NOT BE USED IN PART OR FULL WITHOUT THE WRITTEN PERMISSION OF ARCHITECT
2) THIS DRAWING,DETAIL,SPECIFICATIONS,QUANTITIES ETC.,ARE BASED ON THE INFORMATION SUPPLIED BY THE OWNER OWNER OF ATTORNEY OLDER,BUILDER,PROMOTOR ETC.
3) ALL PLAN ARE SUBJECT TO SANCTION OF CONCERNED AUTHORITIES.
4) ANY DISCREPANCIES IN THE DRAWING SHOULD BE IMMEDIATELY BROUGHT TO THE NOTICE OF THE ARCHITECT.
5) ALL WORK TO BE CARRIED OUT STRICTLY AS PER DRAWING AND INSTRUCTION GIVEN ON SITE.
6) THE ARCHITECT WILL NOT BE RESPONSIBLE FOR INCORRECT,BAD OR DEFECTIVE WORK.
7) ALL TOILET SLAB TO BE TAKEN SUNK.
8) ALL PROJECTED TERRACE SLAB TO BE TAKEN SUNK.
9) NO COLUMNS,BEAMS,R.C.C. WORK TO BE CHISELLED BROKEN FOR
   1) LIFT INSTALLATION.
   2) PLUMBING & SANITATION.
   3) ELECTRICAL CONDUCING.
   4) LEVELING OF SURFACES ANY OTHER.

DRAWING NAME:
SECTION AA'

CLIENT:
MR. SHELKE

PROJECT TITLE :
PROPOSED BUNGALOW AT AURANGABAD.

CHECKED BY	YASH
DRAWN BY	ASMITA
SCALE	NTS
PROJECT CODE	P-AP-(22)-04
DATE	13/01/2023


N

ARCHITECT

Ar. Yash Chudiwal
Ar. Sejal Bamb Chudiwal

57/1, Dhole Patil Farm Road, Kharadi,
Pune- 411014
Contact: +91-9890181691
Email: info@ysarchitects.in

Y:S ARCHITECTS

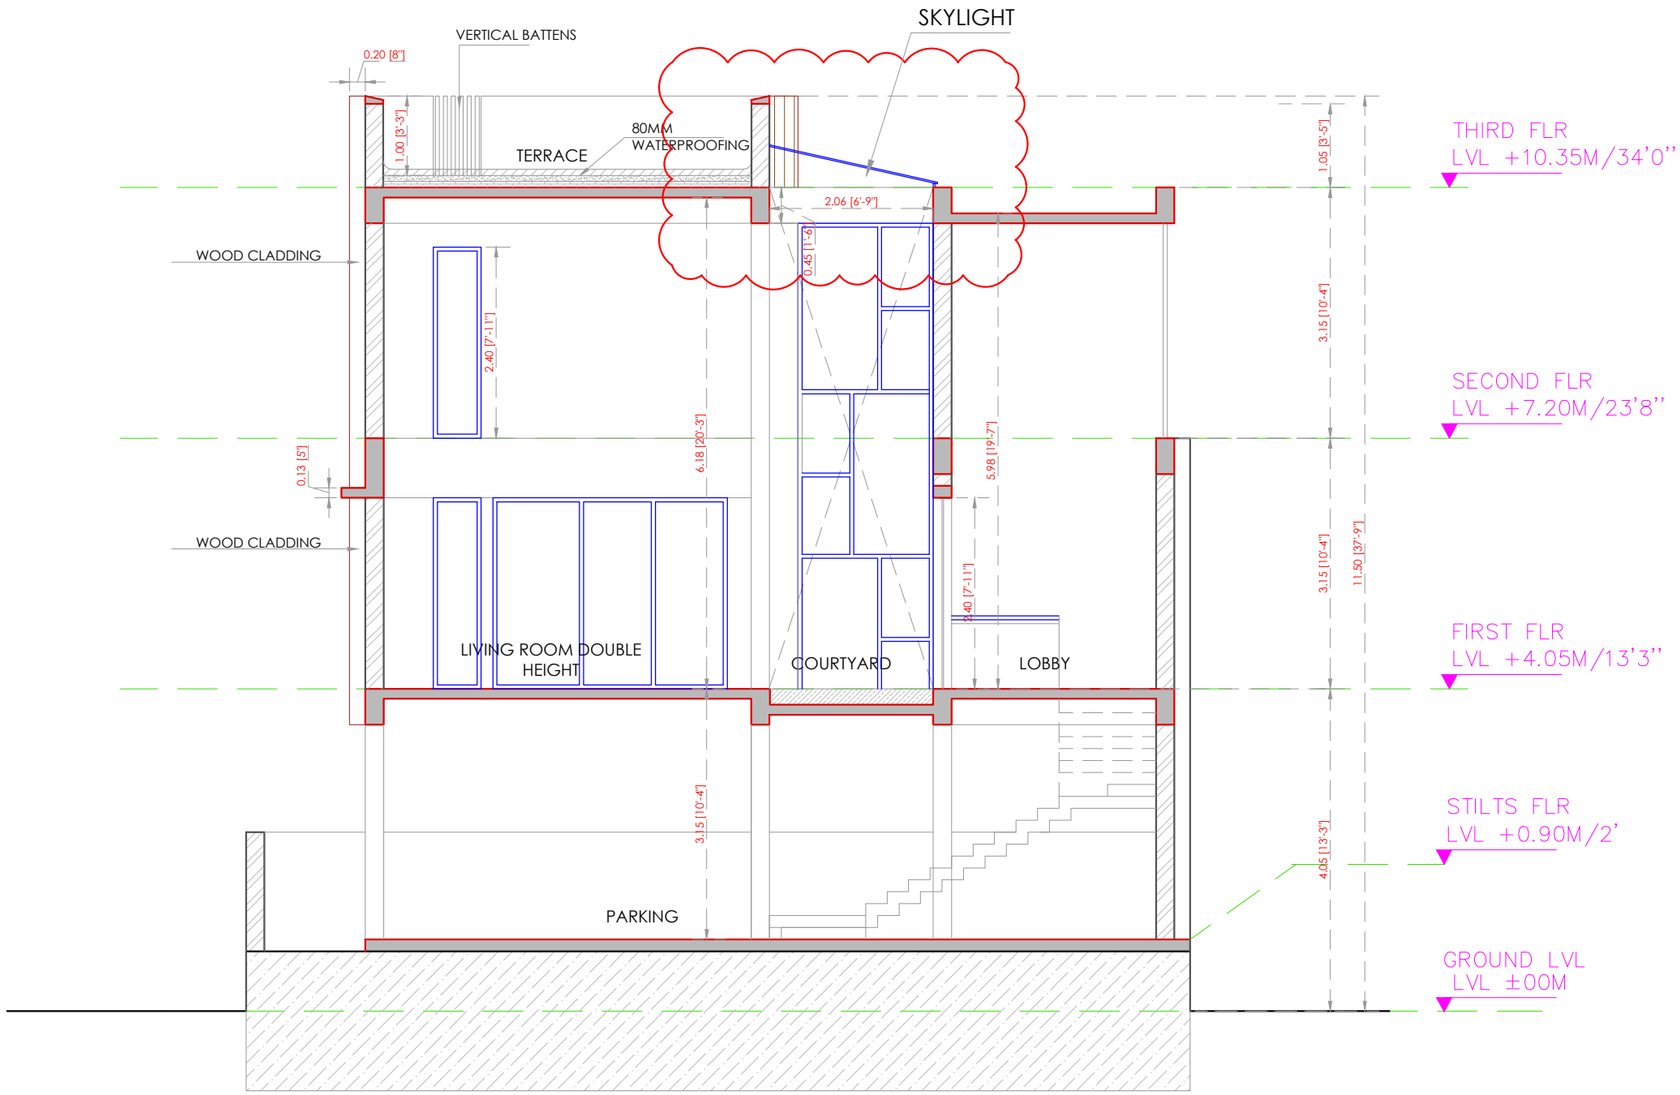

SECTION BB'

LOCATION PLAN

LEGENDS

- 230 MM BRICK WALL
- 150 MM BRICK WALL
- 100 MM BRICK WALL
- SUNK

REVISION LIST

SR.NO.	REV NO.	DATE	DESCRIPTION

NOTE

1) THIS DRAWING UNDER COPY-RIGHT OF ARCHITECT AND SHOULD NOT BE USED IN PART OR FULL WITHOUT THE WRITTEN PERMISSION OF ARCHITECT
2) THIS DRAWING,DETAIL,SPECIFICATIONS,QUANTITIES ETC.,ARE BASED ON THE INFORMATION SUPPLIED BY THE OWNER OWNER OF ATTORNEY OLDER,BUILDER,PROMOTOR ETC.
3) ALL PLAN ARE SUBJECT TO SANCTION OF CONCERNED AUTHORITIES.
4) ANY DISCREPANCIES IN THE DRAWING SHOULD BE IMMEDIATELY BROUGHT TO THE NOTICE OF THE ARCHITECT.
5) ALL WORK TO BE CARRIED OUT STRICTLY AS PER DRAWING AND INSTRUCTION GIVEN ON SITE.
6) THE ARCHITECT WILL NOT BE RESPONSIBLE FOR INCORRECT,BAD OR DEFECTIVE WORK.
7) ALL TOILET SLAB TO BE TAKEN SUNK.
8) ALL PROJECTED TERRACE SLAB TO BE TAKEN SUNK.
9) NO COLUMNS,BEAMS,R.C.C. WORK TO BE CHISELLED BROKEN FOR
   1) LIFT INSTALLATION.
   2) PLUMBING & SANITATION.
   3) ELECTRICAL CONDUCING.
   4) LEVELING OF SURFACES ANY OTHER.

DRAWING NAME:
SECTION BB'

CLIENT:
MR. SHELKE

PROJECT TITLE :
PROPOSED BUNGALOW AT AURANGABAD.

CHECKED BY	YASH
DRAWN BY	ASMITA
SCALE	NTS
PROJECT CODE	P-AP-(22)-04
DATE	13/01/2023

N

ARCHITECT

Ar. Yash Chudiwal
Ar. Sejal Bamb Chudiwal

57/1, Dhole Patil Farm Road, Kharadi,
Pune- 411014
Contact: +91-9890181691
Email: info@ysarchitects.in

Y:S ARCHITECTS