



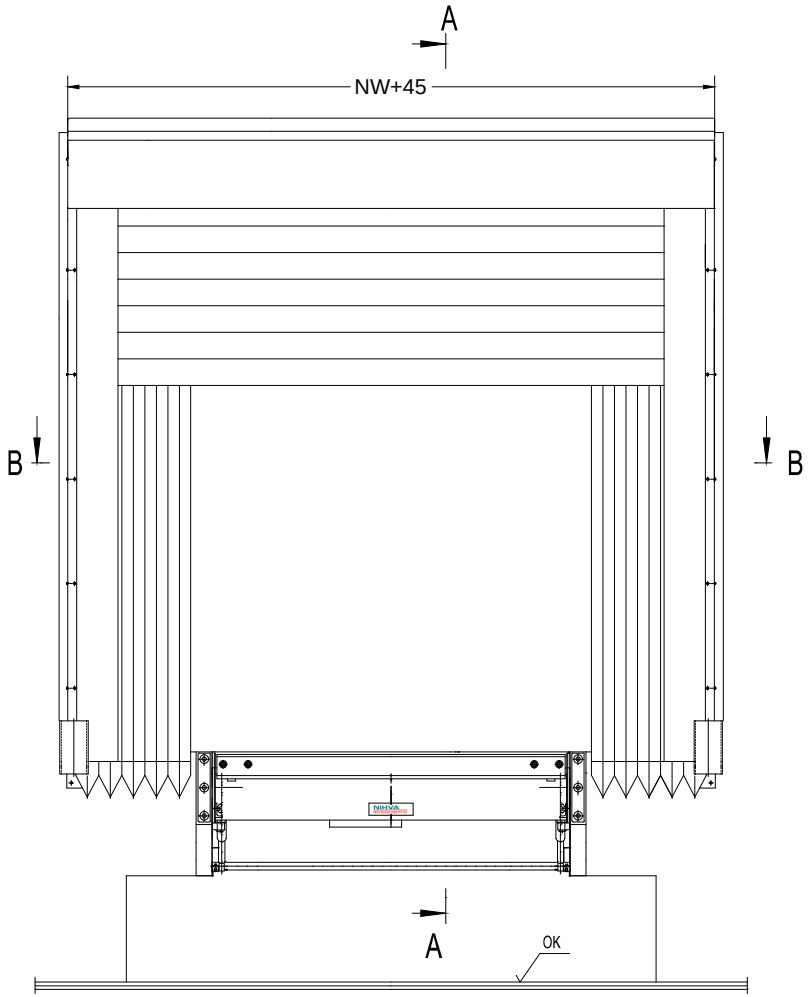


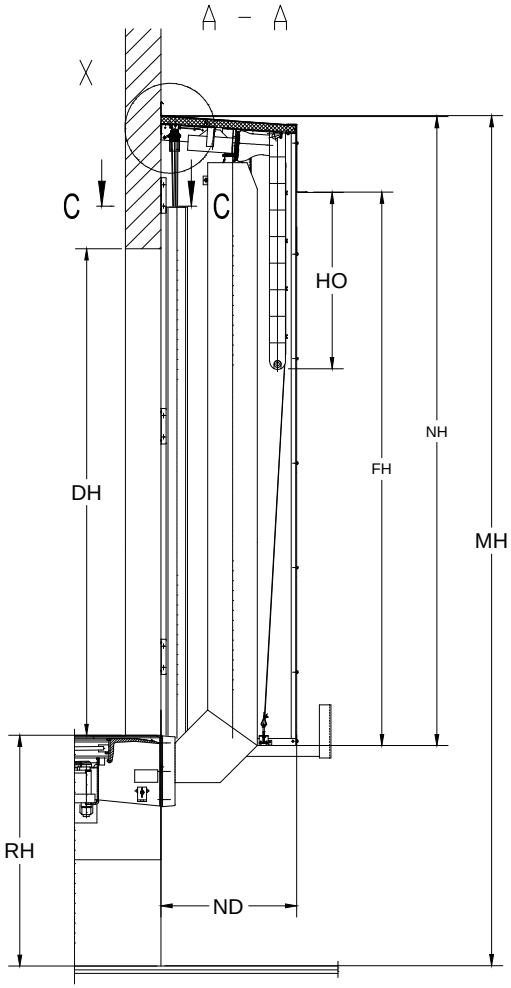

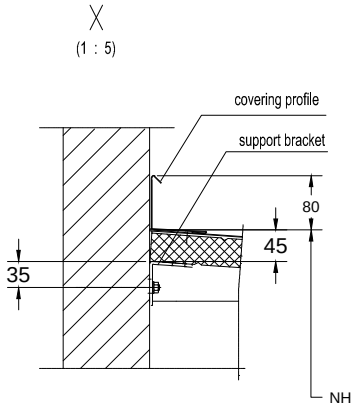

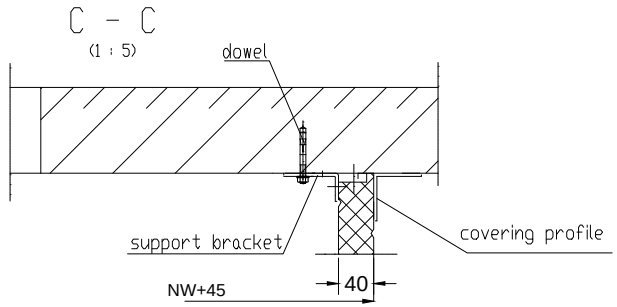

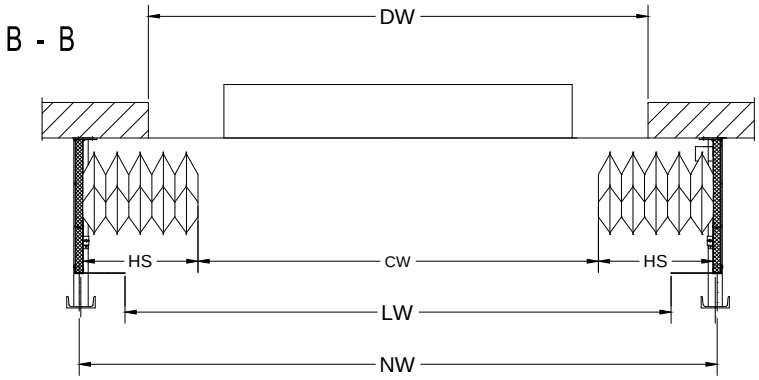

NOTE- SELECTED DOCK SHELTER IS ONLY FOR 20/40 FT.CONTAINER.

Abb.	Dimension	Value(mm)
NW	Nominal width	3600
NH	Nominal height	3755
HS	Side bag extension	650
FH	Free height above level	3300
HO	Top bag extension	1000
ND	Nominal depth	770
MH	Installation height	4955
LW	Clear width(max)	3000
CW	Clear width(min)	2300
DW	Clear Structure width	3100

This drawing & designing is the property of NIHVA TECHNOLOGIES. Not to be sold or copied to any other concern.

TITLE

DOCK SHELTER

NIHVA TECHNOLOGIES PVT. LTD.
NIHVA TECHNOLOGIES PVT. LTD. PUNE
Tel : 020 66304033
Email:- info@nihva.com
Website:- www.nihva.com

	SIGN	DATE
DRAWN	SURAJ	08/04/17
CHECK	SAGAR P.	08/04/17
REV.		
APPROVAL		

If any queries contact : projects@nihva.com

ALL DIMENSION ARE IN mm

CLIENT - ITC

PROJECT -

SITE - GUNTUR,A.P

DWG. NO. : NIHVA/17-18/0005/R01

SCALE: NTS | WT: | SHEET: 01 OF 01