




INSIDE ELEVATION

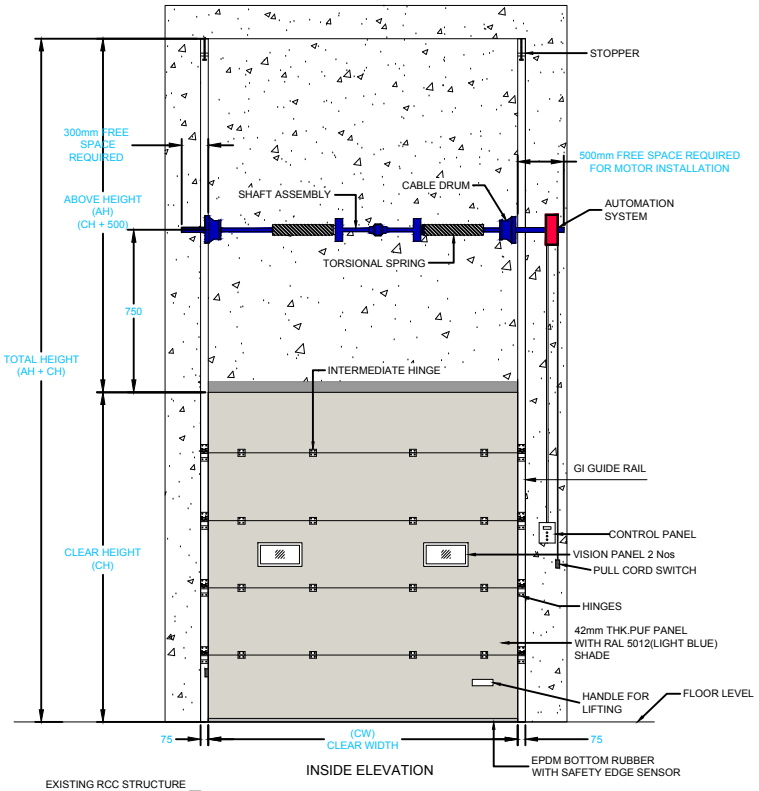

PLAN

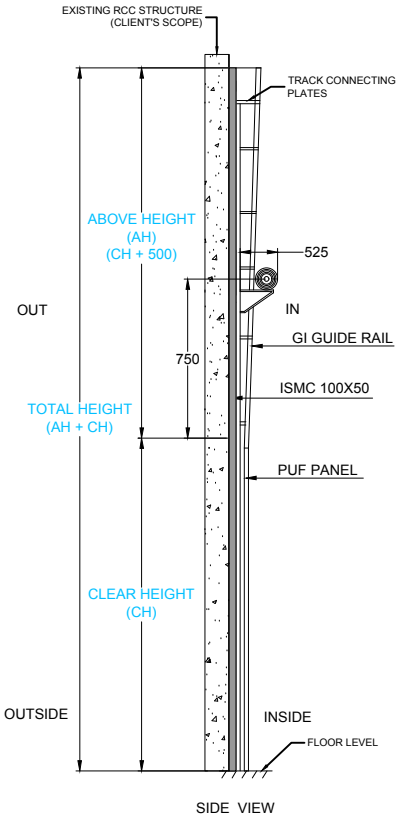

SIDE VIEW

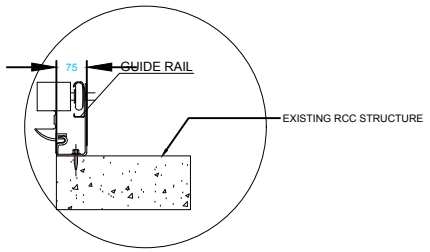

TRACK DETAILS

DIMENSION :

CLEAR WIDTH (CW)	CLEAR HEIGHT (CH)	QUANTITY
5000 mm	4000 mm	01

TECHNICAL DATA :

COMPONENTS	MATERIALS	SPECIFICATIONS
DOOR PANELS	GI & PUF	42mm CFC- FREE POLYURETHANE WITH 0.5mm THK, GI PRECOATED PANELS.
DOOR HINGE	——	HEAVY DUTY HINGES FOR INTERLOCKING OF PANELS
SHAFT ASSEMBLY	STD.	TORSIONAL SPRING WITH SHAFT & BEARING PLATES
FINISH		PANELS ARE IN RAL 5012(LIGHT BLUE)

ACCESSORIES-
1. SAFETY EDGE SENSOR.

IMPORTANT NOTES:
1. REQUIRED STRUCTURE FOR DOOR SHALL BE IN CLIENT'S SCOPE.
2.SINGLE PHASE POWER SUPPLY REQUIRED AT DOOR LOCATION.
3.ALL CIVIL WORK SHALL BE CLIENT'S SCOPE.

NIHVA TECHNOLOGIES PVT. LTD.
NIHVA TECHNOLOGIES PVT. LTD. PUNE
Email:- info@nihva.com
Website:- www.nihva.com

TITLE:

SECTIONAL DOOR (**VERTICAL LIFTING SECTIONAL DOOR WITH FIRE ALARM INTERLOCKING SYSTEM**)

CLIENT'S APPROVAL :

CLIENT - SCON PROJECTS PVT LTD.

PROJECT - INNOVATEC INDIA PVT. LTD.

SITE LOCATION - SANAND

DWG. NO. : NIHVA/20-21/0091 | REV- 0

SCALE: NTS | WT: | SHEET:1 OF 1

	NAME	DATE	SIGN
DRAWN	S.M.S.	19.11.2020	
CHECK	ARJUN	19.11.2020	
APPROVAL			

If any queries contact : projectsupport@nihva.com

NOTE: ALL DIMENSIONS ARE IN mm

THIS DRAWING & DESIGNING IS THE PROPERTY OF NIHVA TECHNOLOGIES. NOT TO BE SOLD OR COPIED TO ANY OTHER CONCERN.