




SIDE VIEW

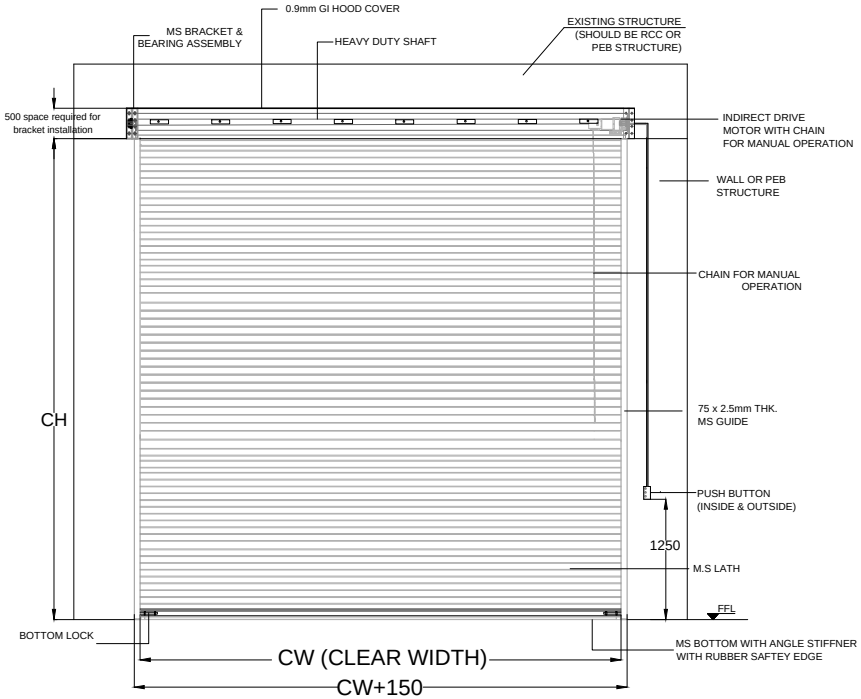


ELEVATION

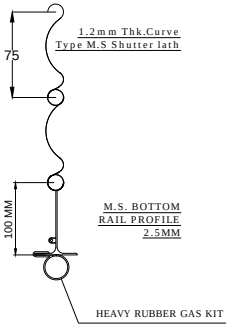

M.S. BOTTOM RAIL PROFILE 2.5MM

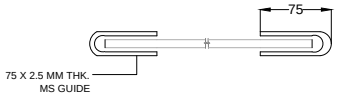

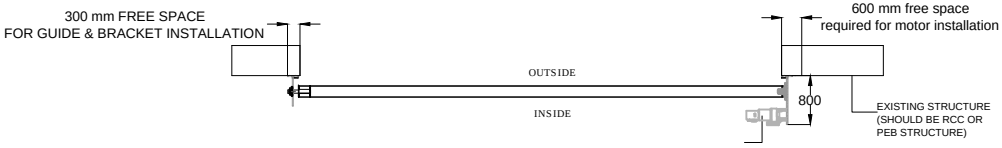

PLAN

NOTE:
1 REQUIRED STRUCTURE FOR SHUTTER WILL BE IN NIHVA SCOPE.
2.PAINT FINISH: EPOXY PAINTED OF APPROVED COLOR RAL CODE - RAL 7036 (PLATINIUM GREY)
3.SINGLE PHASE. 3CORE 1.2SQ. CABLE REQUIRED AT SITE (CLIENT'S SCOPE).
4.SAFETY PHOTOCELL FOR EACH OF DOOR.
5.YELLOW FLASHING LIGHT WITH ALARM FOR EACH OF DOOR.

TOLERANCE - ±10mm

CLEAR WIDTH	CLEAR HEIGHT	LOCATION	QTY.
3500mm	4400mm	Ware House East Side - 3 Nos	03 NOS
3200mm	3000mm	Pin Joint Loading Dock area- 2 Nos & Electrical Room - 1 No	03 NOS
3200mm	3500mm	Ware House Front Dock area - 1 No	01 NO

This drawing & design is the property of NIHVA TECHNOLOGIES. Not to be sold or copied to any other concern.

TITLE
MOTORISED ROLLING SHUTTER

NIHVA TECHNOLOGIES PVT. LTD.
NIHVA TECHNOLOGIES PVT. PUNE
Tel : 020 66304033
Email:- info@nihva.com
Website:- www.nihva.com

	NAME	SIGN	DATE
DRAWN	P.V.A		18.07.2019
CHECK	V.M.T		18.07.2019
APPRD.			

If any queries contact : design@nihva.com

ALL DIMENSION ARE IN mm

CLIENT - LM WIND POWER BLADES

PROJECT -

SITE LOCATION - DABASPETH, BANGLORE.

DWG. NO. : NIHVA/19-20/0051 REV- 0

SCALE: NTS WT: SHEET: 01 OF 01