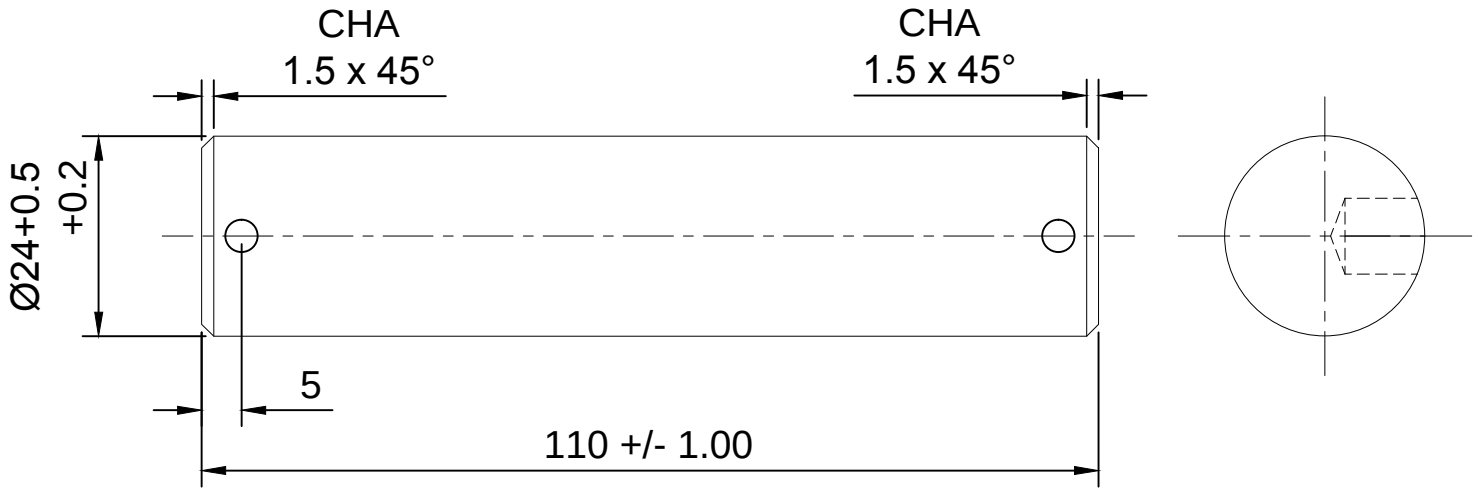


NOTE:~ MTL : EN8

Ø24 X 113L = 14 NOS (HARDENING & GRINDING)

This drawing & design is the property of NIHVA TECHNOLOGIES. Not to be sold or copied to any other concern.

TITLE

MAINTENANCE STOPPER

NIHVA TECHNOLOGIES PVT. LTD.

NIHVA TECHNOLOGIES PVT. PUNE
Tel : 020 66304033
Email:- info@nihva.com
Website:- www.nihva.com

	NAME	SIGN	DATE
DRAWN	PRADEEP		02.05.2018
CHECK	PRADEEP		02.05.2018
APPRD.	PRADEEP		02.05.2018

If any queries contact : design@nihva.com

ALL DIMENSION ARE IN mm

CLIENT -

PROJECT - DLIK1005

SITE LOCATION -

DWG. NO. :NIHVA/18-19/DLIK1005_009_R1

SCALE: NTS | WT: | REV- 0