



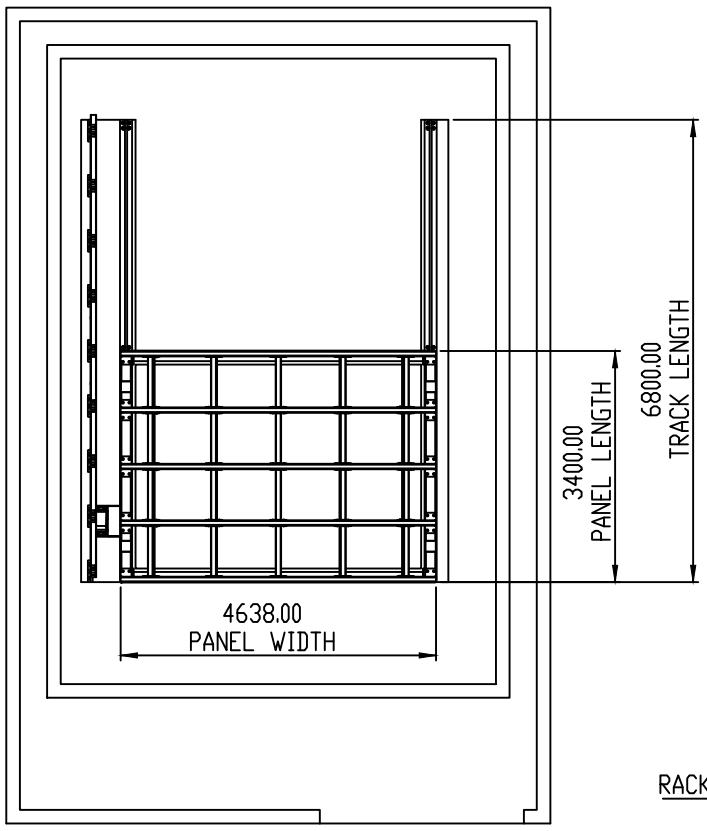


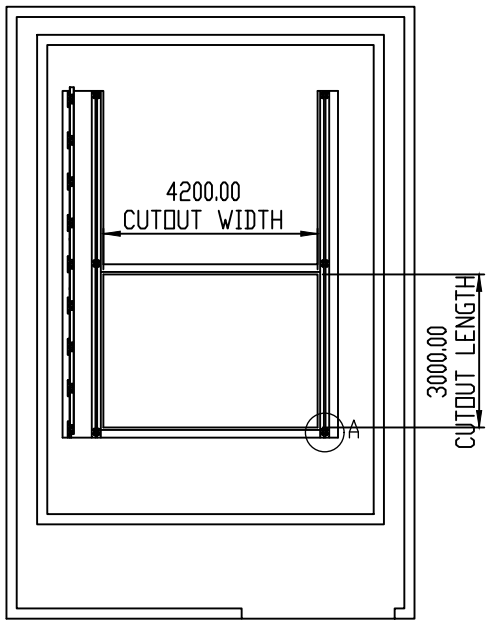

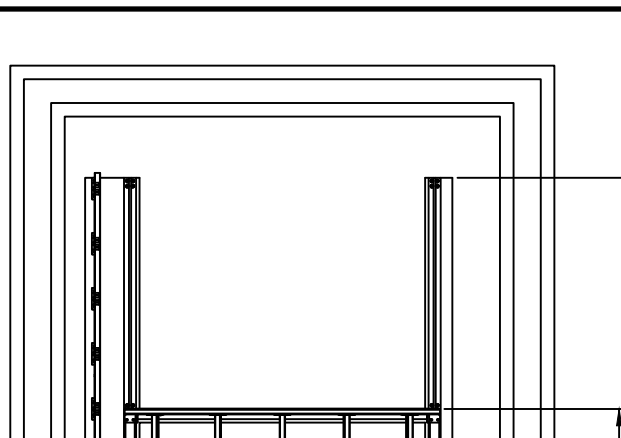

 


DETAIL B
SCALE 1 : 25

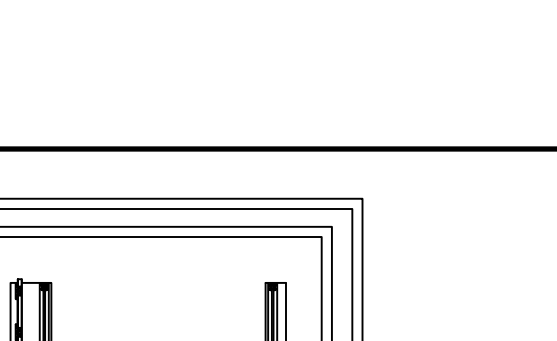

DETAIL A
SCALE 1 : 12


TITLE - RETRACTABLE ROOF				NIHVA TECHNOLOGIES PVT.LTD.PUNE Website - www.nihva.com
DWG NO - NTPL268-PM			QTY - 1	
	NAME	SIGNATURE	DATE	PROJECT NO - NTPL268-PM- AD
DRAWN	S.W		03-03-2025	PRODUCT - RETRACTABLE ROOF
CHK'D	P.M.		03-03-2025	SITE LOCATION - GUJARAT
APPV'D	V.T.		03-03-2025	
if any queries contact supportautomation@nihva.com				REVISION -
ALL DIMENSION ARE IN mm			A3	SCALE - SHEET 1 OF 2

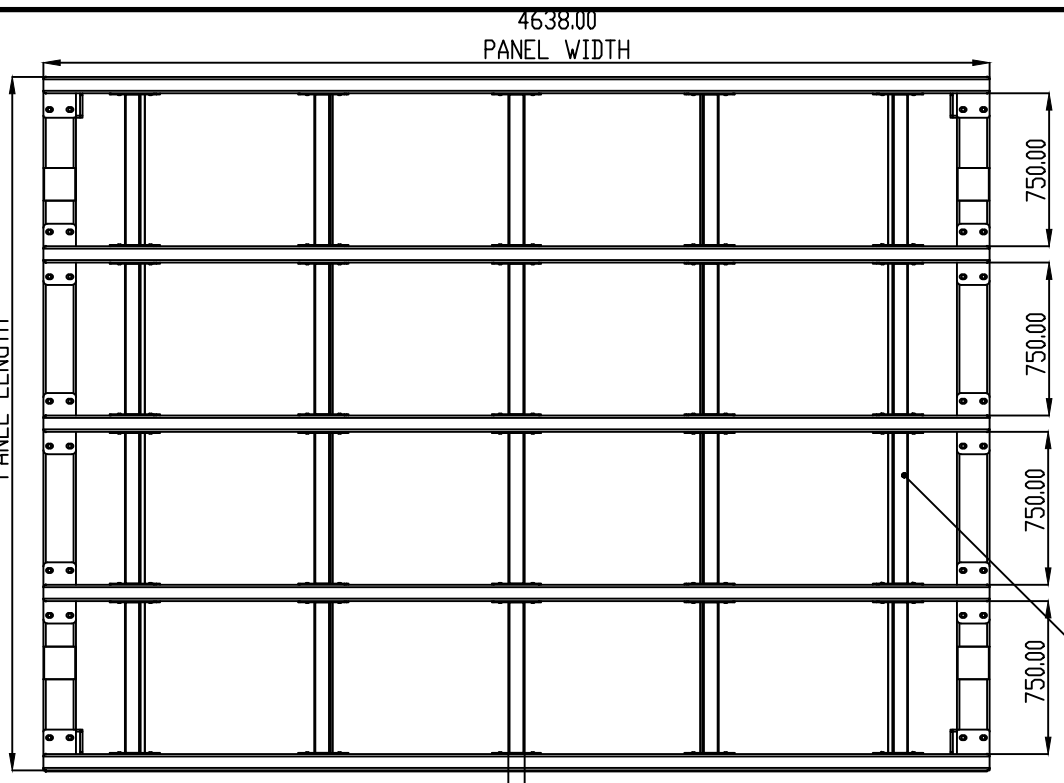


TECHNICAL SPECIFICATION

WIND LOAD :- 4 KN/ SQURE METER
LIVE LOAD :- 1.5 KN/ SQURE METER
DEAD LOAD :- 520 KG

INTERMEDIATE SUPPORT MS TUBE :- 80X80X3 MM

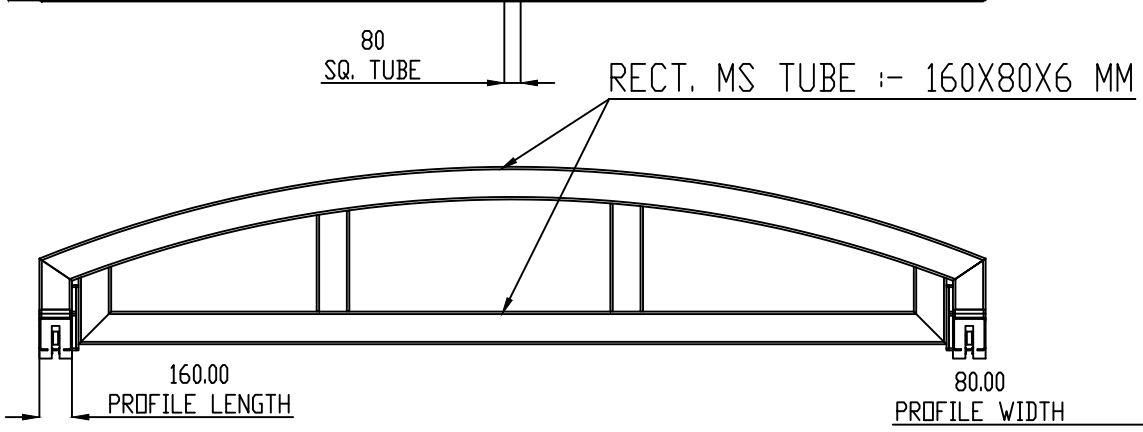

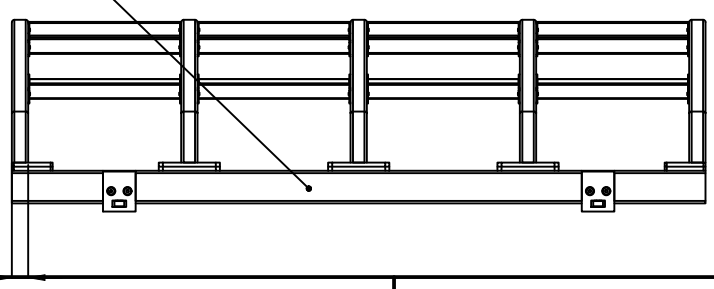

TITLE - RETRACTABLE ROOF				NIHVA TECHNOLOGIES PVT.LTD.PUNE Website - www.nihva.com
DWG NO - NTPL268-PM			QTY - 1	
	NAME	SIGNATURE	DATE	PROJECT NO - NTPL268-PM- AD
DRAWN	S.W		03-03-2025	PRODUCT - RETRACTABLE ROOF
CHK'D	P.M.		03-03-2025	SITE LOCATION - GUJARAT
APPV'D	V.T.		03-03-2025	
if any queries contact supportautomation@nihva.com				REVISION -
ALL DIMENSION ARE IN mm			A3	SCALE - SHEET 2 OF 2