


PLAIN SHEET 1500 X 3 X 3000L = 1 NO

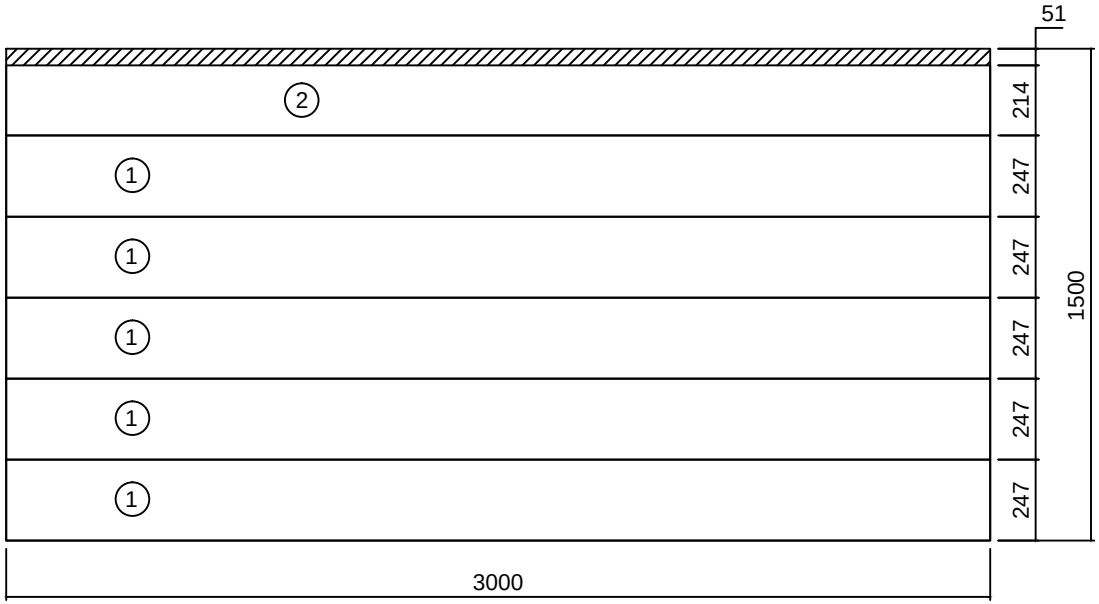

1. SHEET 247 X 3 X 3000L = 5 NOS

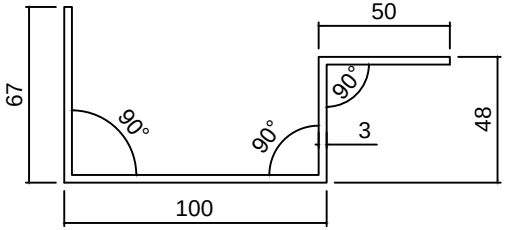

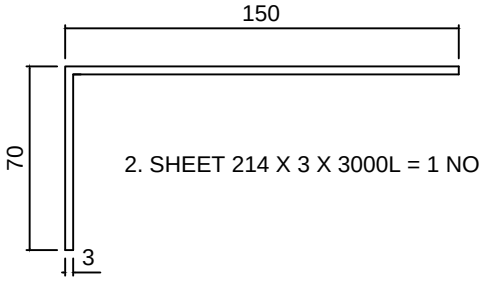

2. SHEET 214 X 3 X 3000L = 1 NO

This drawing & design is the property of NIHVA TECHNOLOGIES. Not to be sold or copied to any other concern.

TITLE	GUIDE			NIHVA TECHNOLOGIES PVT. LTD.
	NAME	SIGN	DATE	
DRAWN	P.V.A		26.08.2019	CLIENT -
CHECK	V.M.T		26.08.2019	PROJECT -
APPRD.				SITE LOCATION -

NIHVA TECHNOLOGIES PVT. LTD. PUNE
Tel : 020 66304033
Email:- info@nihva.com
Website:- www.nihva.com

If any queries contact : design@nihva.com	DWG. NO. : NIHVA/19-20/VDR/150		REV- 00
ALL DIMENSION ARE IN mm	SCALE: NTS	WT:	SHEET: 01 OF 01