




SIDE VIEW

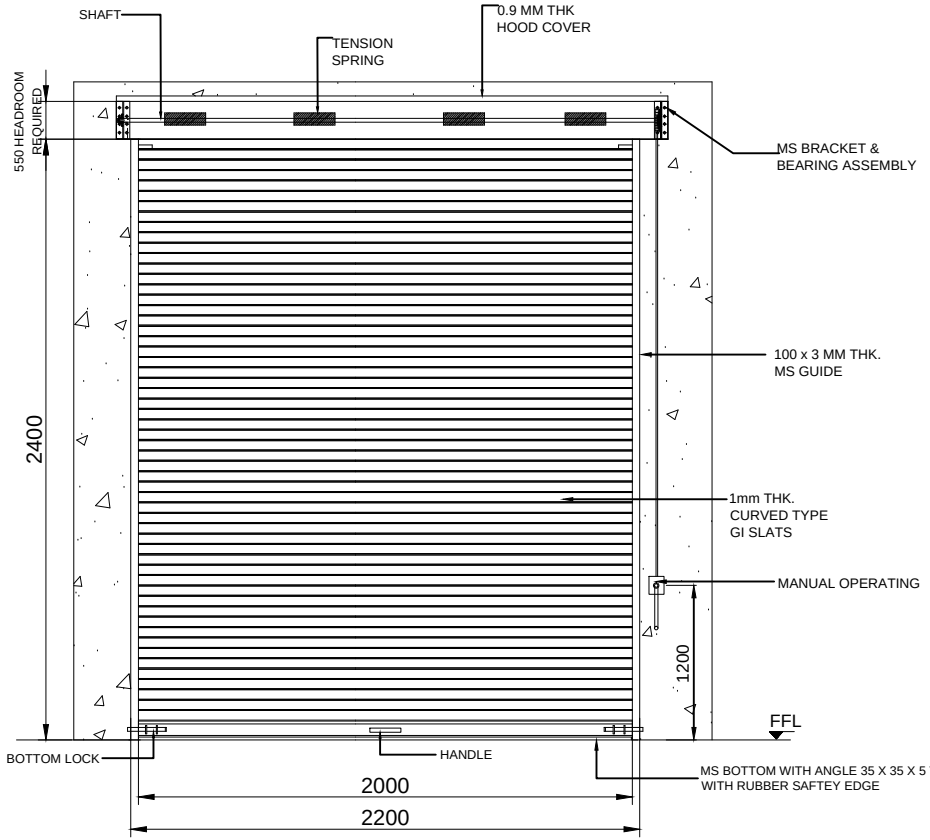


INSIDE ELEVATION

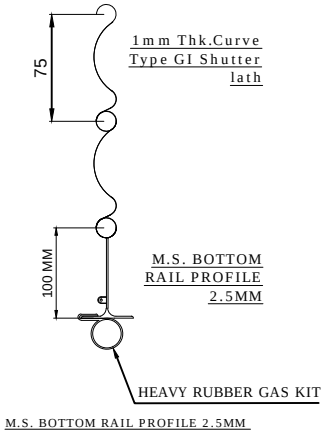

M.S. BOTTOM RAIL PROFILE 2.5MM

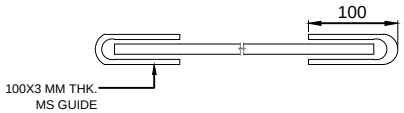

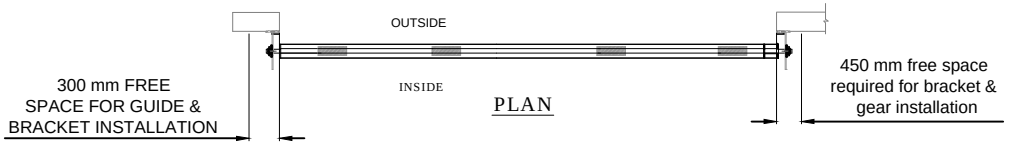

PLAN

NOTE :
1. SHUTTER IS WALL MOUNTED.
2. NO. OF SLATS = 42 NOS.
3. POWDER COAT = RAL 5015 (SKY BLUE)

TOLERANCE - ±10mm

S.N.	LOCATION	SIZE	QUANTITY
1	-	2000(W)X2400(H)	01

NOTE-
1.ALL CIVIL WORK WILL BE CLIENT'S SCOPE.
2.DESIGN OF SHUTTER IS AS PER I.S. 6248:1979 STANDARDS.

This drawing & design is the property of NIHVA TECHNOLOGIES. Not to be sold or copied to any other concern.

TITLE	GEAR OPERATED ROLLING SHUTTER 2mX2.4m With Right side gearbox			NIHVA TECHNOLOGIES PVT. LTD. PUNE Tel : 020 66304033 Email:- info@nihva.com
	NAME	SIGN	DATE	NIHVA TECHNOLOGIES PVT. LTD. Website:- www.nihva.com
DRAWN	P.A		24.12.2018	CLIENT -
CHECK	P.A		24.12.2018	PROJECT -
APPRD.	R.D		24.12.2018	SITE LOCATION - CHAKAN
If any queries contact : design@nihva.com				DWG. NO. : NIHVA/18-19/VDR/294 REV- 0
ALL DIMENSION ARE IN mm				SCALE: NTS WT: SHEET: 01 OF 01