
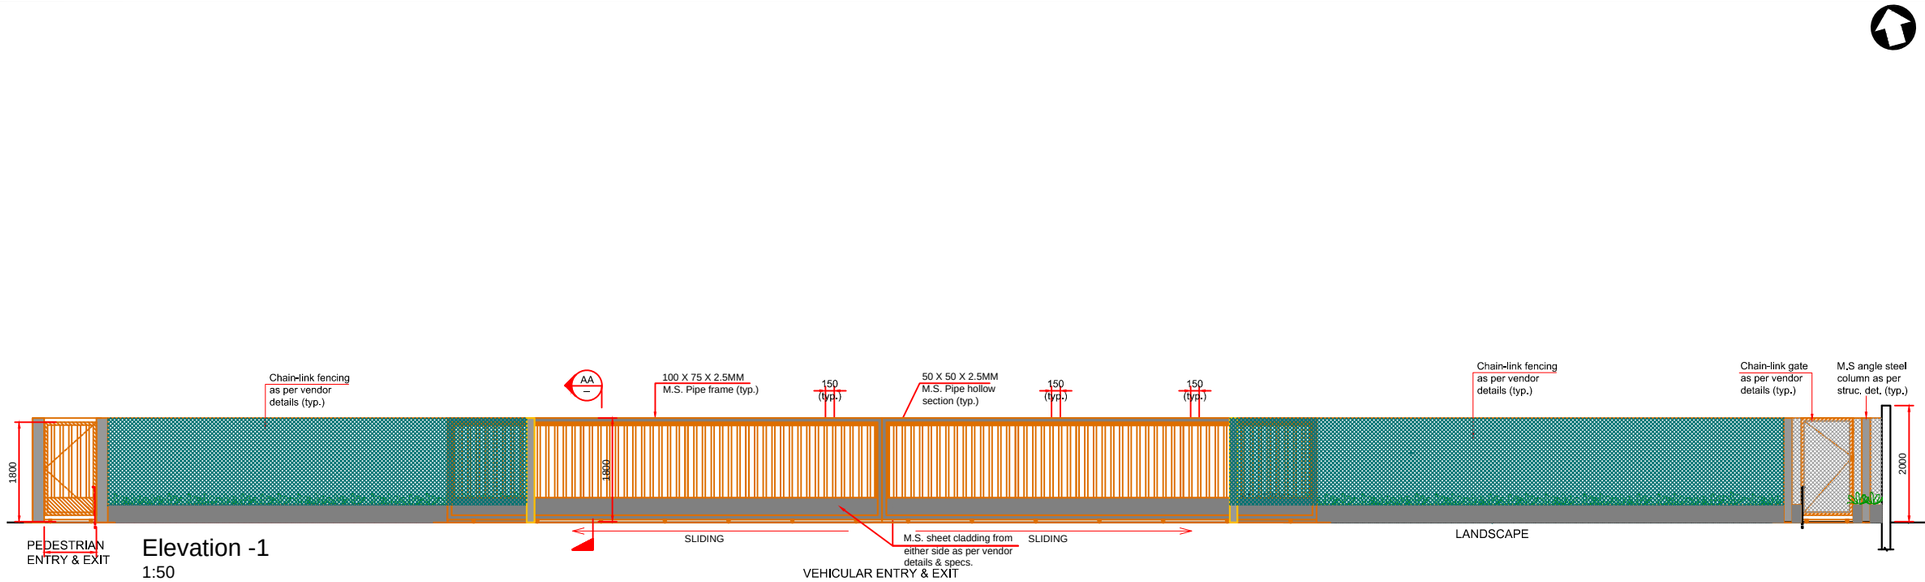


Elevation -1
1:50

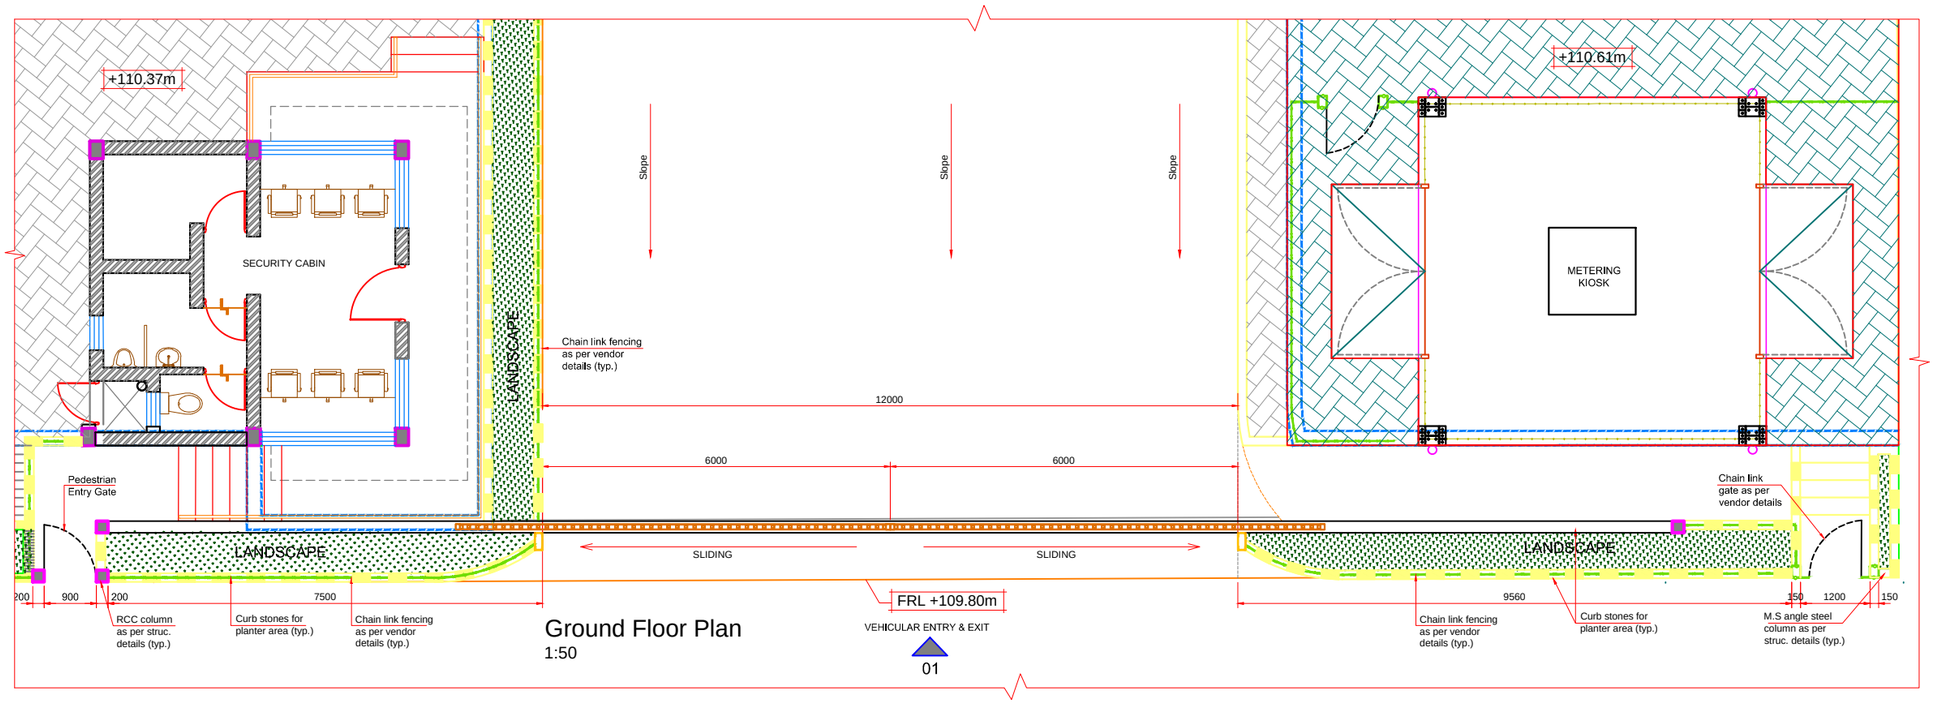

Ground Floor Plan
1:50

01


© Mott MacDonald Pvt Ltd

This document is issued for the party which commissioned it and for specific purposes connected with the captioned project only. It should not be relied upon by any other party or used for any other purpose.
We accept no responsibility for the consequences of this document being relied upon by any other party, or being used for any other purpose, or containing any error or omission which is due to an error or omission in data supplied to us by other parties.

Notes

1. All dimensions and levels are in metres.
2. All levels are unfinished level. unless otherwise mention.
3. Drawings shall not be scaled for dimensions, only written dimensions shall be followed.

Key Plan

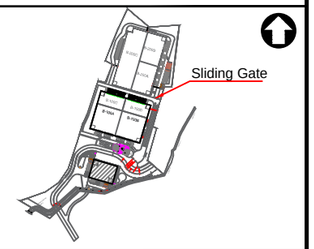

Reference drawings

MMD-340587-A-DR-MSP-XX-0001 Master Plan

Legend

F.F.L.	= Finished Floor Level	M.S.	= Mild Steel
F.G.L.	= Finished Ground Level	Specs.	= Specification
S.S.L.	= Structural slab Level		Brick wall
THK.	= Thick		Landscape Area
Typ.	= Typical		300mm high Curb Stones
Det.	= Detail		
T.O.C.	= Top of Concrete		

Rev	Date	Drawn	Description	Ch'k'd	App'd
B	04/12/2017	RK	Issued for Construction	AC	SS
A	17/10/2017	RK	Issued for Construction	AC	SS

MOTT MACDONALD

Mott MacDonald House
44/45, Street No - 14
MIDC Area, Andheri - East
Mumbai, 400093
India
T +91 (0)22 3083 5000
F
W www.mottmac.com

Client

INDOSPACE INDUSTRIAL & LOGISTICS PARKS

Rohan Realtors (Pune) Pvt. Ltd.
Chakan P4 450/2U , 450/2/K ,
450/2E , 450/2/A , 450/2/K ,
450/2/E , 450/2/U ,
Mahalunge , Khed, Pune.

Title

Rohan Cityscapes Pvt. Ltd.
Chakan IV
Sliding Gate Detail

Designed	A Chaubal		Eng check	A Chaubal	
Drawn	R Kudav		Coordination	A Chaubal	
Dwg check	A Chaubal		Approved	S Sawant	

Scale at A1	Status	Rev	Security
As Shown	CON	B	STD

Drawing Number
MMD-340587-A-DR-B2-XX-2302