SLINDING DIRECTION

2400.00
OVERLAPING DISTANCE


OUTSIDE FTO
(MADC LAND)

D1

LAND SIDE (OUTSIDE)

C1B1


A1

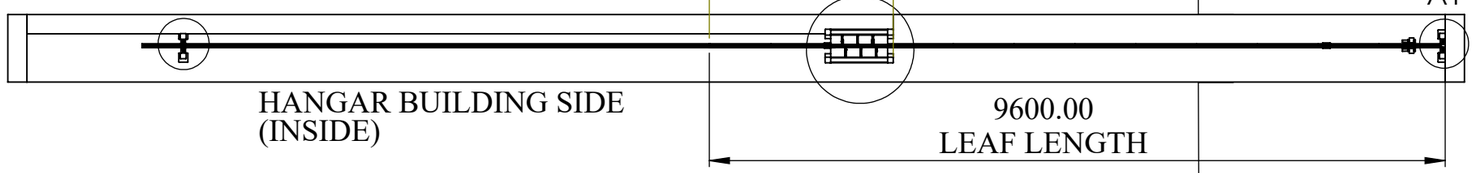

HANGAR BUILDING SIDE
(INSIDE)


9600.00
LEAF LENGTH

INSIDE FTO PLOT

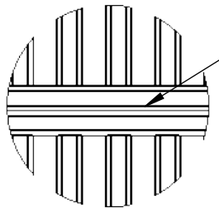

HORIZONTAL TUBE
MS TUBE 40*40*4MM THK

DETAIL E
SCALE 1 : 10

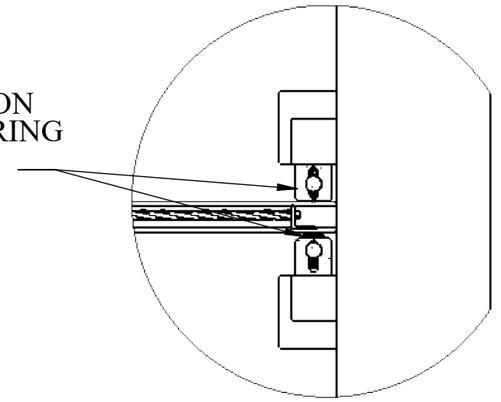

NYLON
BEARING

POST 1 AND NYLON
BEARING ASM

DETAIL A1
SCALE 1 : 10

600.00
L ANLE HEIGHT


L ANGLE 40*40*5MM THK

9600.00
LEAF LENGTH

SQ MS TUBE
40*40*4MM THK

SLIDING DIRECTION

CONFIRMED BY END
CLIENT

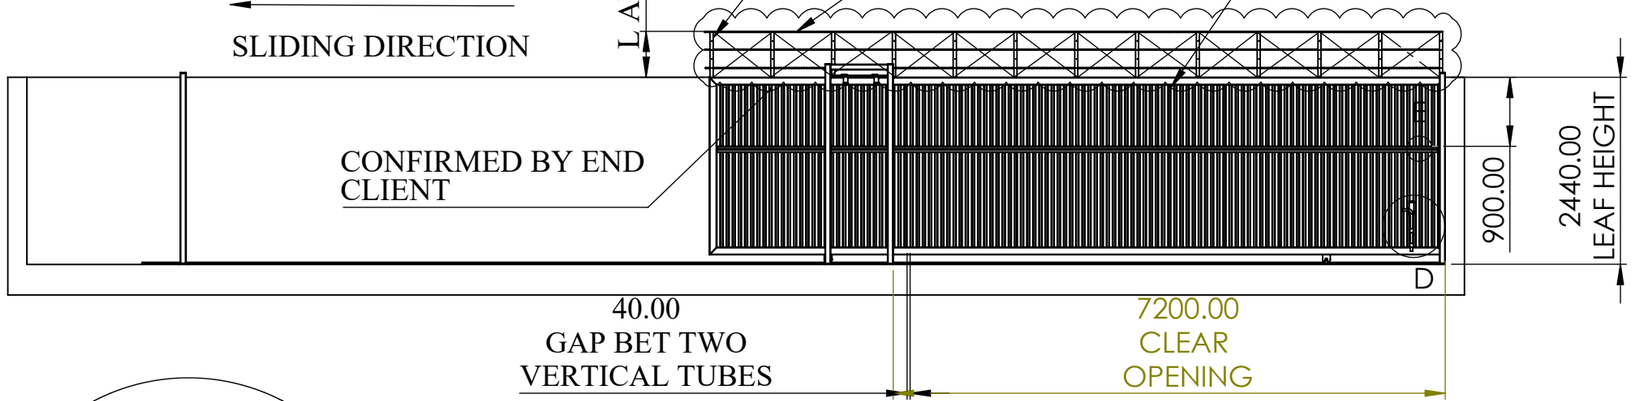


900.00

2440.00
LEAF HEIGHT

40.00
GAP BET TWO
VERTICAL TUBES


7200.00
CLEAR
OPENING

RECT MS TUBE
100*50*5MM THK

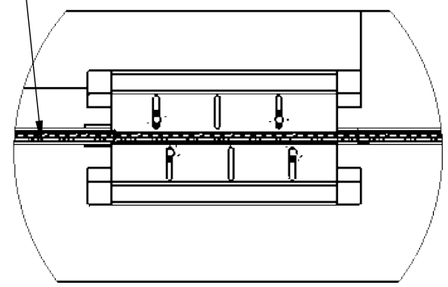

POST 2 AND NYLON
BEARING ASM


DETAIL C1B1
SCALE 1 : 20

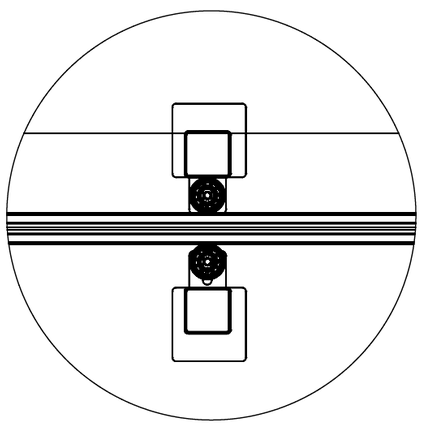

POST NO 3 &
NYLON ROLLER BERAING
ASM

DETAIL D1
SCALE 1 : 10

TOWER BOLT
ROD

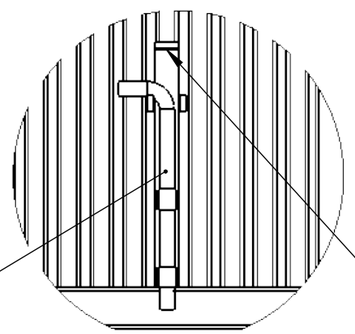

TOWER BOLT
ROD SUPPORT FRAME

TOWER BOLT LOCKING
ARRANGEMENT.

DETAIL D
SCALE 1 : 15

NOTE :

1)GA DRAWING TYPE NO 01
2)Total column -04 (A1,B1,C1,D1)
3) 03 column posts when the gates is in the closed position.(A1,B1,C1)
4) 03 column posts when the gates is in the fully open position.(B1,C1,D1)
5) barbed wire design is zigzag pattern.

TITLE - GATE AUTOMATIOM				NIHVA TECHNOLOGIES PVT.LTD.PUNE
DWG NO - NTPL-000-PM-001-00-00-00				Website - www.nihva.com
	NAME	SIGNATURE	DATE	PROJECT NO - NTPL-000-PM
DRAWN	V.W		21-05-2025	PRODUCT - SINGLE SLIDING GATE
CHK'D	S.W.		21-05-2025	SITE LOCATION -
APPV'D	V.T.		21-05-2025	
if any queries contact - supportautomation@nihva.com				REVISION - 01 / QTY - 1
ALL DIMENSION ARE IN mm		A3		SCALE / SHEET 1 OF 1