


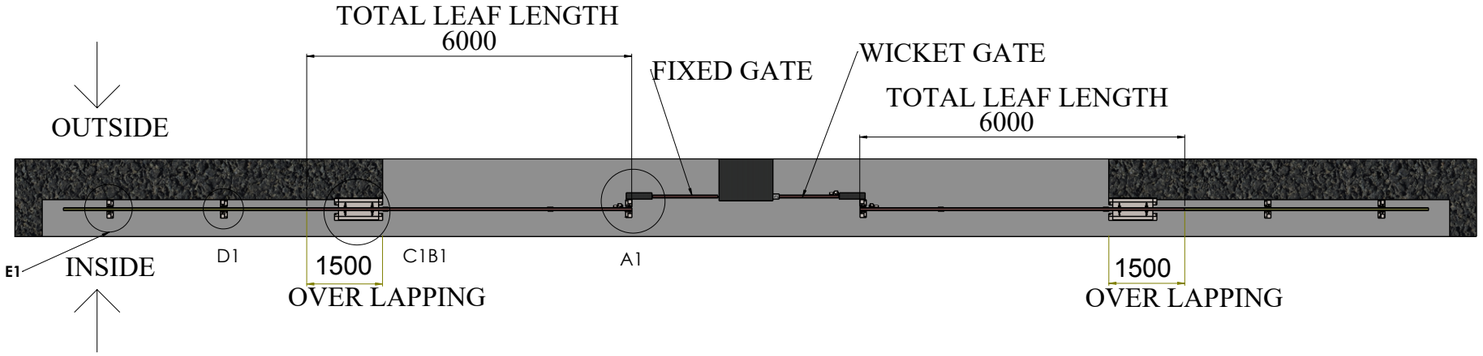


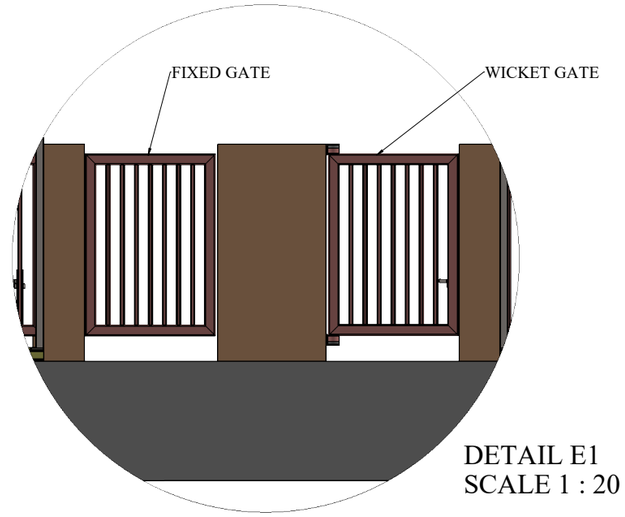


DETAIL E1
SCALE 1 : 20

FIXED GATE AND SWING
GATE VIEW

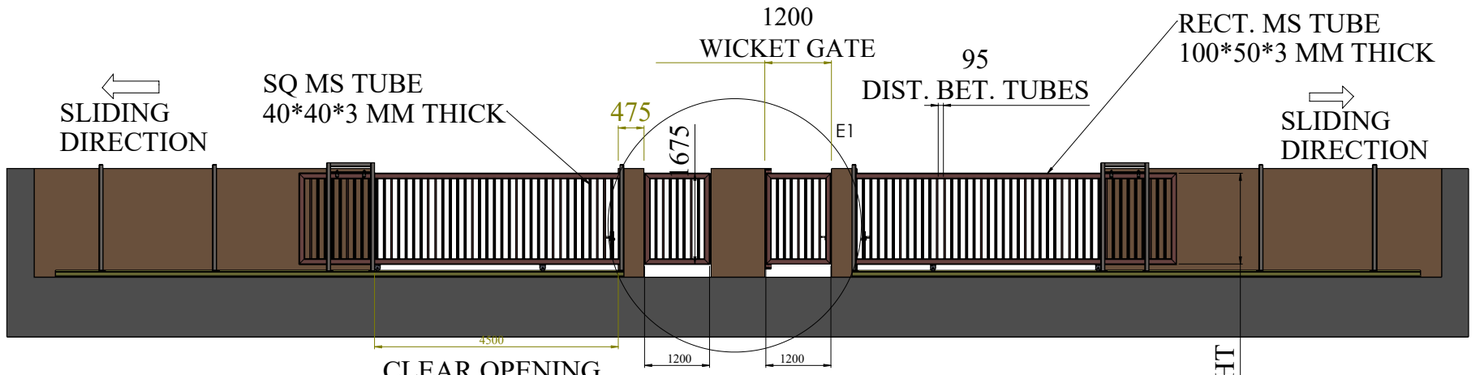


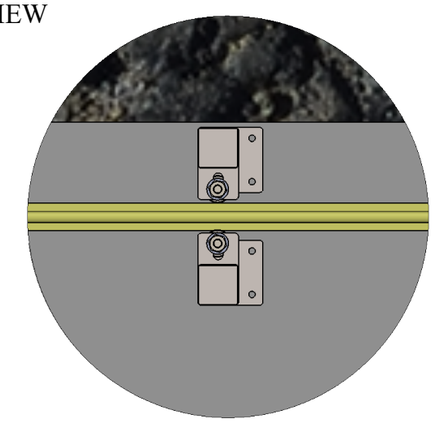

DETAIL D1
SCALE 1 : 4

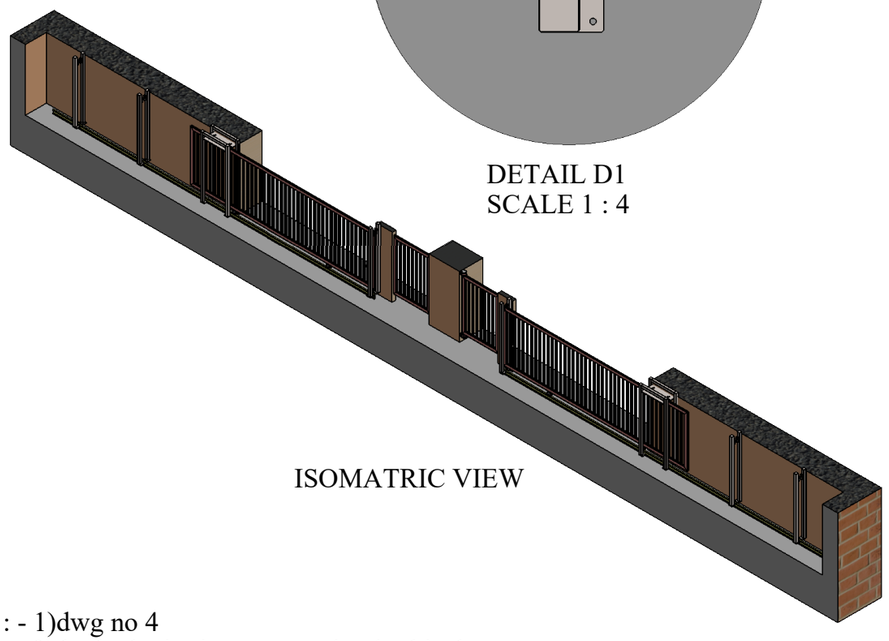


ISOMATRIC VIEW

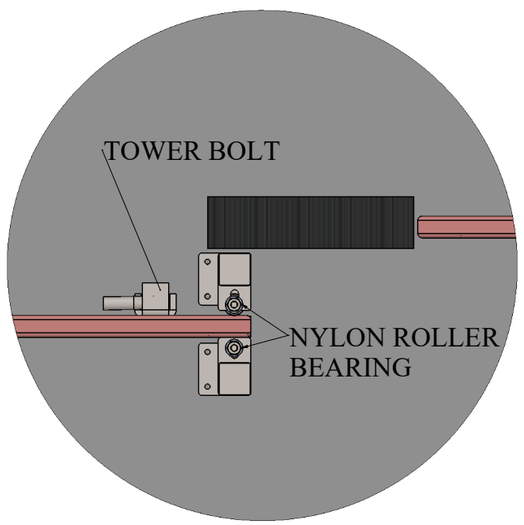

POST 1 AND NYLON ROLLER
BEARING ASSEM.

DETAIL A1
SCALE 1 : 5

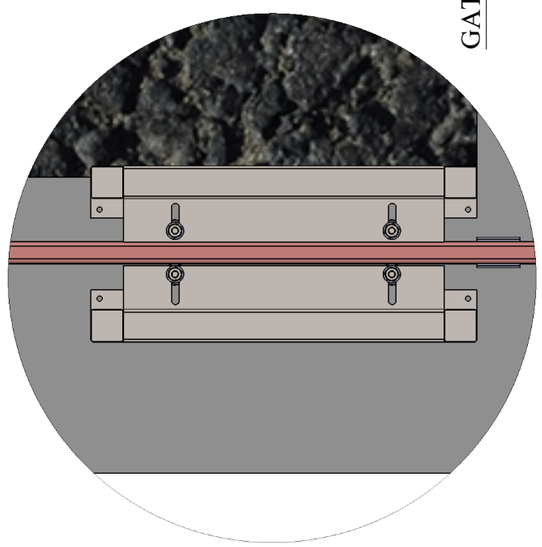

POST 2 AND NYLON ROLLER
BEARING ASSEM.

DETAIL C1B1
SCALE 1 : 5


Note : - 1)dwg no 4
2) barbed wire is not menstion in this dwg.
3)Total column -10(A1,B1,C1,D1,E1 SAME AS RIGHT SIDE ADD 5 POST)
4) 03 column posts when the gates is in the closed position.(A1,B1,C1)
5) 04 column posts when the gates is in the fully open position.(B1,C1,D1,E1)

TITLE - GATE AUTOMATION				NIHVA TECHNOLOGIES PVT.LTD.PUNE Website - www.nihva.com	
DWG NO - NTPL-290-PM-004				PRODUCT - SLIDING_GATE	
	NAME	SIGNATURE	DATE	PROJECT NO - NTPL-290-PM	REVISION - 00
DRAWN	V.W.		29-07-2025	SITE LOCATION - AMRAVATI	WEIGHT -
CHKD	B.S.		29-07-2025	MATRIAL -	QTY - 1
APP'D	V.T.		29-07-2025		
If any queries contact - design@nihva.com				PROJECTION METHOD:	SCALE :
ALL DIMENSION ARE IN mm			A3		SHEET 1 OF 1




ITEM NO.	PART NUMBER	DESCRIPTION	QTY.
1	CIVIL BASE	27000 (L) X3100 (H)	1
2	EN8 & ISMB BEAM	20 MM (DIA) 10610 MM (L)	2
3	FIXED GATE LEAF	1200 (W) X1675 (H)	1
4	WICKET GATE LEAF	1200 (W) X 1675 (H)	1
5	BOTTOM PLATE FOR HINGES	80X75X6 THK	2
6	DOUBLE POST ASM	320(L) X350 (W) X1827(H)	2
7	SLIDING GATE LEAF	6000 (W) X 1675 (H)	2
8	SINGLE POST ASM	320(L) X75 (W) X1827(H)	6
9	NYLON ROLLER AND BEARING ASM	75 (H) X 50 (DIA)	20
10	HEX NUT	M14	20
11	M14 ANCHOR ASSY	M14 X150	82
12	NYLON STOPPER	215X110 X110	2
13	TOWER BOLT	300 (L) 15 MM(DIA) & 18 MM DIA & 3 MM THK (HOLLOW PIPE)	3
14	HINGS	3 INCH HINGS	2

DETAIL A
SCALE 1 : 15

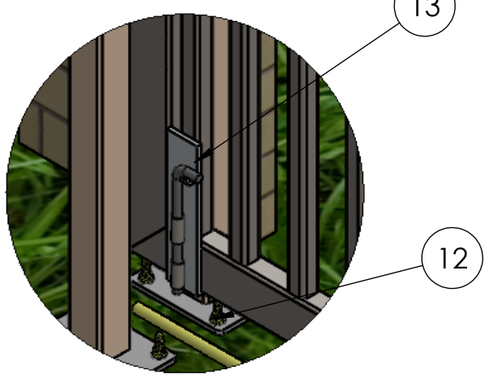

DETAIL C
SCALE 1 : 10

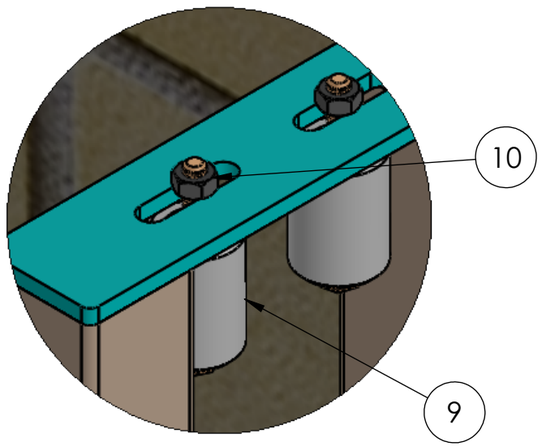



DETAIL B
SCALE 1 : 3

NOTE-
OVERLAPPING IS 1500 MM
GAP BETWEEN TWO TUBE-95 MM

TITLE - GATE AUTOMATION				NIHVA TECHNOLOGIES PVT.LTD.PUNE
DWG NO - NTPL-290-PM-004				Website - www.nihva.com
	NAME	SIGNATURE	DATE	PROJECT NO - NTPL-290-PM
DRAWN	V.B.		16-08-2025	PRODUCT - SLIDING GATE
CHK'D	B.S.		16-08-2025	SITE LOCATION - AMRAVATI
APPV'D	V.T.		16-08-2025	TYPE 4
if any queries contact - design@nihva.com				REVISION -00 / QTY - 1
ALL DIMENSION ARE IN mm		A3		SCALE - / SHEET 1 OF 1

ITEM NO.	PART NUMBER	DESCRIPTION	QTY.
1	SLIDING GATE LEAF	6000 (L) X 1675 (H)	2
2	WHEEL AND PLATE ASM	4 INCH WHEEL	4

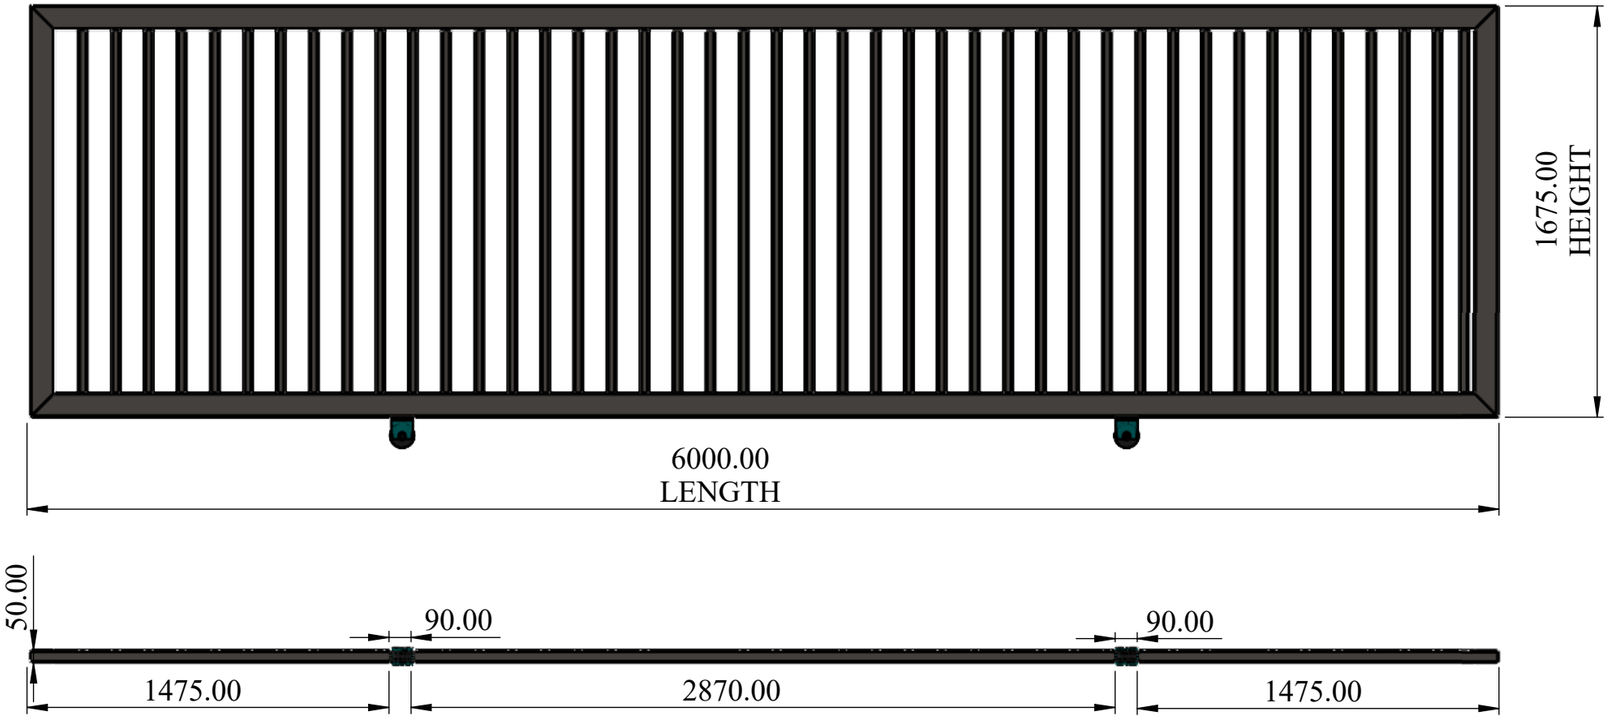


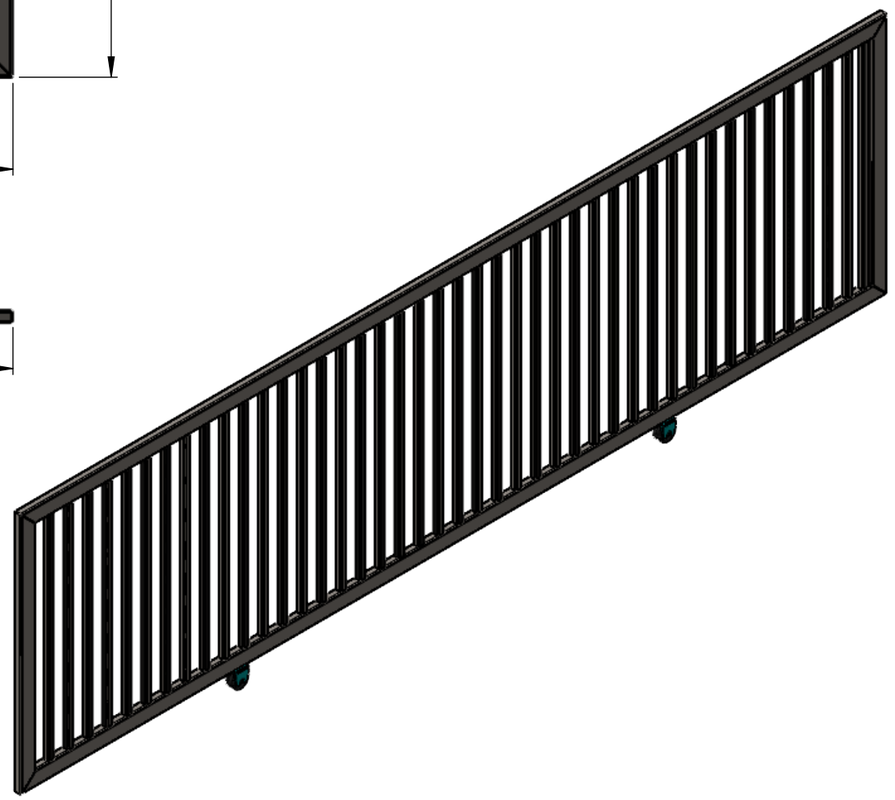



SLIDING LEAF- 2 NOS

TITLE - GATE AUTOMATION				NIHVA TECHNOLOGIES PVT.LTD.PUNE Website - www.nihva.com
DWG NO - NTPL-290-PM-004-01				
	NAME	SIGNATURE	DATE	PROJECT NO - NTPL-290-PM
DRAWN	V.B.		16-08-2025	PRODUCT - SLIDING GATE
CHK'D	B.S.		16-08-2025	SITE LOCATION - AMRAVATI
APPV'D	V.T.		16-08-2025	TYPE 4
if any queries contact - design@nihva.com				REVISION -00 / QTY - 1
ALL DIMENSION ARE IN mm		A3		SCALE - / SHEET 1 OF 18

ITEM NO.	PART NAME	DESCRIPTION	QTY.
	OUTER FRAME	100X 50 X3 THK	8
	INNER SQ TUBE	40 X 40 X 3 THK	84

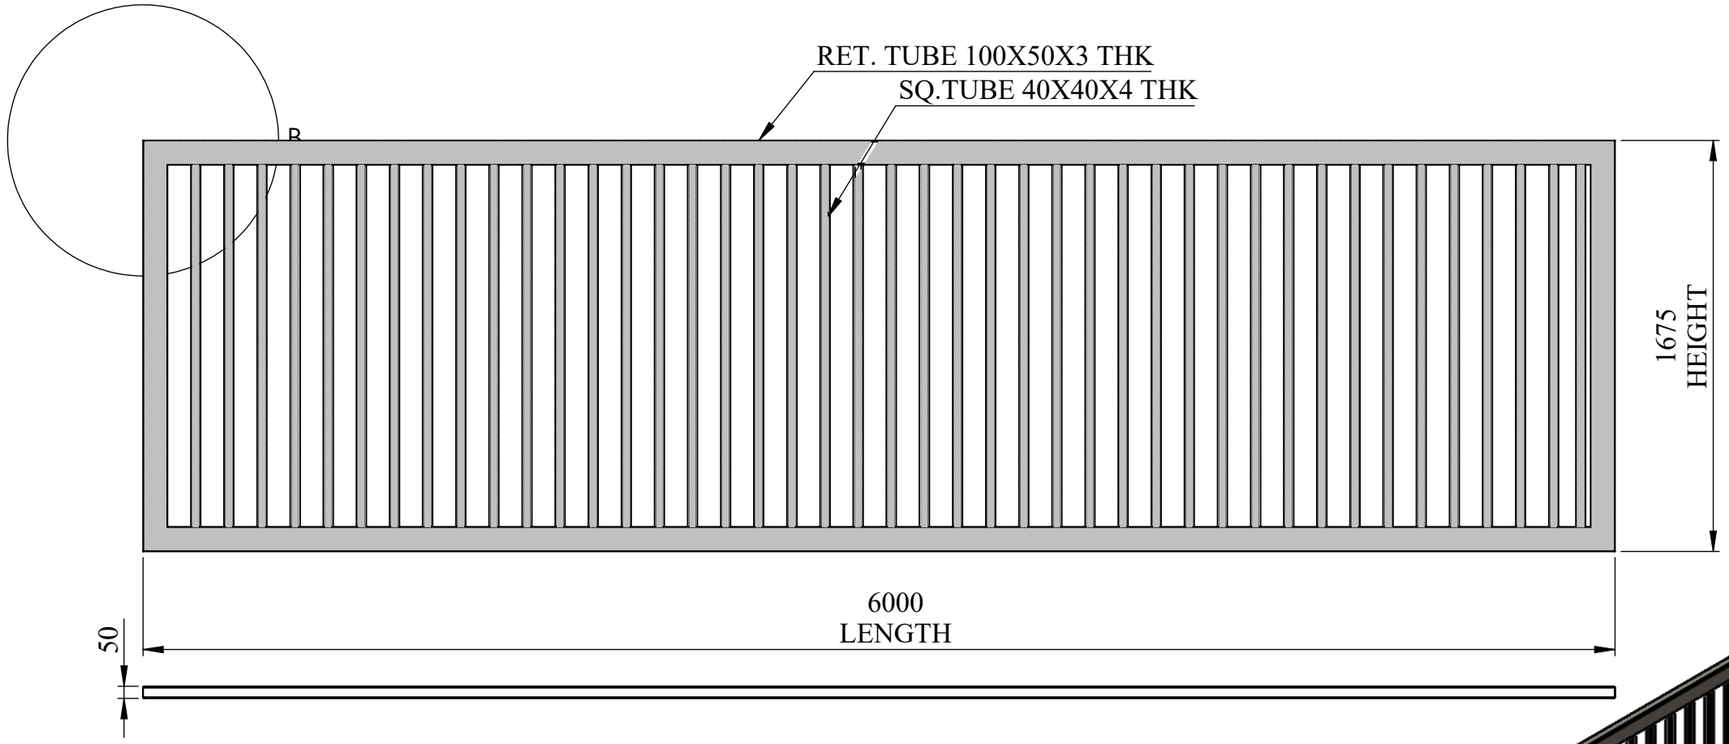

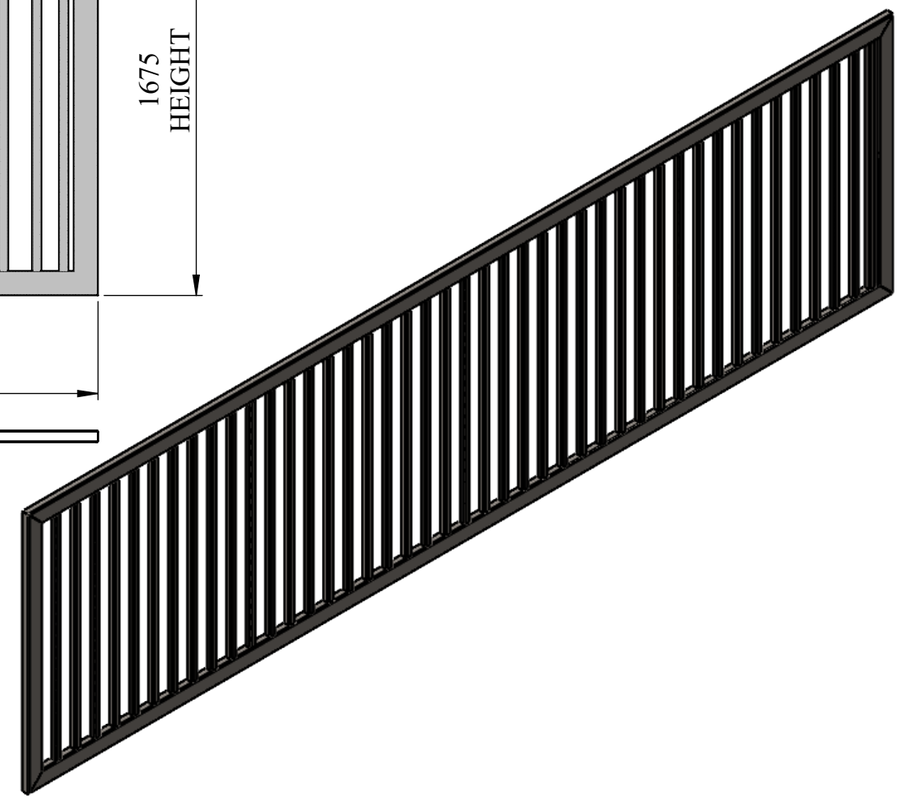

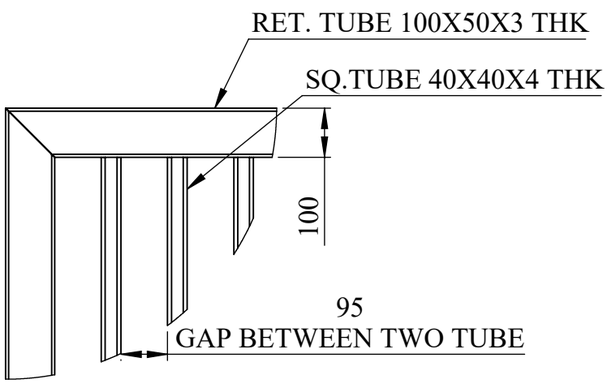



DETAIL B
SCALE 2 : 25

SUPPORT TUBE
QTY-84 NOS FOR TWO LEAF

TITLE - GATE AUTOMATION				NIHVA TECHNOLOGIES PVT.LTD.PUNE
DWG NO - NTPL-290-PM-001-01-01				Website - www.nihva.com
	NAME	SIGNATURE	DATE	PROJECT NO - NTPL-290-PM
DRAWN	V.B.		16-08-2025	PRODUCT - SLIDING GATE
CHK'D	B.S.		16-08-2025	SITE LOCATION - AMRAVATI
APPV'D	V.T.		16-08-2025	TYPE 4
if any queries contact - supportautomation@nihva.com				REVISION -00 / QTY - 1
ALL DIMENSION ARE IN mm		A3		SCALE - / SHEET 2 OF 18

ITEM NO.	PART NUMBER	DESCRIPTION	QTY.
1	BOTTOM PLATE	215X150X10	12
2	SINGLE POST PLATE	320X75X10	6
3	VERTICAL TUBE	75X75X3	12

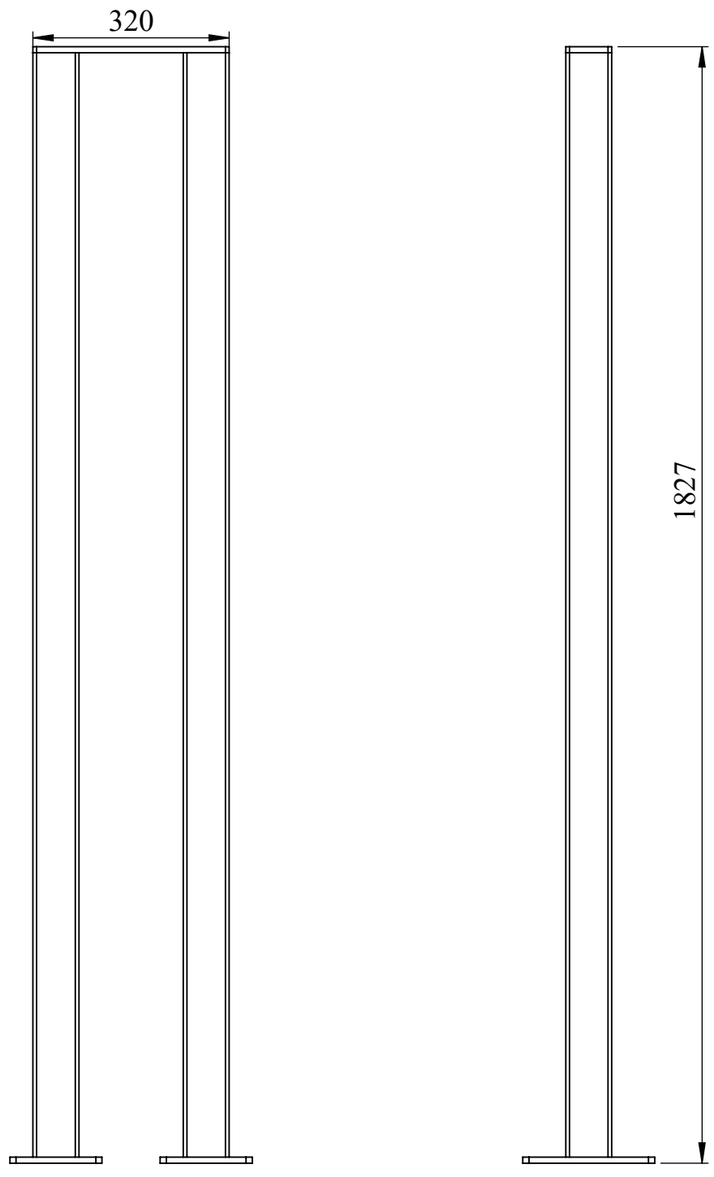


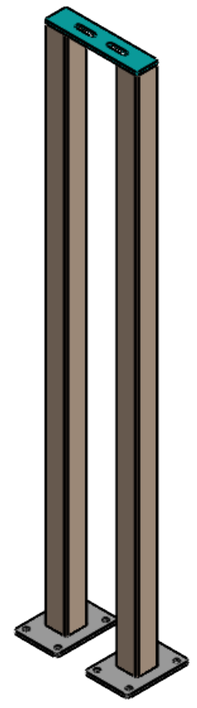


SINGLE POST ASM
QTY- 6 NOS

TITLE -GATE AUTOMATION				NIHVA TECHNOLOGIES PVT.LTD.PUNE Website - www.nihva.com
DWG NO - NTPL-290-PM-004-02				
	NAME	SIGNATURE	DATE	PROJECT NO - NTPL-290-PM
DRAWN	V.B.		16-08-2025	PRODUCT -SLIDING GATE
CHK'D	B.S.		16-08-2025	SITE LOCATION - AMRAVATI
APPV'D	V.T.		16-08-2025	TYPE 4
if any queries contact - design@nihva.com				REVISION -00 / QTY - 1
ALL DIMENSION ARE IN mm		A3		SCALE - / SHEET 3 OF 18

ITEM NO.	PART NUMBER	DESCRIPTION	QTY.
1	SINGLE POST PLATE	320X75X10	6

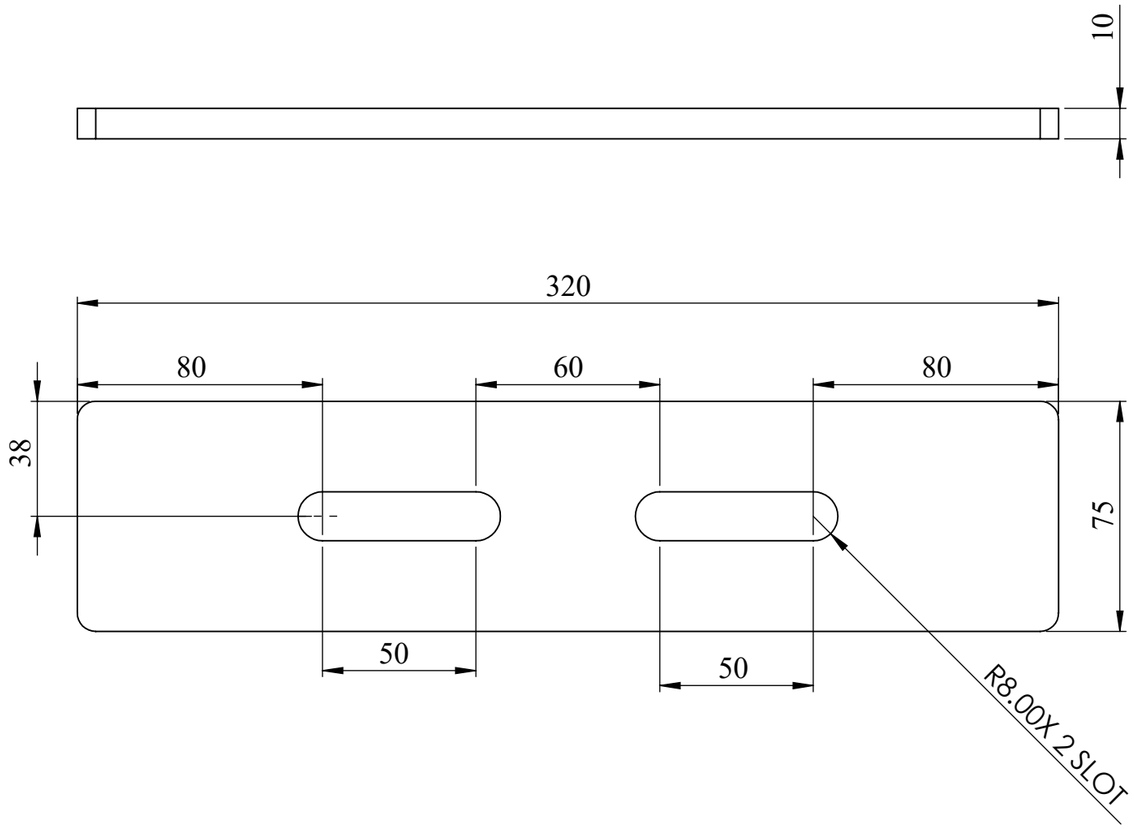


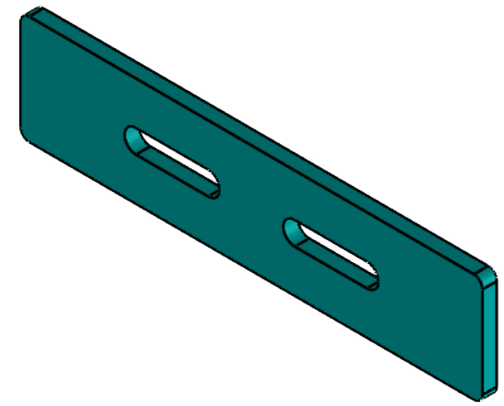


SINGLE POST PLATE
320X75X10 MM THK
QTY-6 NOS

TITLE -GATE AUTOMATION				NIHVA TECHNOLOGIES PVT.LTD.PUNE Website - www.nihva.com
DWG NO - NTPL-290-PM-004-02-01				
	NAME	SIGNATURE	DATE	PROJECT NO - NTPL-290-PM
DRAWN	V.B.		16-08-2025	PRODUCT - SLIDING GATE
CHK'D	B.S.		16-08-2025	SITE LOCATION - AMRAVATI
APPV'D	V.T.		16-08-2025	TYPE 4
if any queries contact - design@nihva.com				REVISION -00 / QTY - 1
ALL DIMENSION ARE IN mm		A3		SCALE - / SHEET 4 OF 18

ITEM NO.	PART NUMBER	DESCRIPTION	QTY.
1	VERTICAL SUPPORT TUBE	75X75X3	20

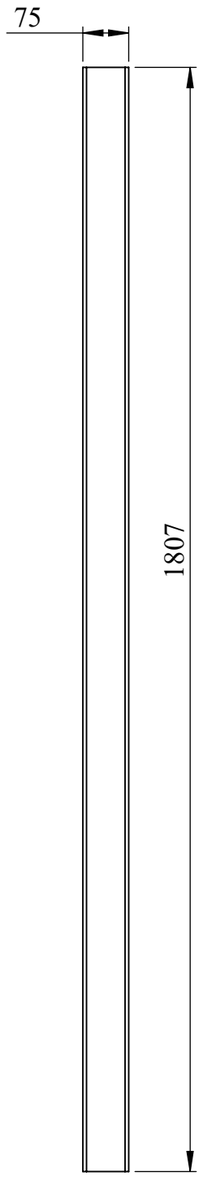


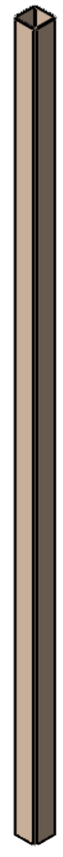



VERTICAL SUPPORT TUBE
75X75X3 MM THK
QTY-20 NOS
THIS VERTICAL SUPPORT TUBE SAME AS USE DOUBLE POST

TITLE -GATE AUTOMATION				NIHVA TECHNOLOGIES PVT.LTD.PUNE
DWG NO - NTPL-290-PM-004-02-02				Website - www.nihva.com
	NAME	SIGNATURE	DATE	PROJECT NO - NTPL-290-PM
DRAWN	V.B.		14-08-2025	PRODUCT - SLIDING GATE
CHK'D	B.S.		14-08-2025	SITE LOCATION - AMRAVATI
APPV'D	V.T.		14-08-2025	TYPE 4
if any queries contact - design@nihva.com				REVISION -00 / QTY - 1
ALL DIMENSION ARE IN mm		A3		SCALE - / SHEET 5 OF 18

ITEM NO.	PART NUMBER	DESCRIPTION	QTY.
1	BOTTOM PLATE	215X150X10	20

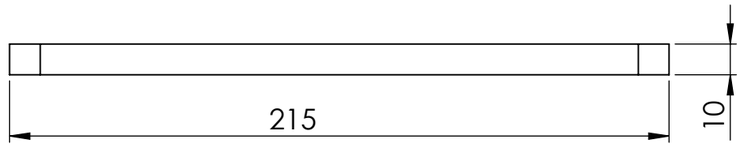

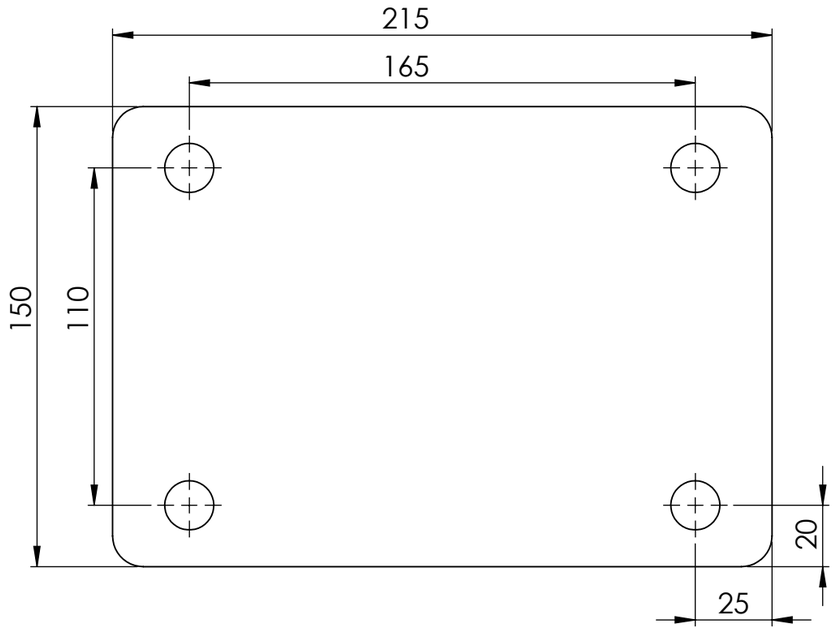


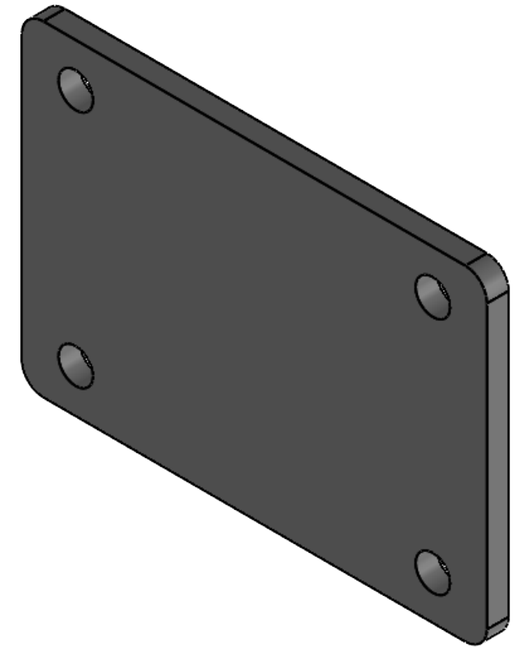


BOTTOM PLATE FOR POST
215X150X10 MM THK
QTY-20 NOS
THIS BOTTOM PLATE SAME AS USE DOUBLE POST

TITLE -GATE AUTOMATION				NIHVA TECHNOLOGIES PVT.LTD.PUNE
DWG NO - NTPL-290-PM-004-02-03				Website - www.nihva.com
	NAME	SIGNATURE	DATE	PROJECT NO - NTPL-290-PM
DRAWN	V.B.		16-08-2025	PRODUCT -SLIDING GATE
CHK'D	B.S.		16-08-2025	SITE LOCATION - AMRAVATI
APPV'D	V.T.		16-08-2025	TYPE 4
if any queries contact - design@nihva.com				REVISION -00 / QTY - 1
ALL DIMENSION ARE IN mm		A3		SCALE - / SHEET 6 OF 18

ITEM NO.	PART NUMBER	DESCRIPTION	QTY.
1	BOTTOM PLATE	215X150X10	8
2	DOUBLE POST PLATE	350X320X10	2
3	VERTICAL TUBE	75X75X3	8

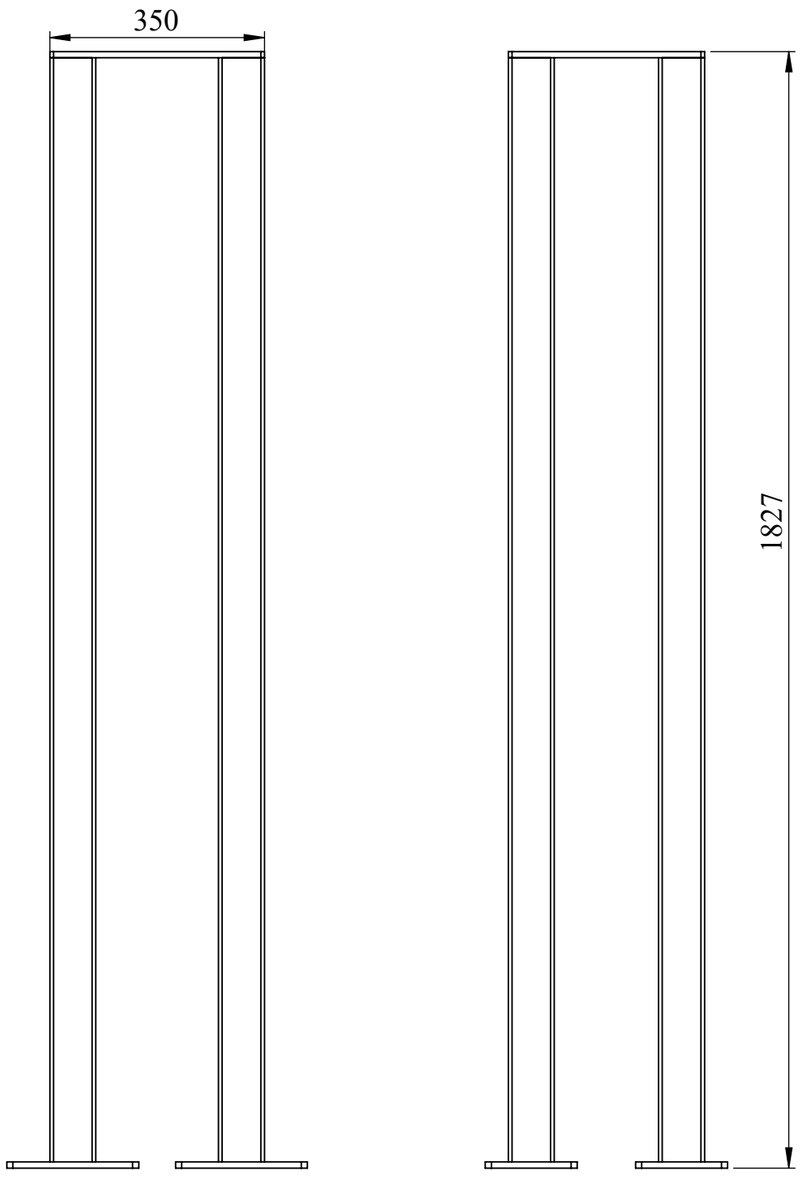

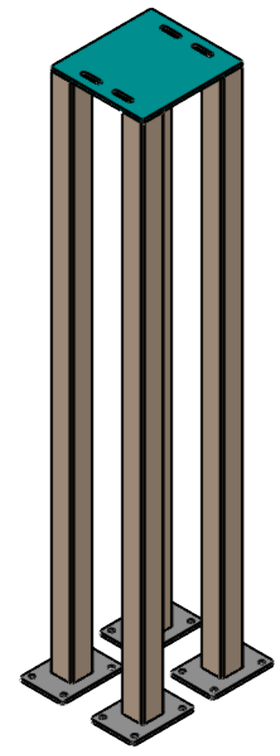



DOUBLE POST ASM
QTY- 2 NOS

TITLE -GATE AUTOMATION				NIHVA TECHNOLOGIES PVT.LTD.PUNE
DWG NO - NTPL-290-PM-004-03				Website - www.nihva.com
	NAME	SIGNATURE	DATE	PROJECT NO - NTPL-290-PM
DRAWN	V.B.		16-08-2025	PRODUCT - SLIDING GATE
CHK'D	B.S.		16-08-2025	SITE LOCATION - AMRAVATI
APPV'D	V.T.		16-08-2025	TYPE 4
if any queries contact - design@nihva.com				REVISION -00 / QTY - 1
ALL DIMENSION ARE IN mm		A3		SCALE - / SHEET 7 OF 18

ITEM NO.	PART NUMBER	DESCRIPTION	QTY.
1	DOUBLE POST PLATE	350X320X10	2



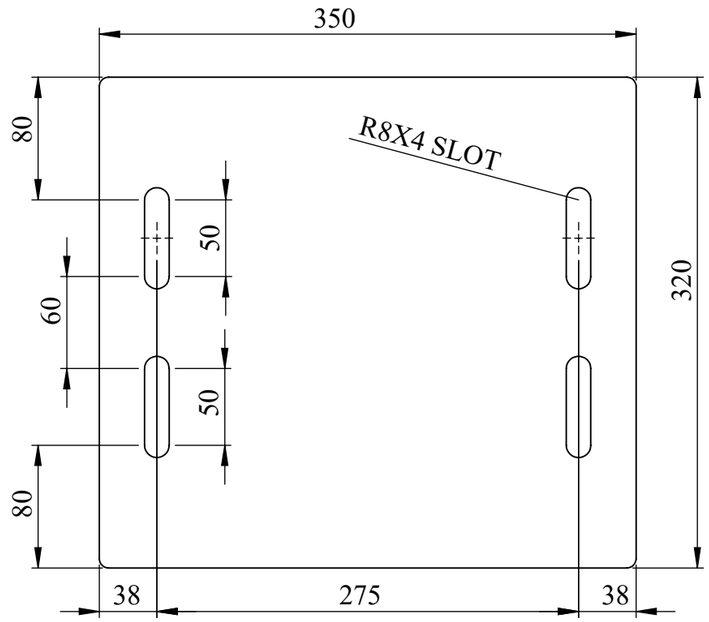


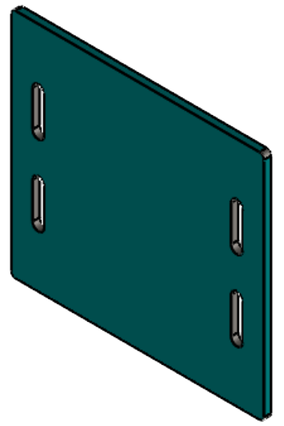



DOUBLE POST PLATE
350X320X10 MM THK
QTY-2 NOS

TITLE -GATE AUTOMATION				NIHVA TECHNOLOGIES PVT.LTD.PUNE
DWG NO - NTPL-290-PM-004-03-01				Website - www.nihva.com
	NAME	SIGNATURE	DATE	PROJECT NO - NTPL-290-PM
DRAWN	V.B.		16-08-2025	PRODUCT -SLIDING GATE
CHK'D	B.S.		16-08-2025	SITE LOCATION - AMRAVATI
APPV'D	V.T.		16-08-2025	TYPE 4
if any queries contact - design@nihva.com				REVISION -00 / QTY - 1
ALL DIMENSION ARE IN mm		A3		SCALE - / SHEET 8 OF 18

ITEM NO.	PART NUMBER	DESCRIPTION	QTY.
1	GUIDE PLATE	ID-14 (H)-79 (W)-10	8
2	SUPPORT PLATE	90x74x10	4
3	WHEEL	100x50	4

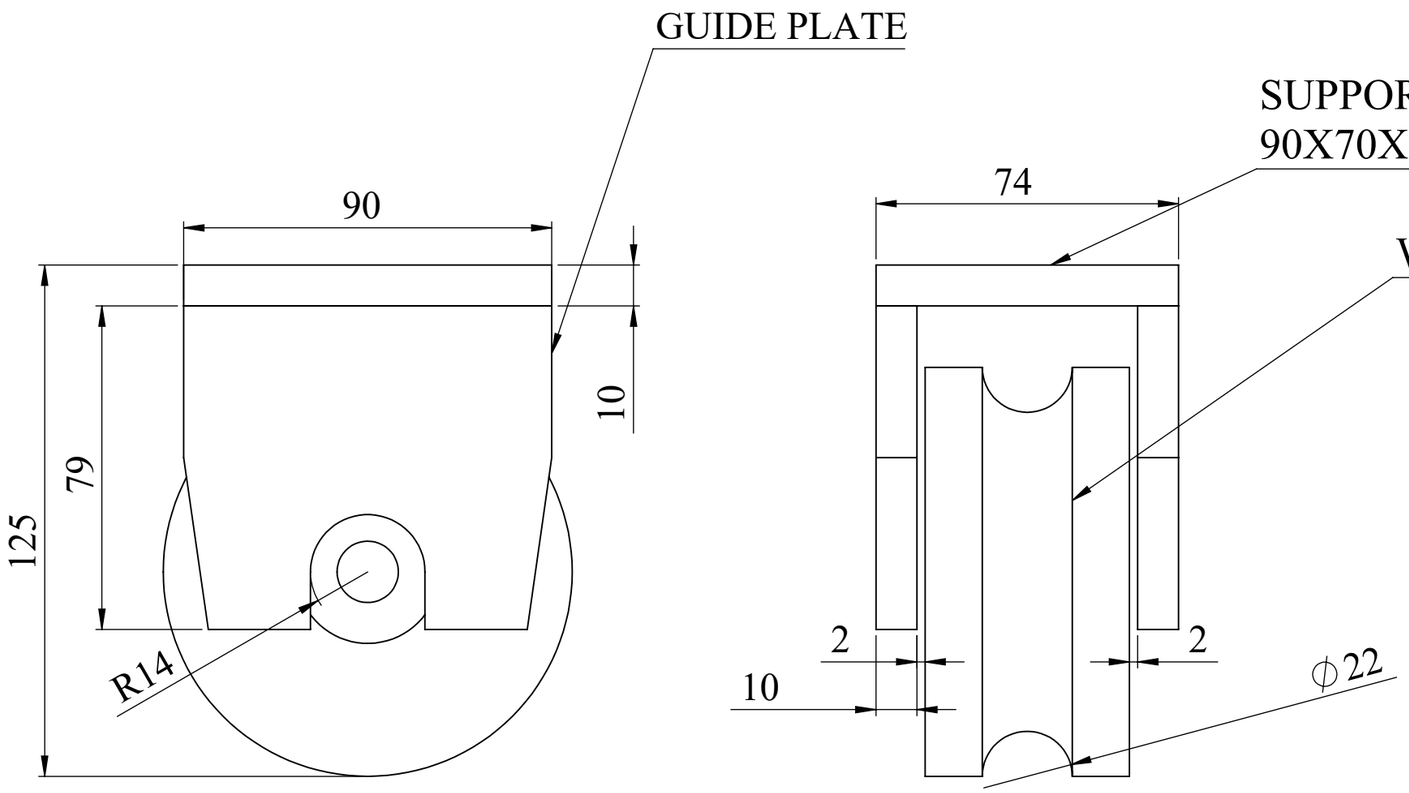

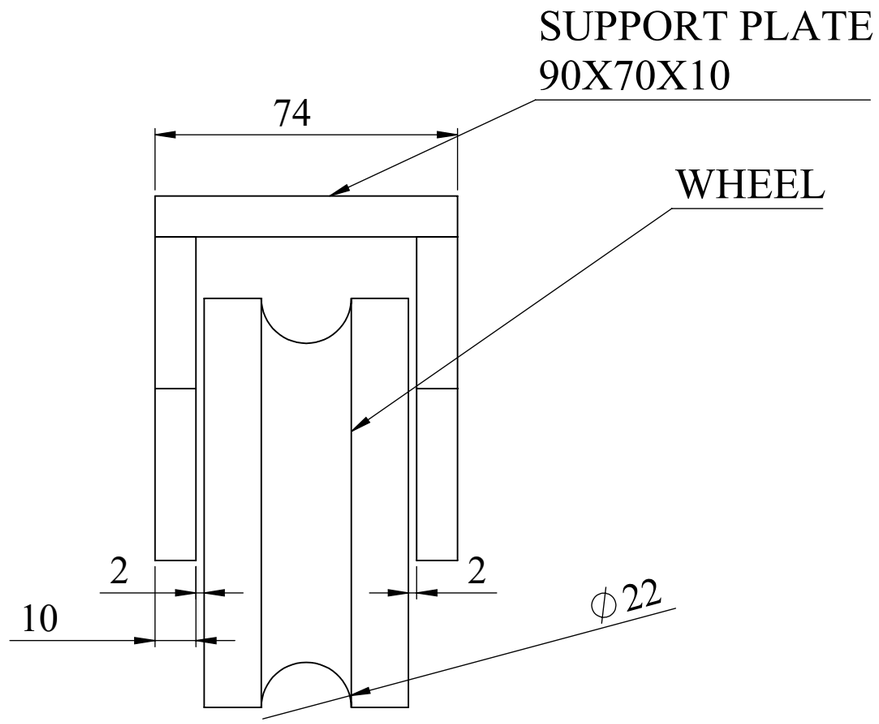


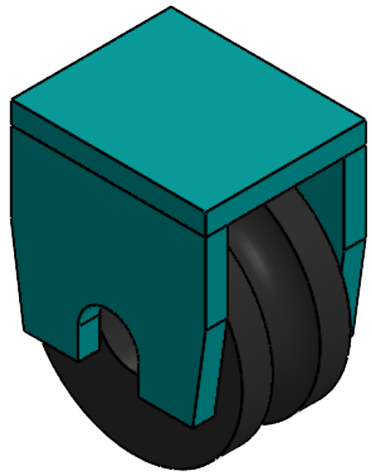


QTY- 4 NOS

TITLE - GATE AUTOMATION				NIHVA TECHNOLOGIES PVT.LTD.PUNE	
DWG NO - NTPL-290-PM-004-01-02				Website - www.nihva.com	
	NAME	SIGNATURE	DATE	PROJECT NO -NTPL-290-PM	
DRAWN	V.B.		16-08-25	PRODUCT -SLIDING GATE	
CHK'D	B.S.		16-08-25	SITE LOCATION - AMRAVATI	
APPV'D	V.T.		16-08-25	TYPE 4	
if any queries contact - design@nihva.com				REVISION -00	QTY - 1
ALL DIMENSION ARE IN mm		A3		SCALE -	SHEET 9 OF 18

ITEM NO.	PART NUMBER	DESCRIPTION	QTY.
1	SUPPORT PLATE	90x74x10	4

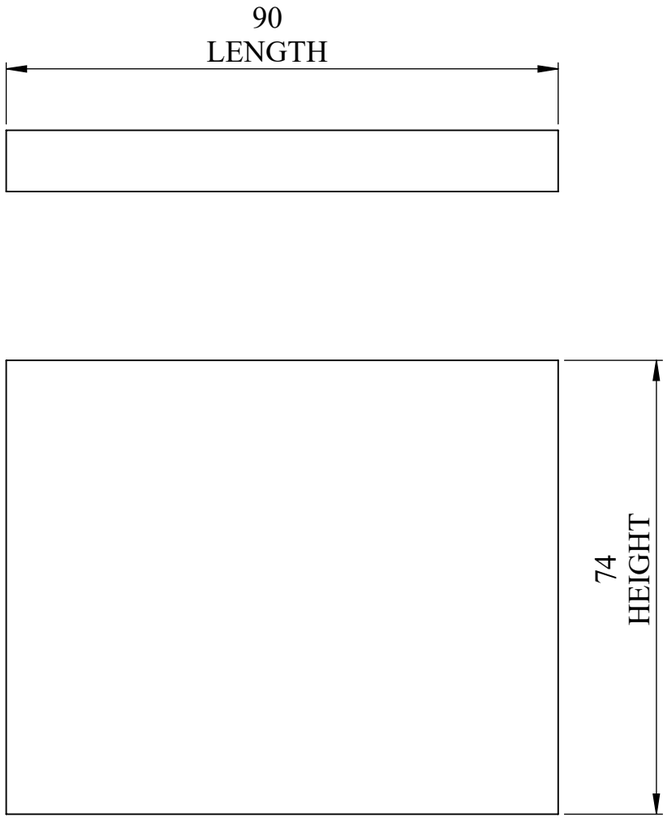


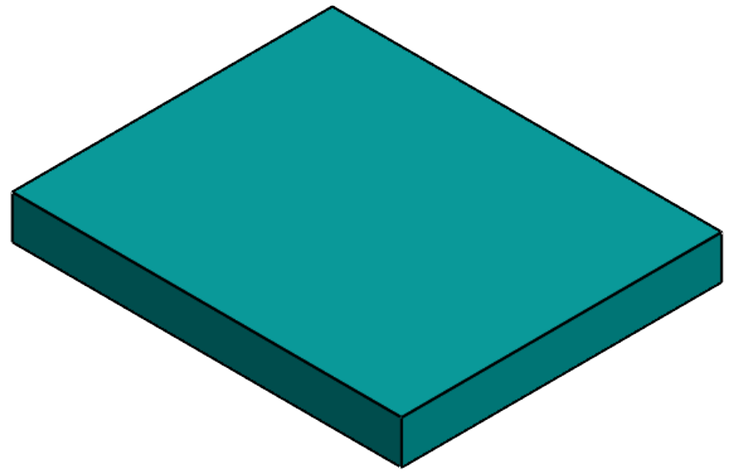



SUPPORT PLATE
QTY- 4 NOS

TITLE - GATE AUTOMATION				NIHVA TECHNOLOGIES PVT.LTD.PUNE
DWG NO - NTPL-290-PM-004-01-02-01				Website - www.nihva.com
	NAME	SIGNATURE	DATE	PROJECT NO - NTPL-290-PM
DRAWN	V.B.		16-08-2025	PRODUCT - SLIDING GATE
CHK'D	B.S.		16-08-2025	SITE LOCATION -AMRAVATI
APPV'D	V.T.		16-08-2025	TYPE 4
if any queries contact - design@nihva.com				REVISION -00 / QTY - 1
ALL DIMENSION ARE IN mm		A3		SCALE - / SHEET 10 OF 18

ITEM NO.	PART NUMBER	DESCRIPTION	QTY.
1	GUIDE PLATE	ID-14 (H)-79 (W)-10	8

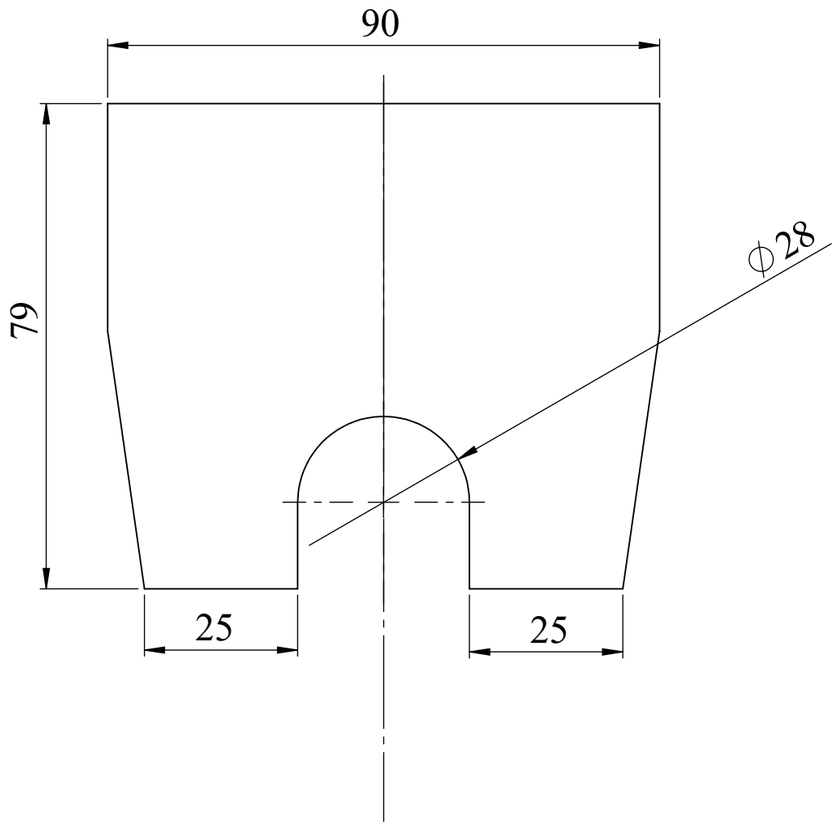

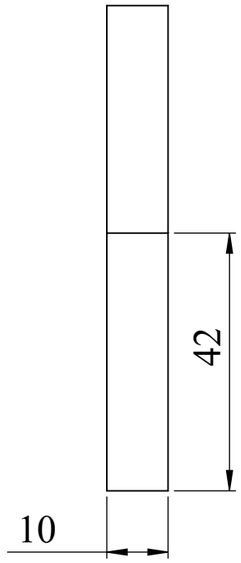


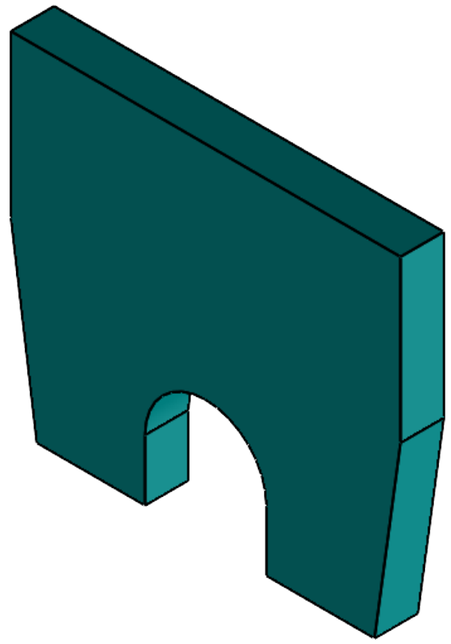


GUIDE PLATE
QTY- 8 NOS

TITLE - GATE AUTOMATION				NIHVA Technologies Pvt. Ltd.	NIHVA TECHNOLOGIES PVT.LTD.PUNE Website - www.nihva.com
DWG NO - NTPL-290-PM-004-01-02-02					
	NAME	SIGNATURE	DATE	PROJECT NO - NTPL-290-PM	
DRAWN	V.B.		16-08-2025	PRODUCT -SLIDING GATE	
CHK'D	B.S.		16-08-2025	SITE LOCATION -AMRAVATI	
APPV'D	V.T.		16-08-2025	TYPE 4	
if any queries contact - design@nihva.com				REVISION -00	QTY - 1
ALL DIMENSION ARE IN mm		A3		SCALE -	SHEET 11 OF 18

ITEM NO.	PART NUMBER	DESCRIPTION	QTY.
1	WHEEL	100x50	4

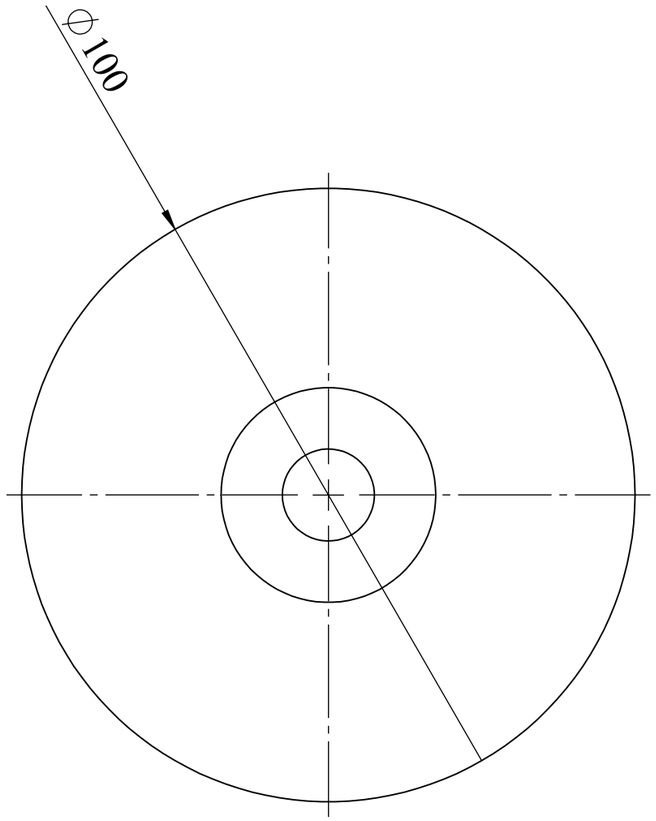

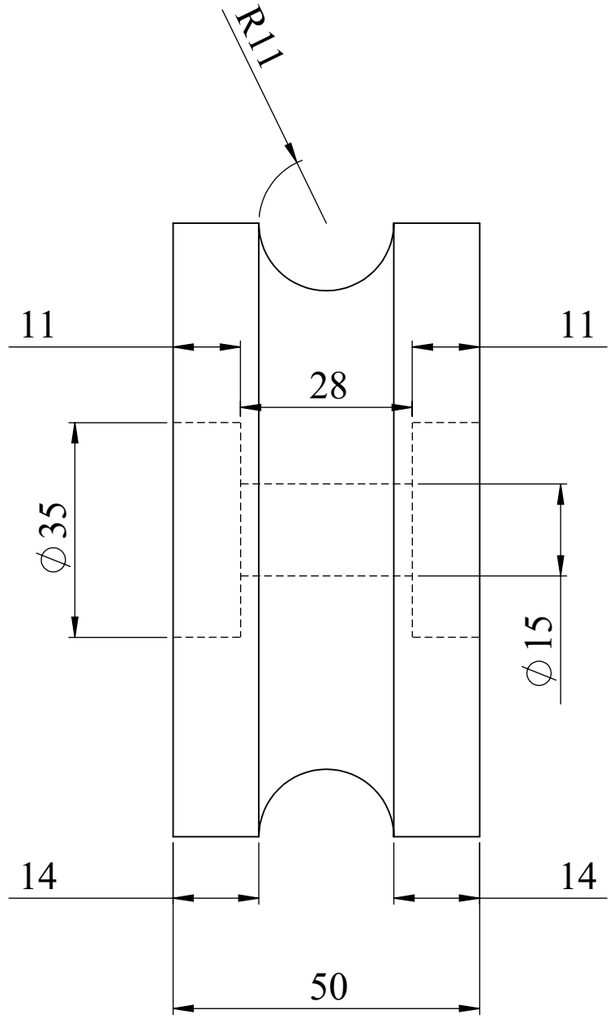




WHEEL
QTY- 4 NOS

TITLE - GATE AUTOMATION				NIHVA TECHNOLOGIES PVT.LTD.PUNE
DWG NO - NTPL-290-PM-004-01-02-03				Website - www.nihva.com
	NAME	SIGNATURE	DATE	PROJECT NO - NTPL -290-PM
DRAWN	V.B.		16-08-2025	PRODUCT -SLIDING GATE
CHK'D	B.S.		16-08-2025	SITE LOCATION -AMRAVATI
APPV'D	V.T.		16-08-2025	TYPE 4
if any queries contact - design@nihva.com				REVISION -00 / QTY - 1
ALL DIMENSION ARE IN mm		A3		SCALE - / SHEET 12 OF 18

ITEM NO.	PART NUMBER	DESCRIPTION	QTY.
1	WICKET GATE	1200 (W)x1675 (H)	1

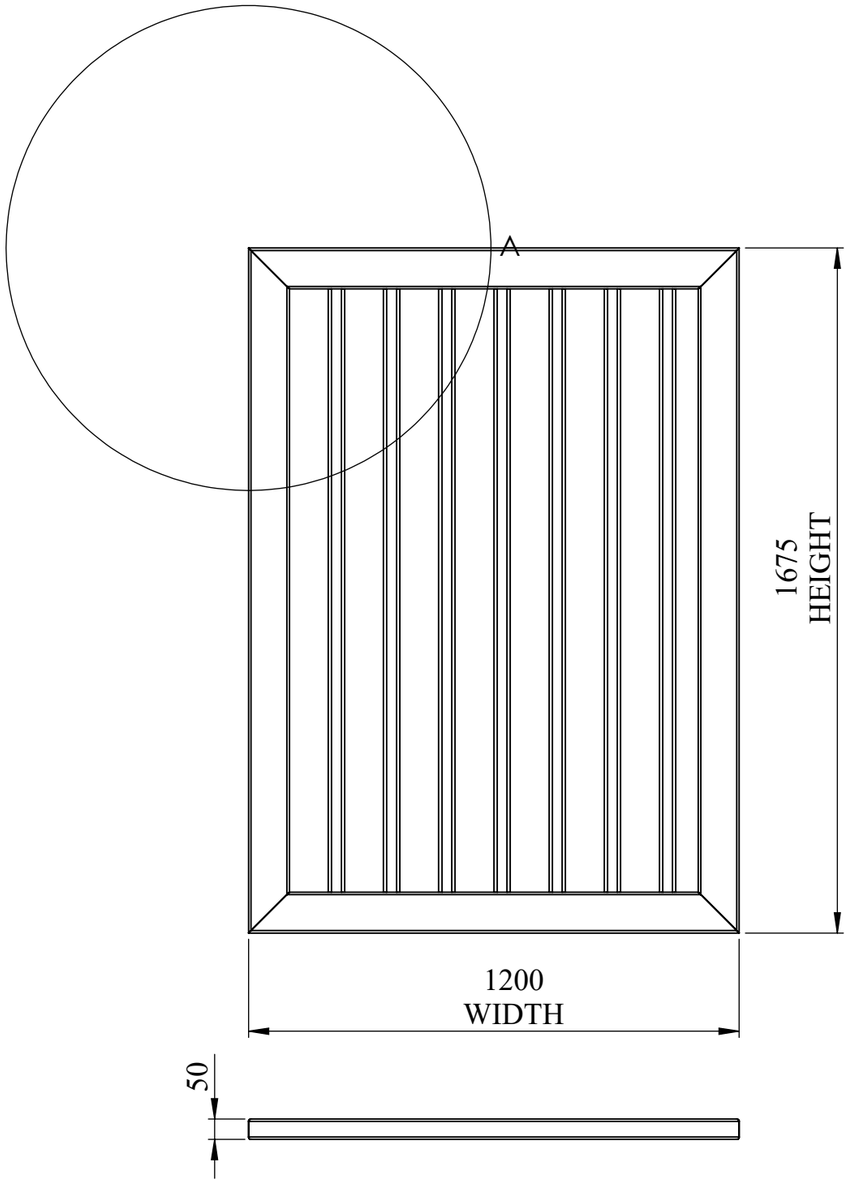




DETAIL A
SCALE 2 : 15


SUPPORT TUBE
QTY-7 NOS

TITLE - GATE AUTOMATION				NIHVA TECHNOLOGIES PVT.LTD.PUNE Website - www.nihva.com
DWG NO - NTPL-290-PM-004-04				
	NAME	SIGNATURE	DATE	PROJECT NO - NTPL-290-PM
DRAWN	V.B.		16-08-2025	PRODUCT - SLIDING GATE
CHK'D	B.S.		16-08-2025	SITE LOCATION - AMRAVATI
APPV'D	V.T.		16-08-2025	TYPE 4
if any queries contact - design@nihva.com				REVISION -00 / QTY - 1
ALL DIMENSION ARE IN mm		A3		SCALE - / SHEET 1 OF 2

ITEM NO.	PART NUMBER	DESCRIPTION	QTY.
1	FIXED GATE	1200 (W)x1675 (H)	1

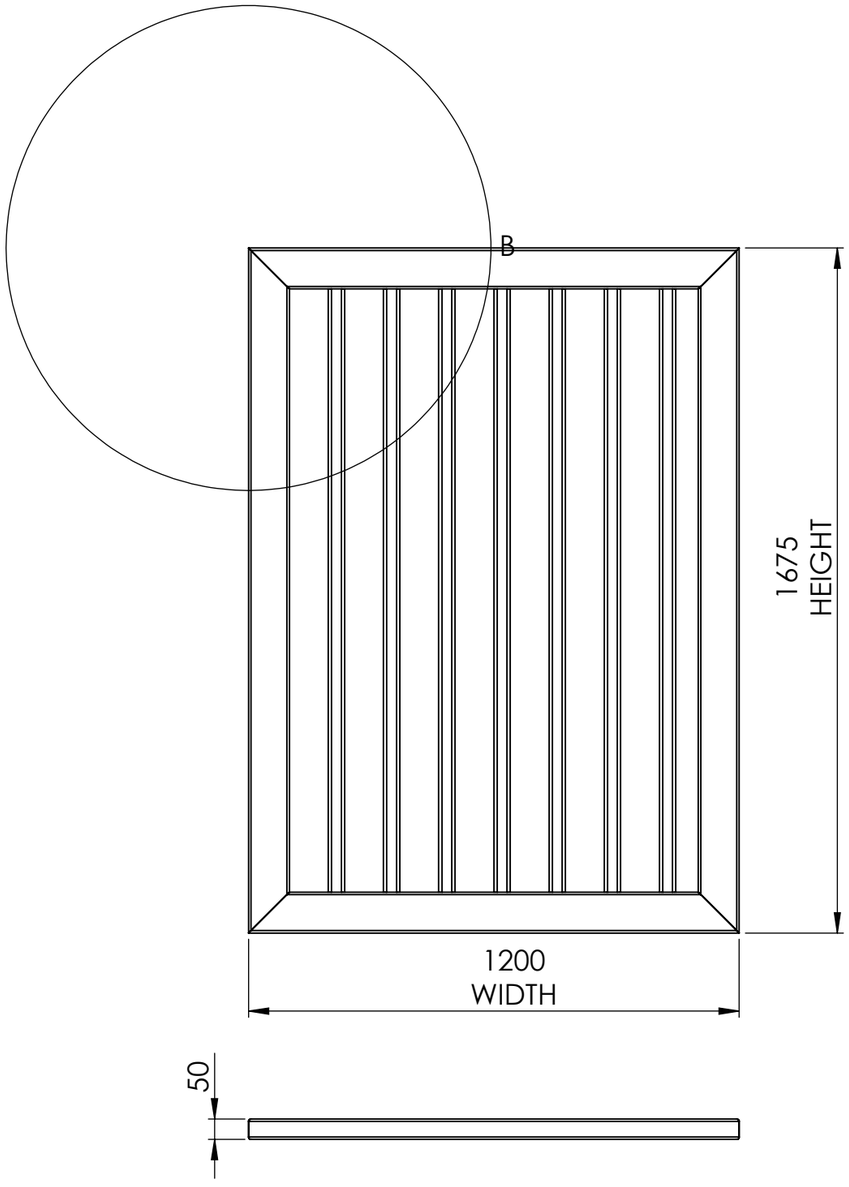


DETAIL B
SCALE 2 : 15

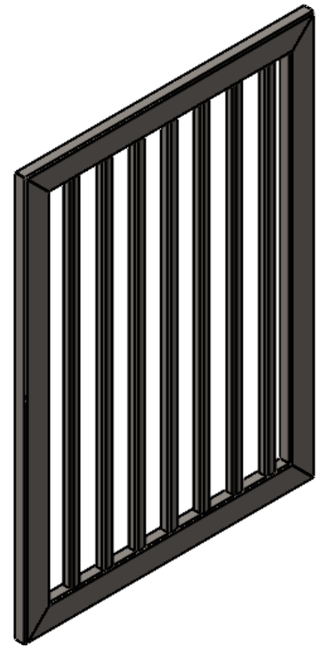



SUPPORT TUBE
QTY-7 NOS

TITLE - GATE AUTOMATION				NIHVA TECHNOLOGIES PVT.LTD.PUNE
DWG NO - NTPL-290-PM-004-05				Website - www.nihva.com
	NAME	SIGNATURE	DATE	PROJECT NO - NTPL-290-PM
DRAWN	V.B.		16-08-2025	PRODUCT - SLIDING GATE
CHK'D	B.S.		16-08-2025	SITE LOCATION - AMRAVATI
APPV'D	V.T.		16-08-2025	TYPE 4
if any queries contact - design@nihva.com				REVISION -00 / QTY - 1
ALL DIMENSION ARE IN mm		A3		SCALE - / SHEET 2 OF 2

ITEM NO.	PART NUMBER	DESCRIPTION	QTY.
1	EN8 BAR	OD- 20 MM	2
	ISMB BEAM	SIZE- 100 X 50 10610MM (L)	2

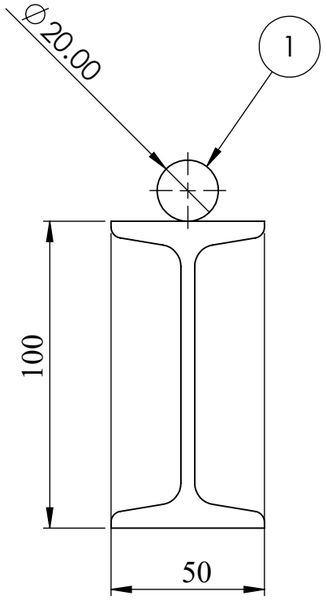

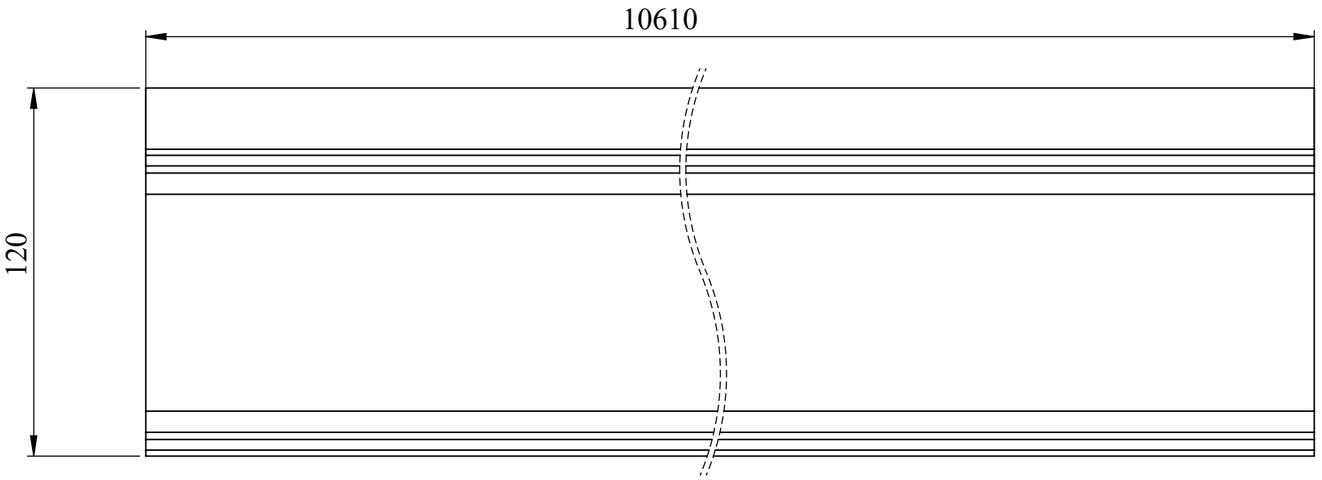


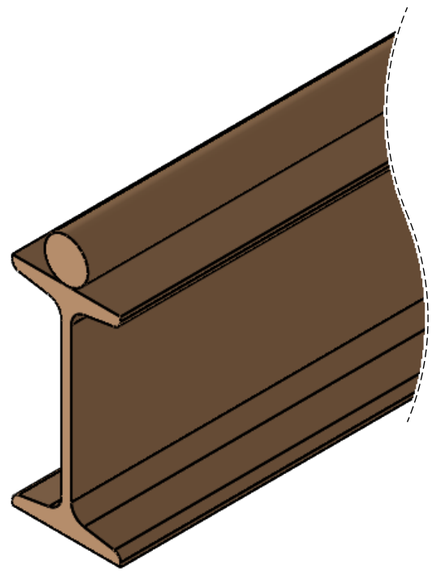


GATE TRACK
QTY- 2NOS

TITLE - GATE AUTOMATION				NIHVA Technologies Pvt. Ltd.	NIHVA TECHNOLOGIES PVT.LTD.PUNE Website - www.nihva.com
DWG NO - NTPL-290-PM-004-06					
	NAME	SIGNATURE	DATE	PROJECT NO - NTPL-290-PM	
DRAWN	V.B.		16-08-2025	PRODUCT -SLIDING GATE	
CHK'D	B.S.		16-08-2025	SITE LOCATION - AMRAVATI	
APPV'D	V.T.		16-08-2025	TYPE-4	
if any queries contact - design@nihva.com				REVISION -00	QTY - 1
ALL DIMENSION ARE IN mm			A3	SCALE -	SHEET 13 OF 21

ITEM NO.	PART NUMBER	DESCRIPTION	QTY.
1	M14 ANCHOR	M14X150	70

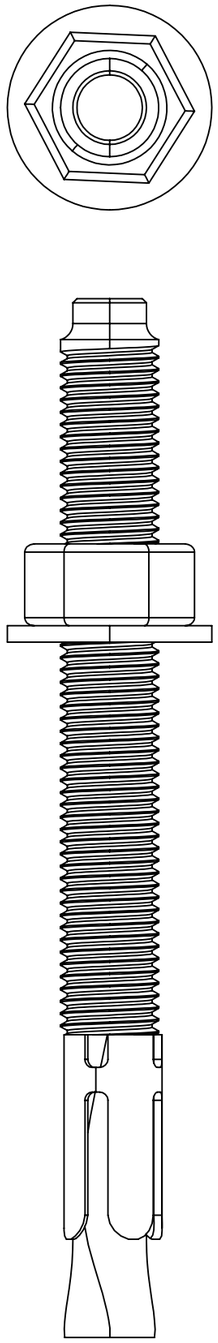


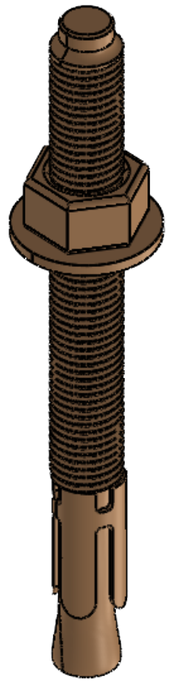


NOTE -
M14 X 150 MM ANCHOR BOLT
QTY- 70 NOS


TITLE -GATE AUTOMATION				NIHVA TECHNOLOGIES PVT.LTD.PUNE
DWG NO - NTPL-290-PM-004-07				Website - www.nihva.com
	NAME	SIGNATURE	DATE	PROJECT NO - NTPL-290-PM
DRAWN	V.B.		16-08-2025	PRODUCT -SLIDING GATE
CHK'D	B.S.		16-08-2025	SITE LOCATION - AMRAVATI
APPV'D	V.T.		16-08-2025	TYPE 4
if any queries contact - design@nihva.com				REVISION -00 / QTY - 1
ALL DIMENSION ARE IN mm		A3		SCALE - / SHEET 14 OF 21

ITEM NO.	PART NUMBER	DESCRIPTION	QTY.
1	NYLON STOPPER		2
2	NYLON STOPPER PLATE	135X135X10	2

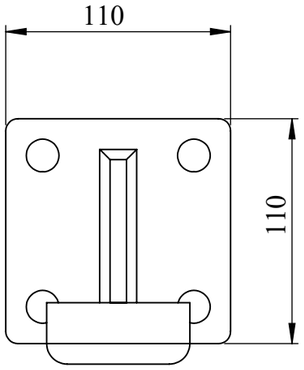


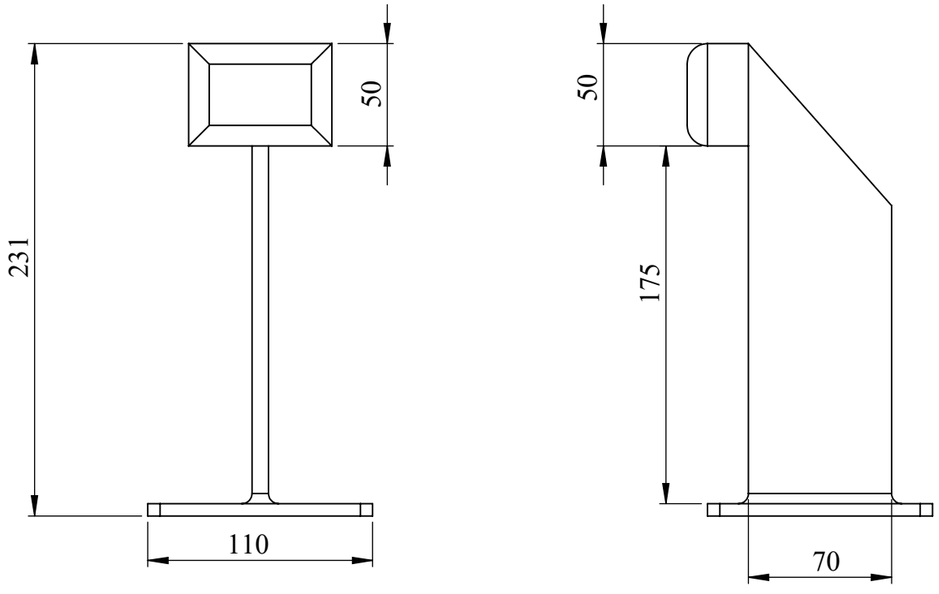


NOTE -
NYLON STOPPER
QTY- 2 NOS

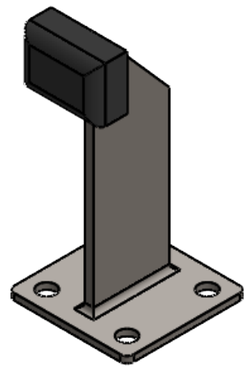


TITLE -GATE AUTOMATION				NIHVA TECHNOLOGIES PVT.LTD.PUNE
DWG NO - NTPL-290-PM-004-08				Website - www.nihva.com
	NAME	SIGNATURE	DATE	PROJECT NO - NTPL-290-PM
DRAWN	V.B.		16-08-2025	PRODUCT -SLIDING GATE
CHK'D	B.S.		16-08-2025	SITE LOCATION - AMRAVATI
APPV'D	V.T.		16-08-2025	TYPE 4
if any queries contact - design@nihva.com				REVISION -00 / QTY - 1
ALL DIMENSION ARE IN mm		A3		SCALE - / SHEET 15 OF 21

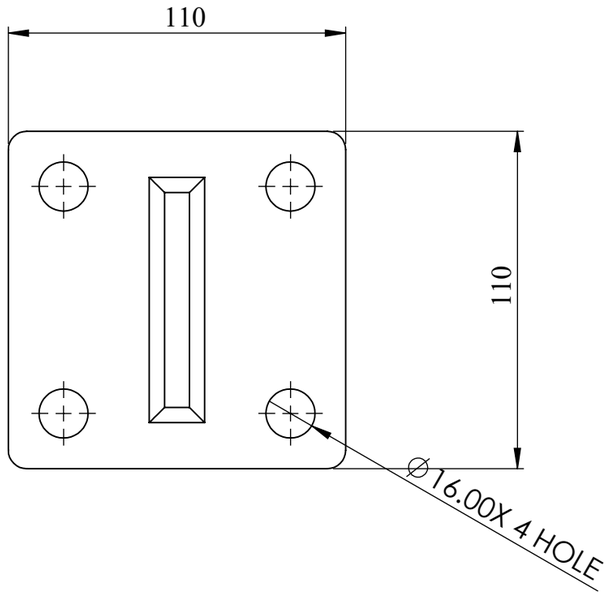

ITEM NO.	PART NUMBER	DESCRIPTION	QTY.
2	NYLON STOPPER PLATE	135X135X10	2

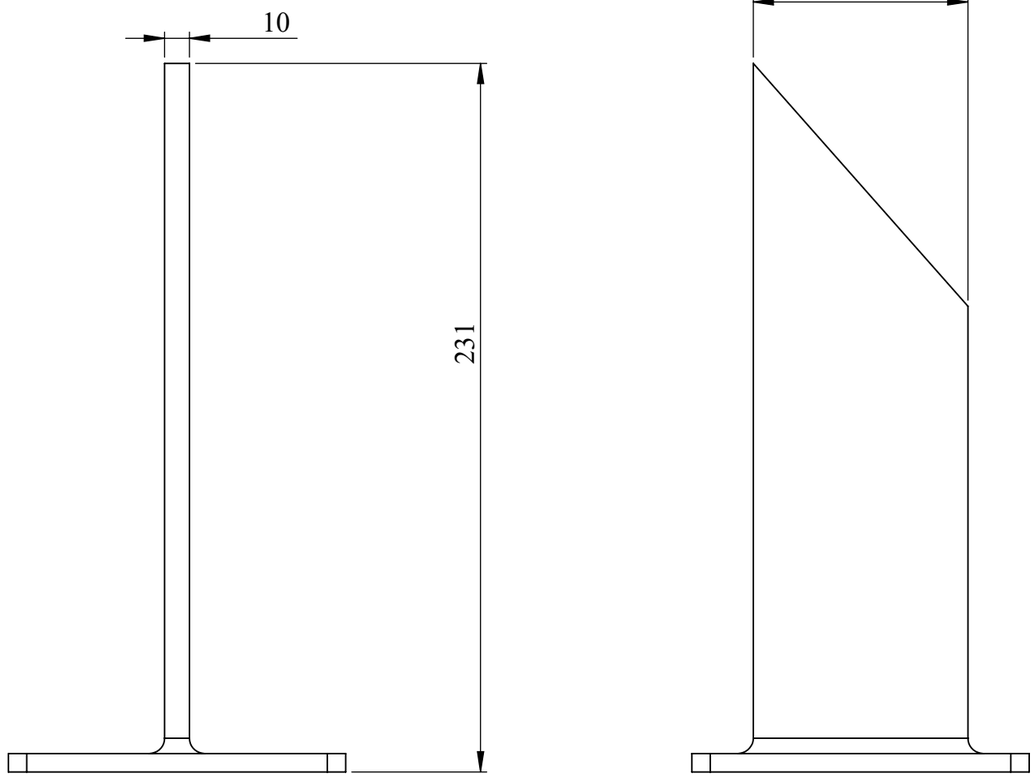



NOTE -
NYLON STOPPER
QTY- 2 NOS

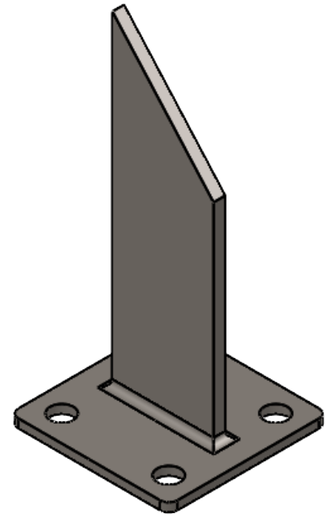


TITLE -GATE AUTOMATION				NIHVA TECHNOLOGIES PVT.LTD.PUNE Website - www.nihva.com
DWG NO - NTPL-290-PM-004-08-01				
	NAME	SIGNATURE	DATE	PROJECT NO - NTPL-290-PM
DRAWN	V.B.		16-08-2025	PRODUCT -SLIDING GATE
CHK'D	B.S.		16-08-2025	SITE LOCATION - AMRAVATI
APPV'D	V.T.		16-08-2025	TYPE 4
if any queries contact - design@nihva.com				REVISION -00 / QTY - 1
ALL DIMENSION ARE IN mm		A3		SCALE - / SHEET 16 OF 21

ITEM NO.	PART NUMBER	DESCRIPTION	QTY.
1	NYLON STOPPER		2

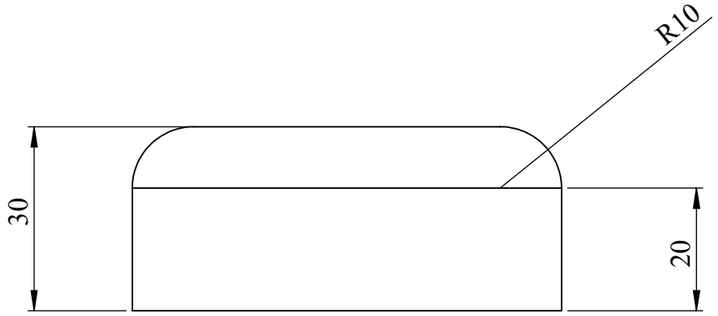

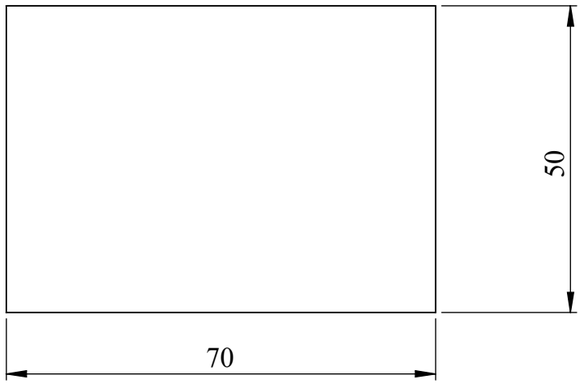


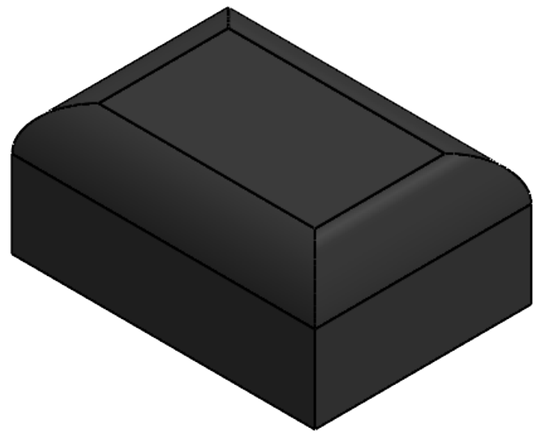


NOTE -
NYLON STOPPER
QTY- 2 NOS

TITLE -GATE AUTOMATION				NIHVA TECHNOLOGIES PVT.LTD.PUNE
DWG NO - NTPL-290-PM-004-08-02				Website - www.nihva.com
	NAME	SIGNATURE	DATE	PROJECT NO - NTPL-290-PM
DRAWN	V.B.		16-08-2025	PRODUCT -SLIDING GATE
CHK'D	B.S.		16-08-2025	SITE LOCATION - AMRAVATI
APPV'D	V.T.		16-08-2025	TYPE 4
if any queries contact - design@nihva.com				REVISION -00 / QTY - 1
ALL DIMENSION ARE IN mm		A3		SCALE - / SHEET 17 OF 21

ITEM NO.	PART NUMBER	DESCRIPTION	QTY.
1	TOWER BOLT HOLLOW PIPE	DIA- 18MM (3 MM THK)	3
2	Tower Bolt	DIA- 15MM 300(L)	3

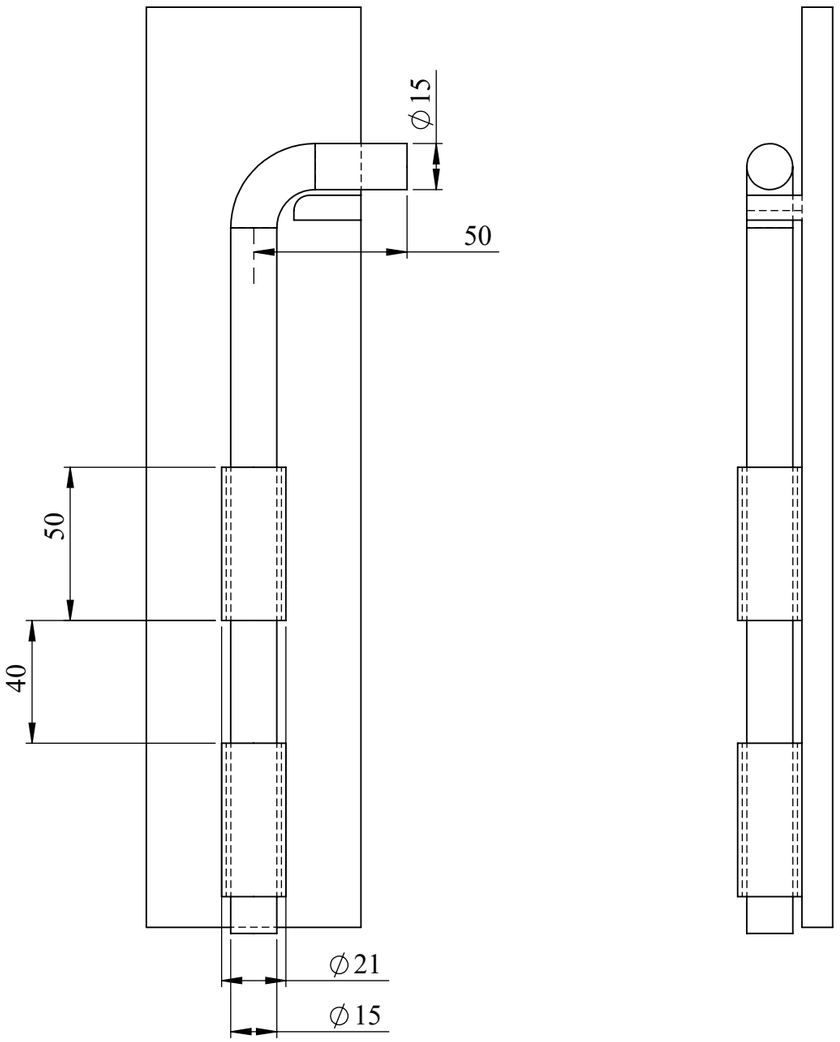


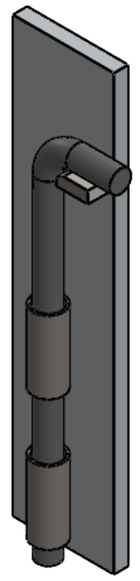


NOTE -
TOWER BOLT
QTY- 3 NOS

TITLE -GATE AUTOMATION				NIHVA TECHNOLOGIES PVT.LTD.PUNE
DWG NO - NTPL-290-PM-004-09				Website - www.nihva.com
	NAME	SIGNATURE	DATE	PROJECT NO - NTPL-290-PM
DRAWN	V.B.		16-08-2025	PRODUCT -SLIDING GATE
CHK'D	B.S.		16-08-2025	SITE LOCATION - AMRAVATI
APPV'D	V.T.		16-08-2025	TYPE 4
if any queries contact - design@nihva.com				REVISION -00 / QTY - 1
ALL DIMENSION ARE IN mm		A3		SCALE - / SHEET 18 OF 21

ITEM NO.	PART NUMBER	DESCRIPTION	QTY.
1	WICKET GATE	1200X1675	1
2	BOTTOM SIDE HINGS PLATE	80X75X6	2
3	MALE - FEMALE Hings	3 INCH	2
4	hing bearing		2
5	UPPER SUPPORT HINGS PLATE	100X197X10	2
7	female hings	3 INCH	2

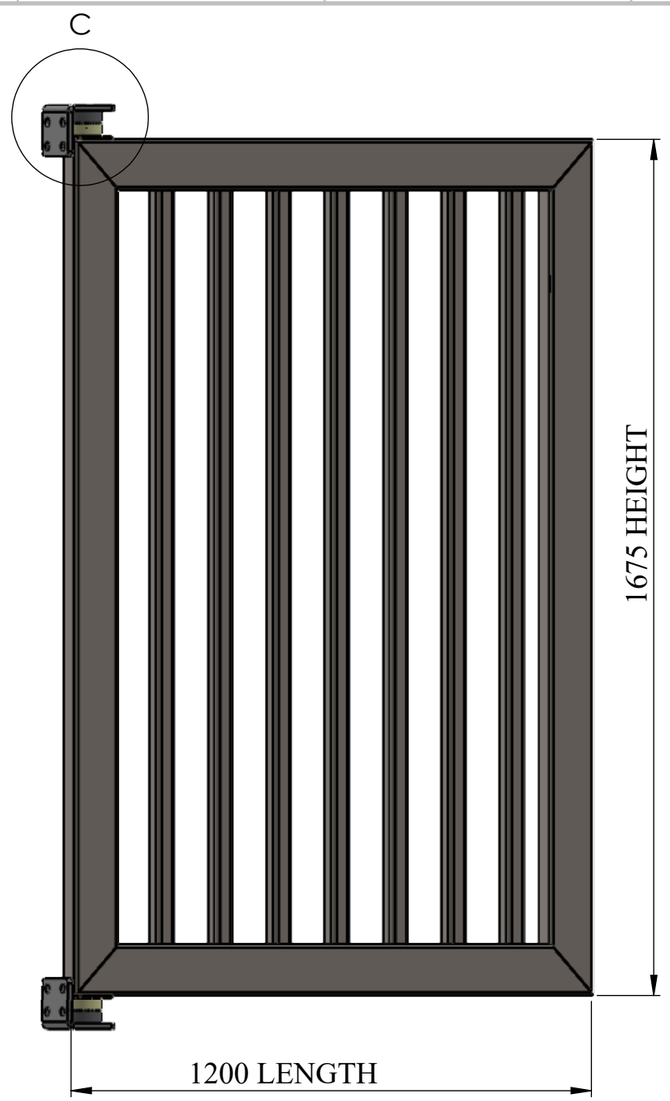

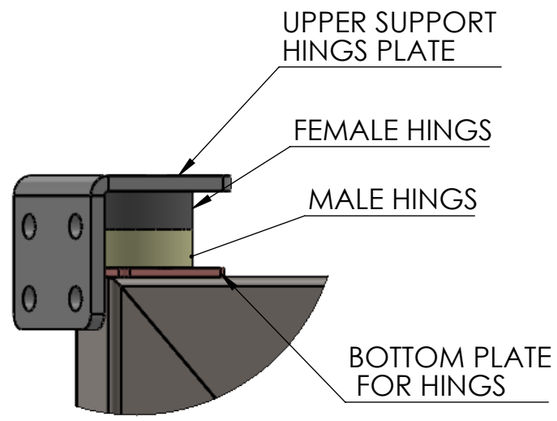

DETAIL C
SCALE 1 : 4







QTY- 1NOS

TITLE - RETRACTABLE ROOF				NIHVA TECHNOLOGIES PVT.LTD.PUNE
DWG NO - NTPL290-PM-004-11			QTY - 1	Website - www.nihva.com
	NAME	SIGNATURE	DATE	PROJECT NO - NTPL290-PM
DRAWN	V.B.		16-08-2025	PRODUCT - SLIDING GATE
CHK'D	B.S.		16-08-2025	SITE LOCATION - AMRAVATI
APPV'D	V.T.		16-08-2025	TYPE 4
if any queries contact - design@nihva.com				REVISION -00
ALL DIMENSION ARE IN mm			A3	SCALE -
				SHEET 19 OF 21

ITEM NO.	PART NUMBER	DESCRIPTION	QTY.
1	Bottom Hinges Plate	80x75x6 mm THK	2

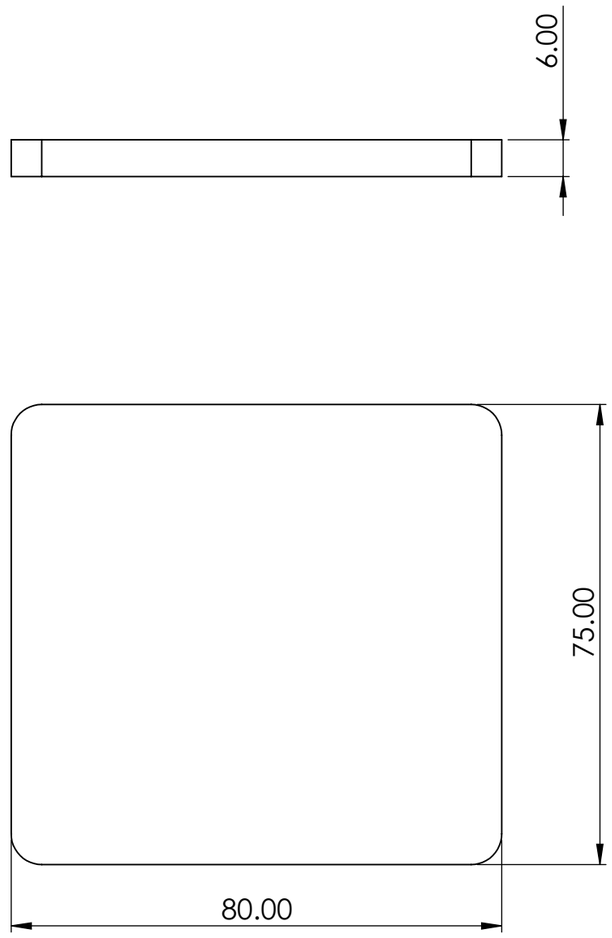


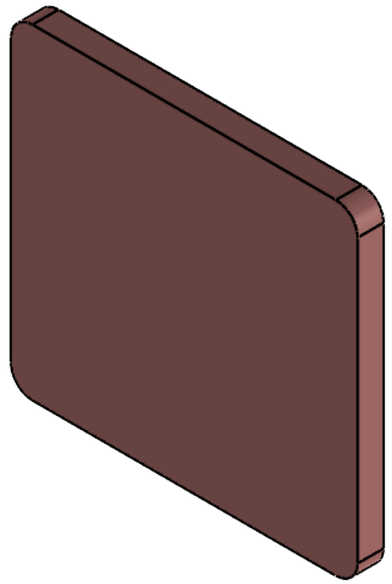


BOTTOM PLATE FOR HINGES
SIZE:- 80X75X6MM THK
MATERIAL:- MS
QTY:- 2 NOS

TITLE -GATE AUTOMATION				NIHVA TECHNOLOGIES PVT.LTD.PUNE
DWG NO - NTPL-290-PM-004-11-01				Website - www.nihva.com
	NAME	SIGNATURE	DATE	PROJECT NO - NTPL-290-PM
DRAWN	V.B.		16-08-2025	PRODUCT -SLIDING GATE
CHK'D	B.S.		16-08-2025	SITE LOCATION - AMRAVATI
APPV'D	V.T.		16-08-2025	TYPE 4
if any queries contact - design@nihva.com				REVISION -00 / QTY - 1
ALL DIMENSION ARE IN mm		A3		SCALE - / SHEET 20 OF 21

ITEM NO.	PART NUMBER	DESCRIPTION	QTY.
1	UPPER SUPPORT PLATE	100X197X10 THK	2

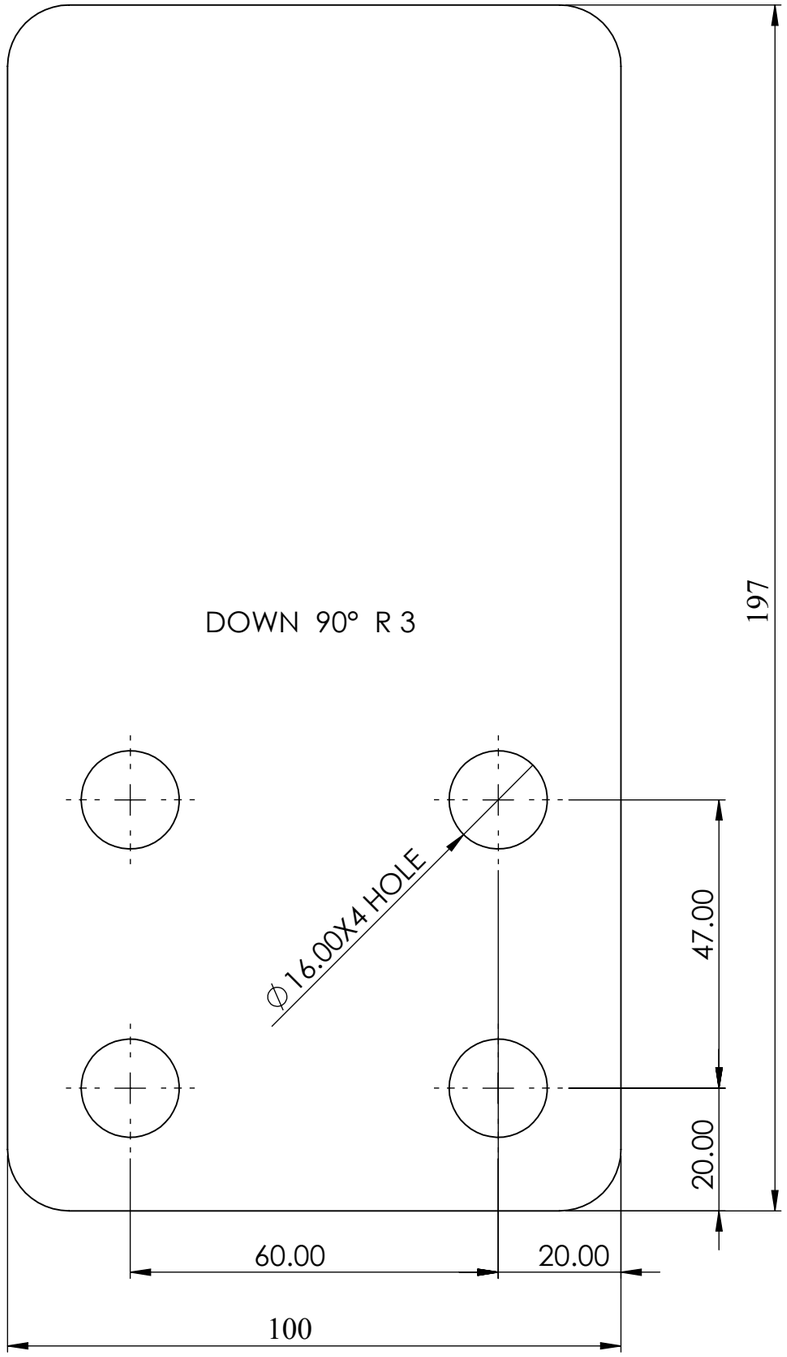

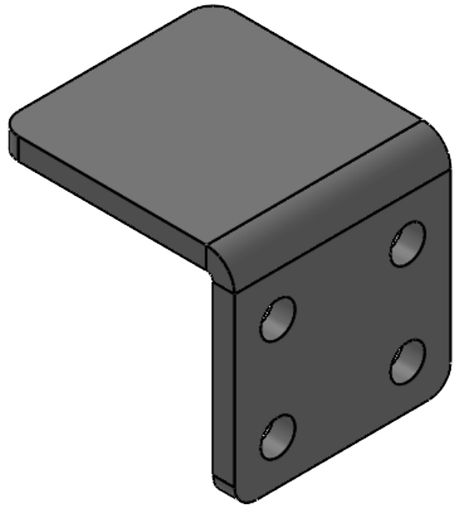

UPPER SUPPORT PLATE FOR HINGES
SIZE:- 100X197X10THK
MATERIAL:- MS
QTY:- 2 NOS

TITLE -GATE AUTOMATION				NIHVA TECHNOLOGIES PVT.LTD.PUNE
DWG NO - NTPL-290-PM-004-11-02				Website - www.nihva.com
	NAME	SIGNATURE	DATE	PROJECT NO - NTPL-290-PM
DRAWN	V.B.		16-08-2025	PRODUCT -SLIDING GATE
CHK'D	B.S.		16-08-2025	SITE LOCATION - AMRAVATI
APPV'D	V.T.		16-08-2025	TYPE 4
if any queries contact - design@nihva.com				REVISION -00 / QTY - 1
ALL DIMENSION ARE IN mm		A3		SCALE - / SHEET 21 OF 21