




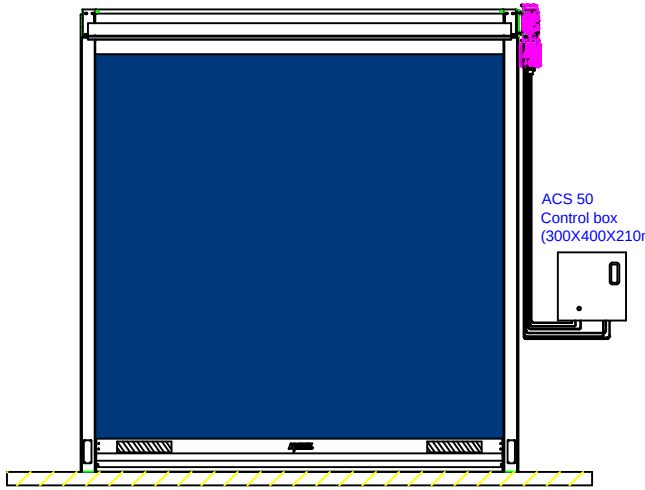


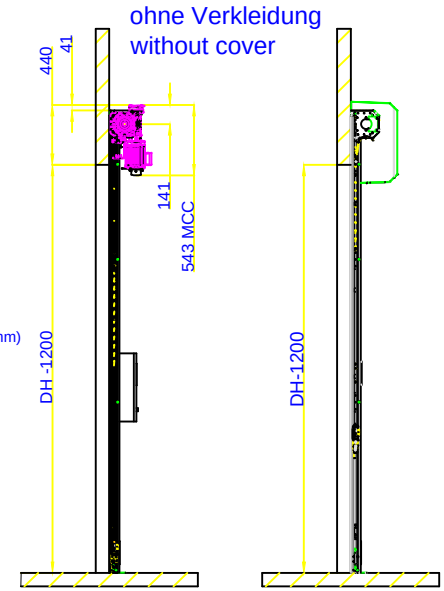

STRUCTURE FOR HSD

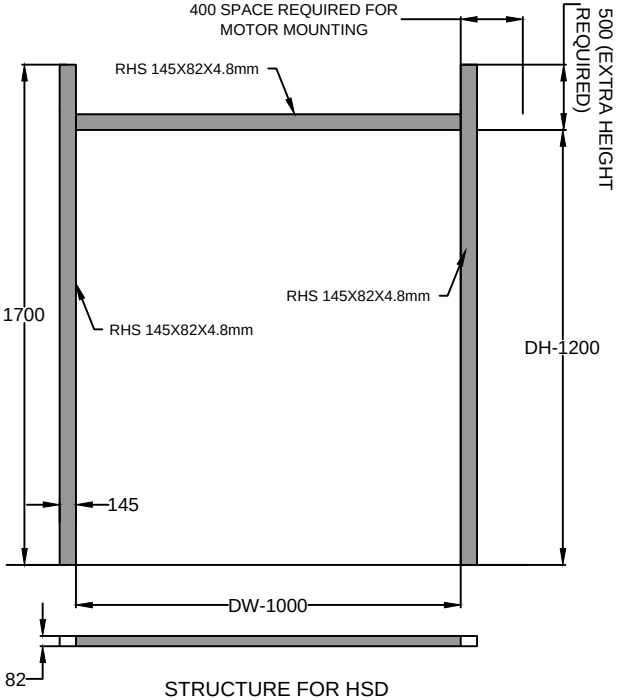

ohne Verkleidung
without cover

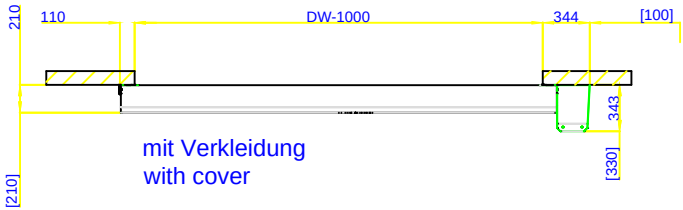

mit Verkleidung
with cover

Tolerance ±3 mm (for all dimensions)

Dimensions in [ ] ==> clearance for installation

COLORS -
1. BLUE (RAL 5002)
CURTAIN TYPE:-ROLLTEX

CLEAR WIDTH(DW)	CLEAR HEIGHT(DH)	MOTOR MOUNTING	QUANTITY
1000mm	1200mm	RIGHT SIDE	01 NOS

NOTE -
1.STRUTURE REQUIRED FOR HSD IS IN CLIENT'S SCOPE.
2.CLIENT HAS TO CONFIRM MOTOR POSITION(RIGHT/LEFT SIDE) AS PER SITE CONDITIONS.
3.CLIENT HAS TO CONFIRM COLOR OF CURTAIN.

This drawing & design is the property of NIHVA TECHNOLOGIES. Not to be sold or copied to any other concern.

TITLE: HIGH SPEED DOOR
RP300 & STRUCTURE

	NAME	SIGN	DATE
DRAWN	SURAJ		30/07/18
CHECK	PRADEEP		30/07/18
APPV'ED	R.D		30/07/18

If any queries contact : design@nihva.com

ALL DIMENSION ARE IN mm

NIHVA
NIHVA TECHNOLOGIES PVT. LTD.
NIHVA TECHNOLOGIES PVT. LTD. PUNE
Tel : 020 66304033
Email:- info@nihva.com
Website:- www.nihva.com

CLIENT :- KIRPEKAR ENGINEERING PVT. LTD.
PROJECT :-
LOCATION :- HINJEWADI PHASE-2
DWG. NO. :- NIHVA/18-19/0090 REV.:- 0
SCALE: NTS WT: SHEET: 01 OF 01