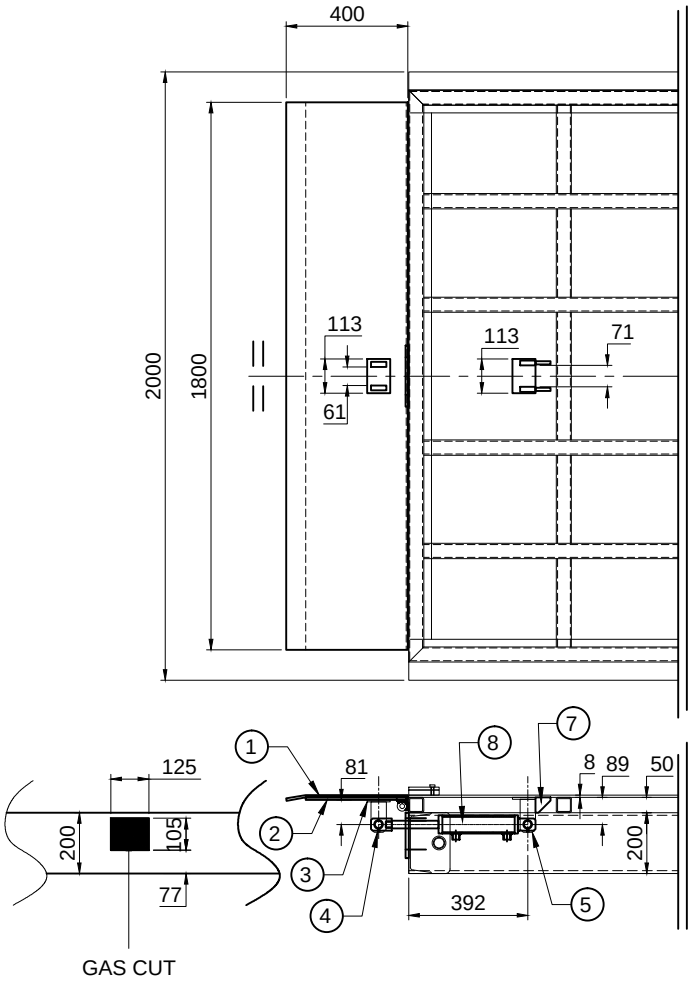

1. CHEQ.SHEET 400 X 8 THK X 1800L = 1 NOS
2. CHEQ.SHEET 330 X 8 THK X 1800L = 1 NOS
3. FLAT 75 X 6 X 113L = 2 NOS
4. FLAT 50 X 16 X 100L = 2 NOS
5. FLAT 50 X 16 X 108L = 2 NOS
6. ALLEN BOLT M8 X 25L = 2 NOS
7. RIB 50 X 10 X 50L = 2 NOS
8. STD LIP CYLINDER = 1 NO
9. USE OLD BUSH AS IT IS.

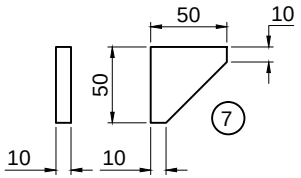

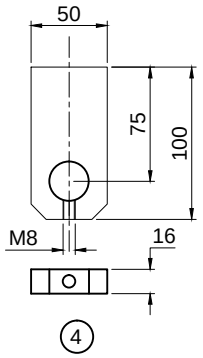

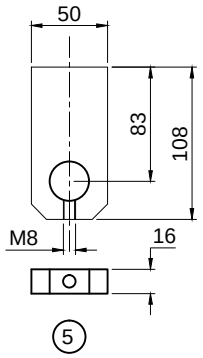

This drawing & design is the property of NIHVA TECHNOLOGIES. Not to be sold or copied to any other concern.

TITLE				
LIP CYLINDER MOUNTING				NIHVA TECHNOLOGIES PVT. LTD.
	NAME	SIGN	DATE	
DRAWN	P.A		20.12.2018	CLIENT -
CHECK	R.D		20.12.2018	PROJECT -
APPRD.	V.T		20.12.2018	SITE LOCATION -
If any queries contact : design@nihva.com				DWG. NO. : NIHVA/18-19/MFG/NSL1002/10 / REV- 0
ALL DIMENSION ARE IN mm				SCALE: NTS / WT: / SHEET: 01 OF 01

NIHVA TECHNOLOGIES PVT. LTD. PUNE
Tel : 020 66304033
Email:- info@nihva.com
Website:- www.nihva.com