
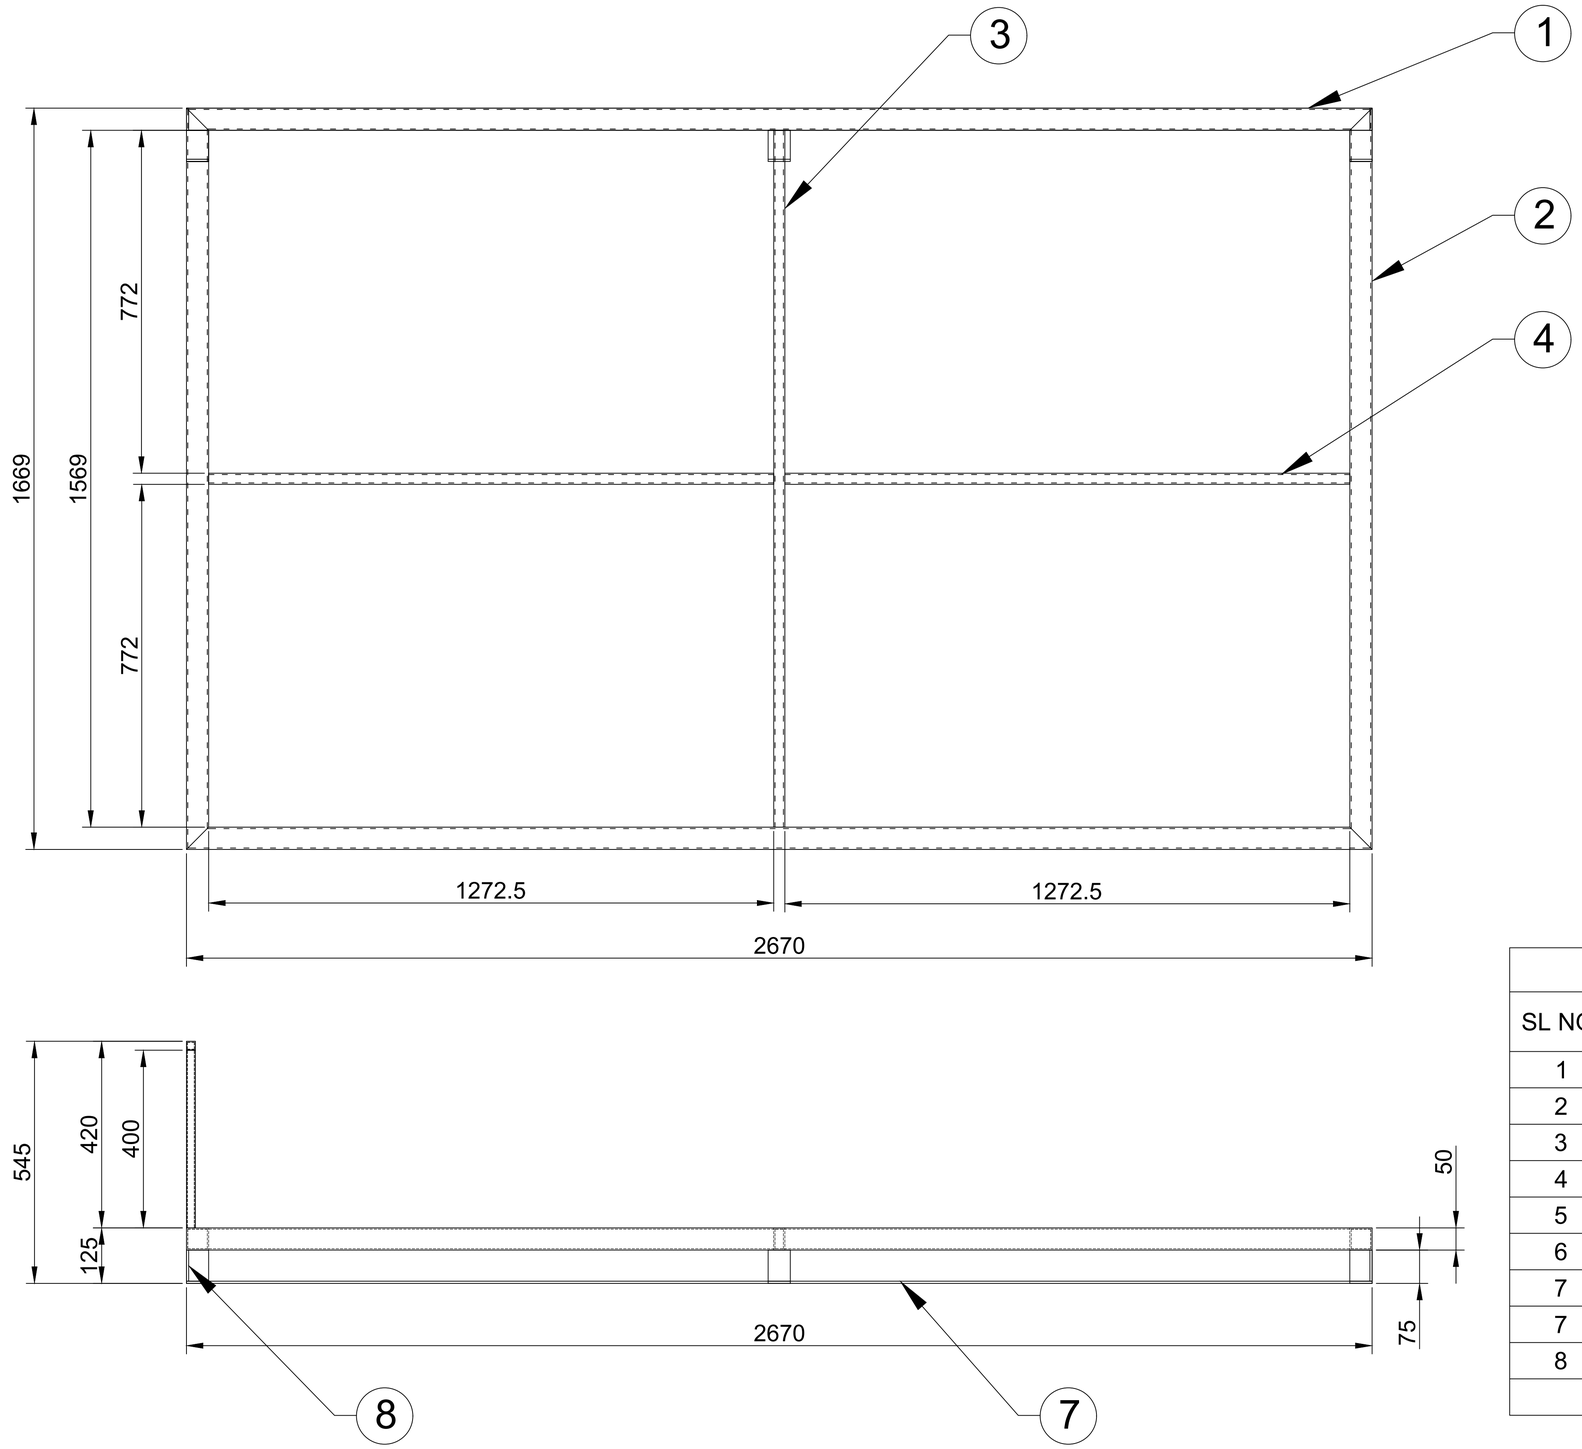


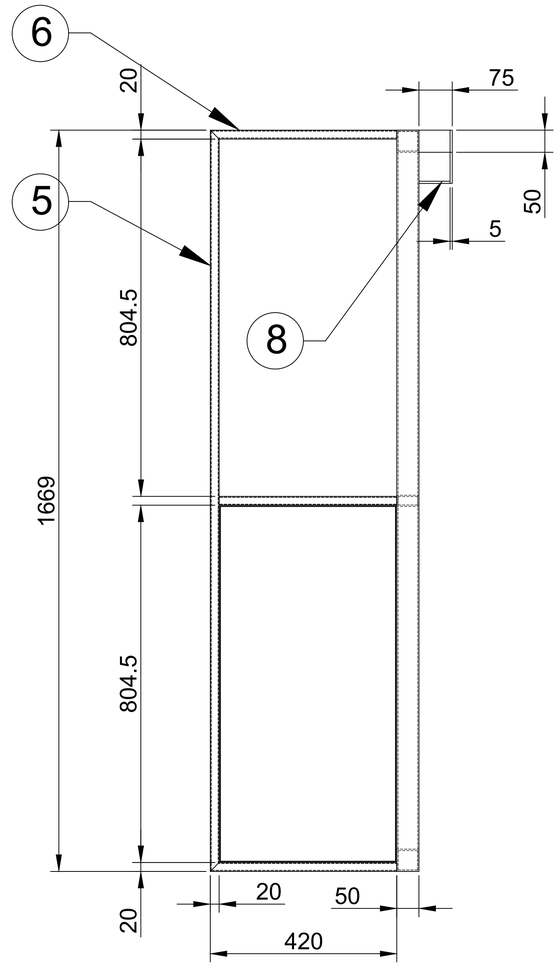

BOM FOR 1 LEAF

SL NO.	DESCRIPTION	SPECIFICATION	QTY	WEIGHT
1	MS SQ. TUBE	50X50X3X2670L	2NOS	22.99
2	MS SQ. TUBE	50X50X3X1669L	2NOS	14.37
3	MS REC. TUBE	50X25X3X1569L	1NO	4.91
4	MS SQ. TUBE	50X25X3X1272.5L	2 NOS	7.96
5	MS SQ. TUBE	20X20X2X1669L	1 NO	1.8
6	MS SQ. TUBE	20X20X2X420L	2 NOS	0.9
7	MS SQ. TUBE	20X20X2X400L	1 NO	0.43
7	M.S. FLAT	50 X 5 X 2670 L	1 NO	5.24
8	M.S. FLAT	50 X 5 X 70 L	8 NOS	1.08
	TOTAL			59.6800

Note:-

1.All Dimension are in MM

2.Kindly Mentain the given Dimensions

Rev No.	Revision	Date	Revised By

This drawing & design is the property of NIHVA TECHNOLOGIES. Not to be sold or copied to any other concern.

TITLE:- MASTER LEAF

NIHVA TECHNOLOGIES PVT. LTD.

NIHVA TECHNOLOGIES PVT. LTD. PUNE
Tel : 020 66304033
Email:- info@nihva.com
Website:- www.nihva.com

	NAME	DATE	SIGN
DRAWN	NIRMALA	15/04/2023	
CHECK	A.K.	15/04/2023	
APPRD.	V.T.	15/04/2023	

If any queries contact : design1@nihva.com

ALL DIMENSION ARE IN mm

CLIENT - Cloos India Welding Technology Pvt. Ltd

LOCATION -

PRODUCT - TELESCOPIC SLIDING GATE | QTY- 4

DWG NO:- NIHVA/23-24/MFG /0120 | REV-00

SCALE: NTS | SCALE:-- 1:1 | SHEET: 01 OF 01