

THIS PRINT IS THE PROPERTY OF NIHVA TECHNOLOGIES PVT LTD
RETURNED UPON REQUSETHIS PART MUST NOT BE SOLD TO ANY OTHER CONCERN

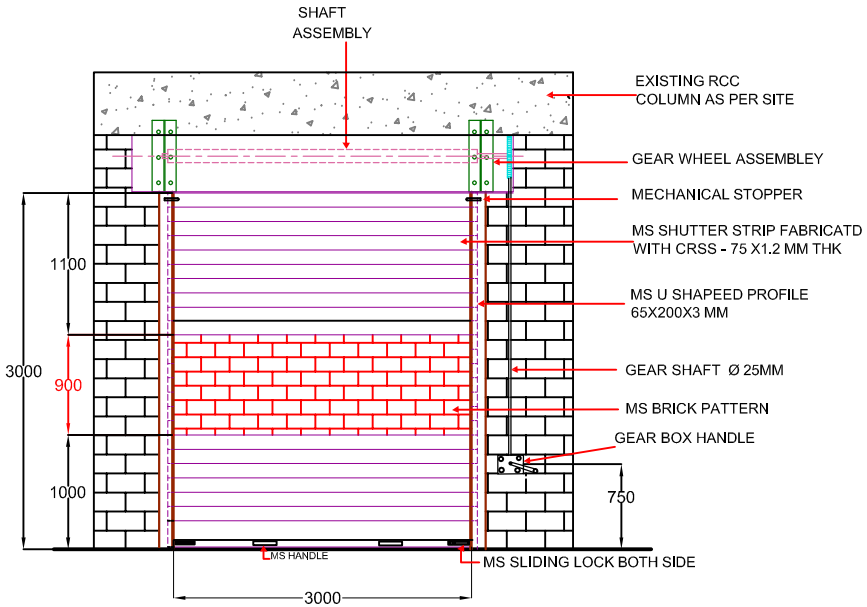


INSIDE ELEVATION


Clear Opening size:-
(W)3.0m x (H)3.0m

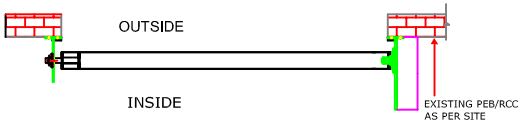


PLAN

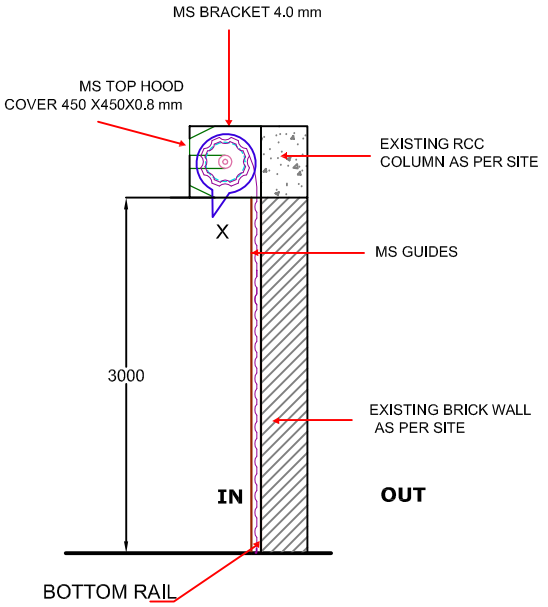


SIDE VIEW

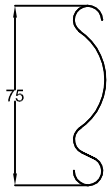

Curve Type Slat Profile

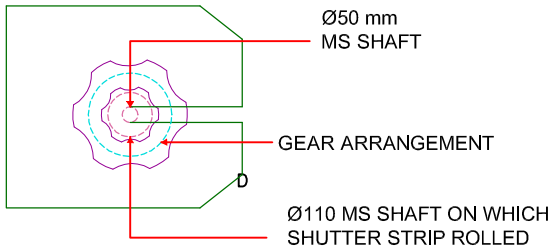

Bracket

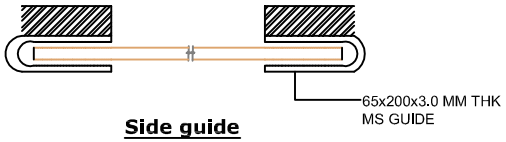

Side guide

Location :- Substation
Size :- 3.0m(W) X 3.0M (H)

TITLE: Grilled Manual Gear Operated Rolling Shutter	**DO NOT SCALE DRAWING**		NIHVA TECHNOLOGIES PVT. LTD. Pune:-411044 Tel :- 020 66304033 Email :- info@nihva.com
		SIGN	DATE
CLIENTS APPROVEL:–	DRAWN	Anil	
	CHECK		
	ENG		**CLIENT:** REWARD CONSTRUCTION
	APPRD.		**PROJECT / SITE:** IR PROJECT/ NAROL - AHEMDABAAD
	PROD		**PRODUCT NAME:**
ALL DIMENSION ARE IN M.M.	MFG		**DWG. NO.:** NVA/REWARD/01/R1
	Ref. No.		**REV.:** 0
			SCALE: NTS **WT:** **SHEET:** 1 OF 1