
PRODUCED BY AN AUTODESK STUDENT VERSION

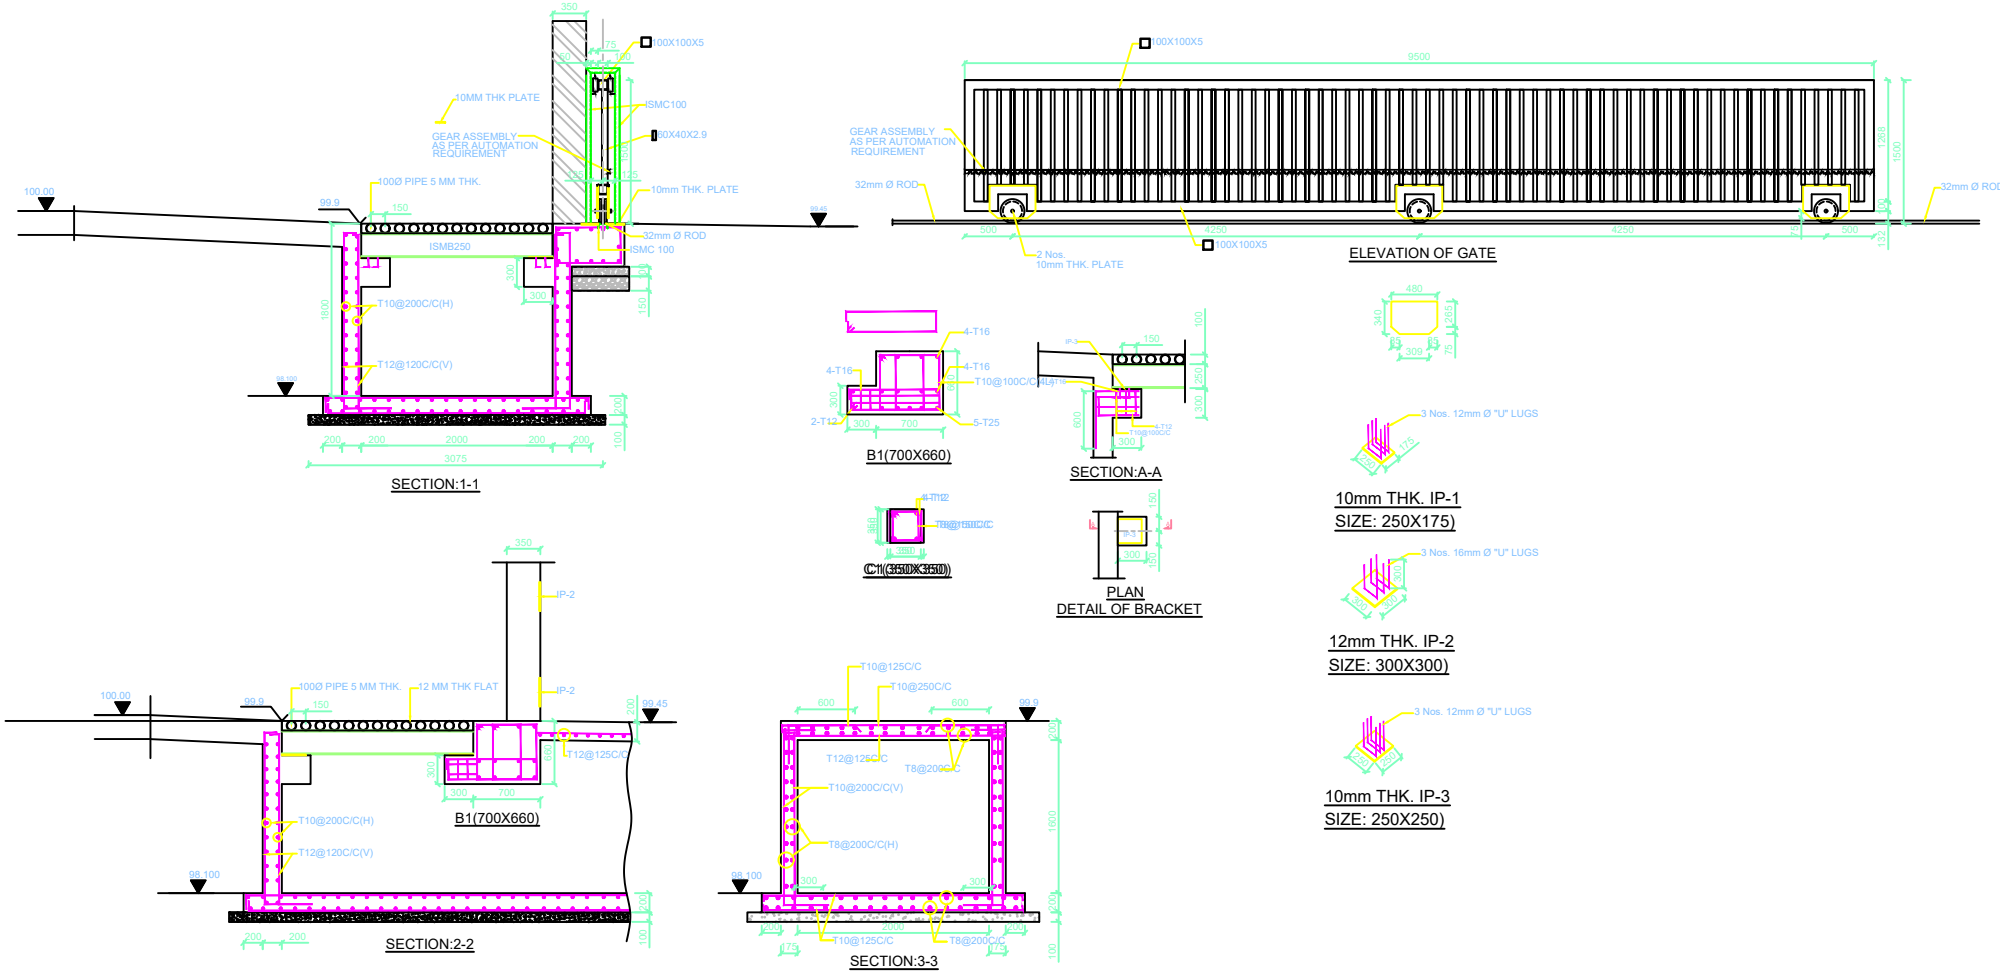

DETAIL OF COMPOUND WALL SECTION-1

NOTE: USE M25 GRADE CONCRETE & FE415 GRADE STEEL

This drawing is the property of AJIT NAIR ARCHITECTS ATELIER Pvt. Ltd. and their associate Project Consultants.
The drawing shall not be used or copied for purpose other then for which it has been issued.
All drawings to be read in conjunction with relevant Architectural and Consultant's drawings.
Any ambiguity in the drawing shall be brought to the notice of the Architect prior to initiating
All dimensions are to be read and not to be measured.

Comments and Instructions

REV NO	DATE	DESCRIPTION	CHECKED BY
1	07/11/15	REVESION IN F.G.L. AS PER MOM-06-11-15	H.A.P.

Associate Consultants

ACOUSTICS		CONDITIONING	
CIVIL AND STRUCTURAL	COMTEN ENGINEERS STRUCTURAL CONSULTANTS 3rd Floor, Kunal Complex, Deluxe, Nizampura Road, Vadodara. Ph. : (O) 0265 3916556. E-mail : comtenengineers@gmail.com	LANDSCAPING	
ELECTRICAL		SANITARY & FIRE FIGHTING	

CLIENT	ABB INDIA LTD.
PROJECT	INFRA. DEVELOPMENT AT NASHIK
TITLE	GATE & COMPOUND WALL DETAILS
SCALE	NTS
DRG NO :	1297-C-03
DATE :	24/10/15

N

AJIT NAIR ARCHITECTS
ATELIER PVT. LTD.
Architects Atelier
Project Management Consultants – Planners
Interior Designers – Industrial & Landscape Architects
P – 17 , SANGATH BUNGALOWS , B/H GEB SUBSTATION , OFF SAMA – SAVLI ROAD , VADODARA – 9
Ph : +91 265 2710347 Email: studio@archajitnair.com

PRODUCED BY AN AUTODESK STUDENT VERSION