


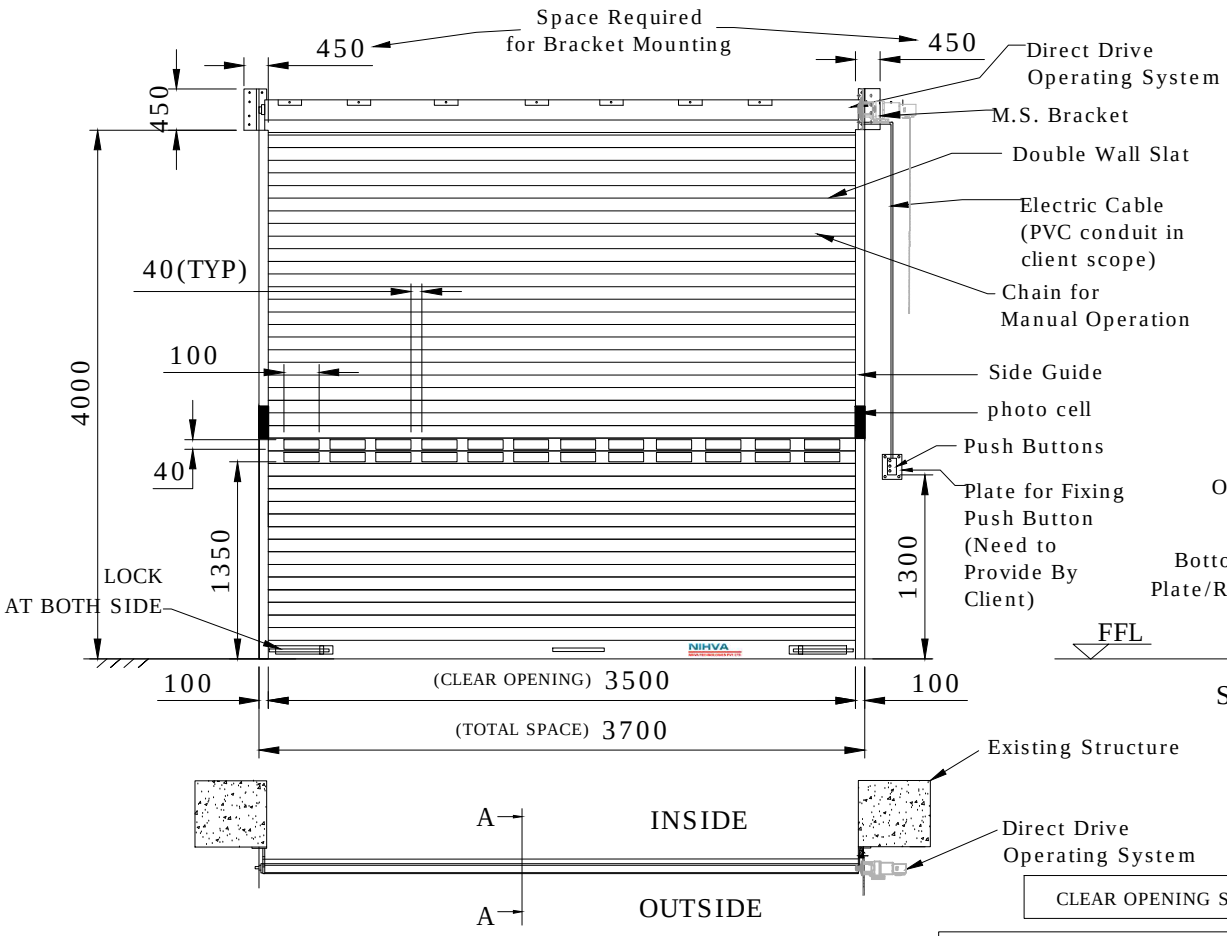


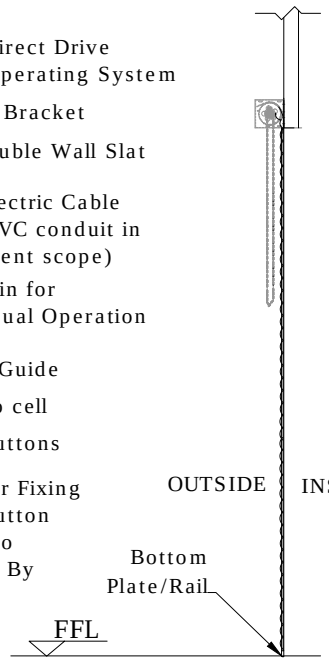

Section A-A

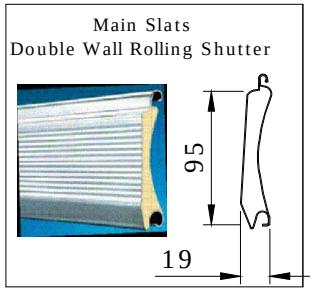

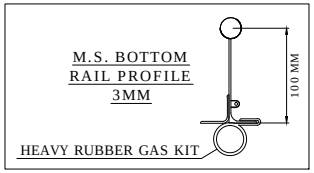

as per standard:
EN12424 -wind resistant-100km/hr
EN13241-Thermal Insulation U=3.9w/m2k
En 717-1-Acoustic Insulation R=16dB

CLEAR OPENING SIZE :- 3500mm x 4000mm = 2 NOS	COLOUR: Off White

NOTE: push button fixing will be decided as per site ready condition.

Sr. No.	Details	Specification
1)	Slats Profile	95mm x 19mm with PU filled inside
2)	Guide Channel	100mm x 40mm
3)	Shaft	125mm OD with heavy duty flanges and hardware
4)	Bottom Rail	125mm x3mm thick with extra angle support. Locking arrangement provides
5)	Brackets	450mmx450mmx3mm thickness

TITLE:

DOUBLE WALL
ROLLING SHUTTER

CLIENT APPROVAL

This drawing & designing is the property of NIHVA TECHNOLOGIES. Not be sold or copy to any other concern.

ALL DIMENSION ARE IN mm

	SIGN	DATE
DRAWN	P.V.A	18.07.19
CHECK	V.M.T	18.07.19
REV.	00	
APPRD.		
MFG		
Ref. No.		

NIHVA TECHNOLOGY PVT. LTD. PUNE
Tel : 020 66304033
Email:- info@nihva.com
Website:- www.nihva.com

CLIENT - LM WIND POWER BLADES

PROJECT -

SITE LOCATION - DABASPETH, BANGLORE.

DWG. NO. -NIHVA/19-20/0056

SCALE: NTS | WT: | SHEET: 01 OF 01

If any queries contact : projects@nihva.com