


DWG.NO: SALT_1729_GA_01_R0

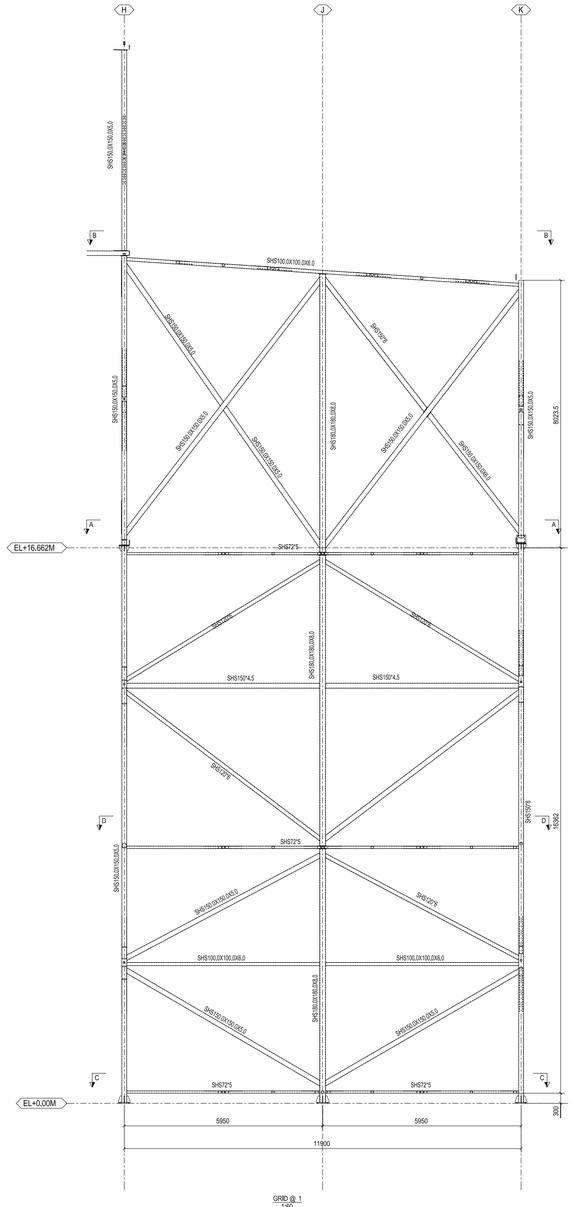


GRID @ 1
1:60

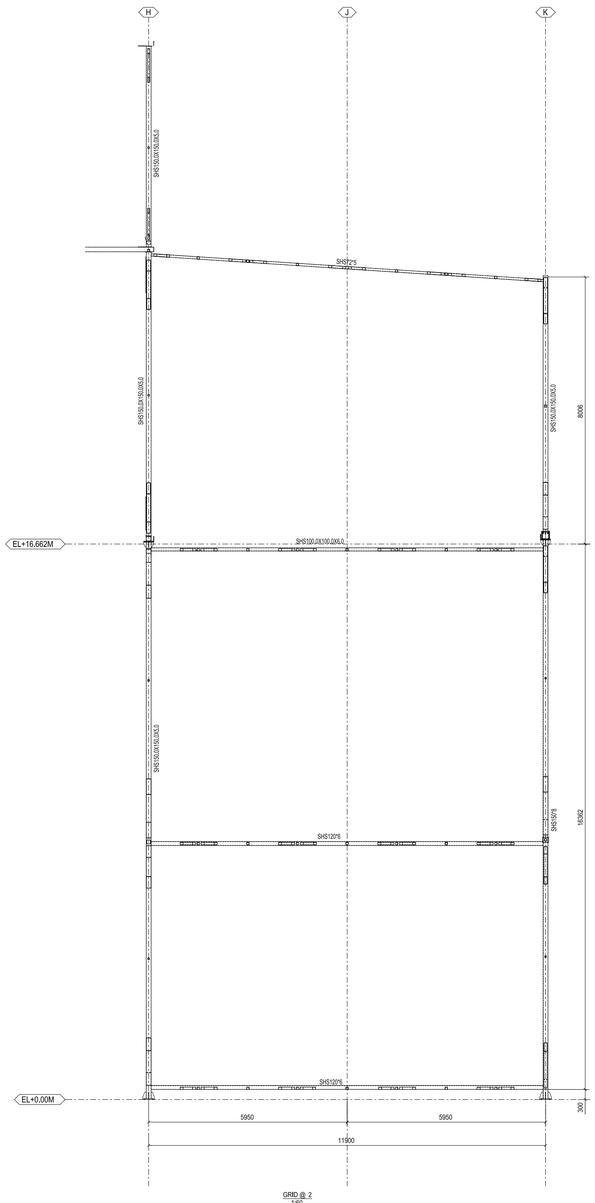


GRID @ 2
1:60

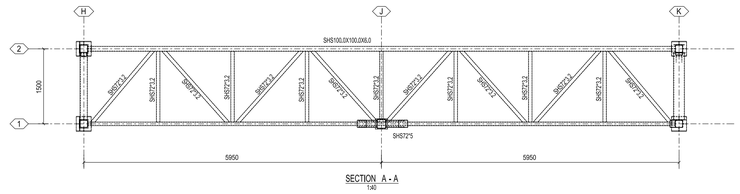


SECTION A - A
1:40

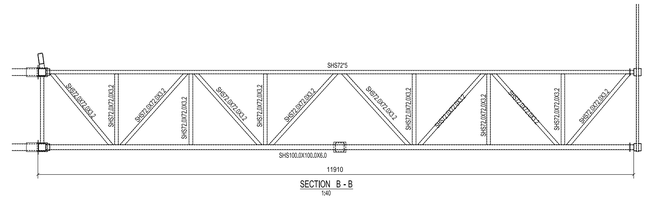

SECTION B - B
1:40

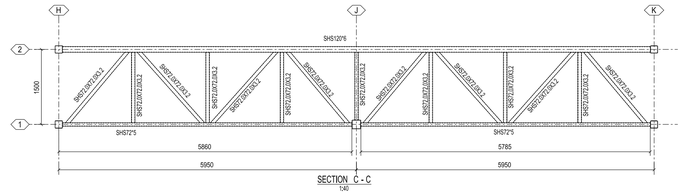

SECTION C - C
1:40

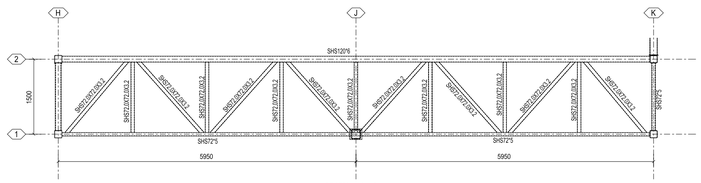

SECTION D - D
1:40

0	GA DRAWING FOR APPROVAL	05.11.22	MEGHA	HAB	HAB
REV.NO.	DESCRIPTION.	REV.DATE	DRAWN.	CHKD.	APPD.

DWG.TITLE :-	GA DRAWING FOR DOOR FRAME TRUSS BETWEEN 84M & 99M
PROJECT	MEGADOOR INSTALLATION AT HYDRABAD AIRPORT
CLIENT	GMR

SALT Design Services
NIHVA TECHNOLOGIES PVT LTD

SALT DESIGN SERVICES

NIHVA TECHNOLOGIES PVT. LTD. PUNE
Tel : 020 66304033
Email:- info@nihva.com
Website:- www.nihva.com

DRAWN :RRK	CHECKED : HAB	SCALE: 1:100
APPROVED : HAB	JOB CODE. : 1729	DATE: 05.11.2022
DWG.NO: SALT_1729_GA_01_R0	(SH-1OF1)	REV. - R0
		SIZE. - A0

A1 [841 x 594]