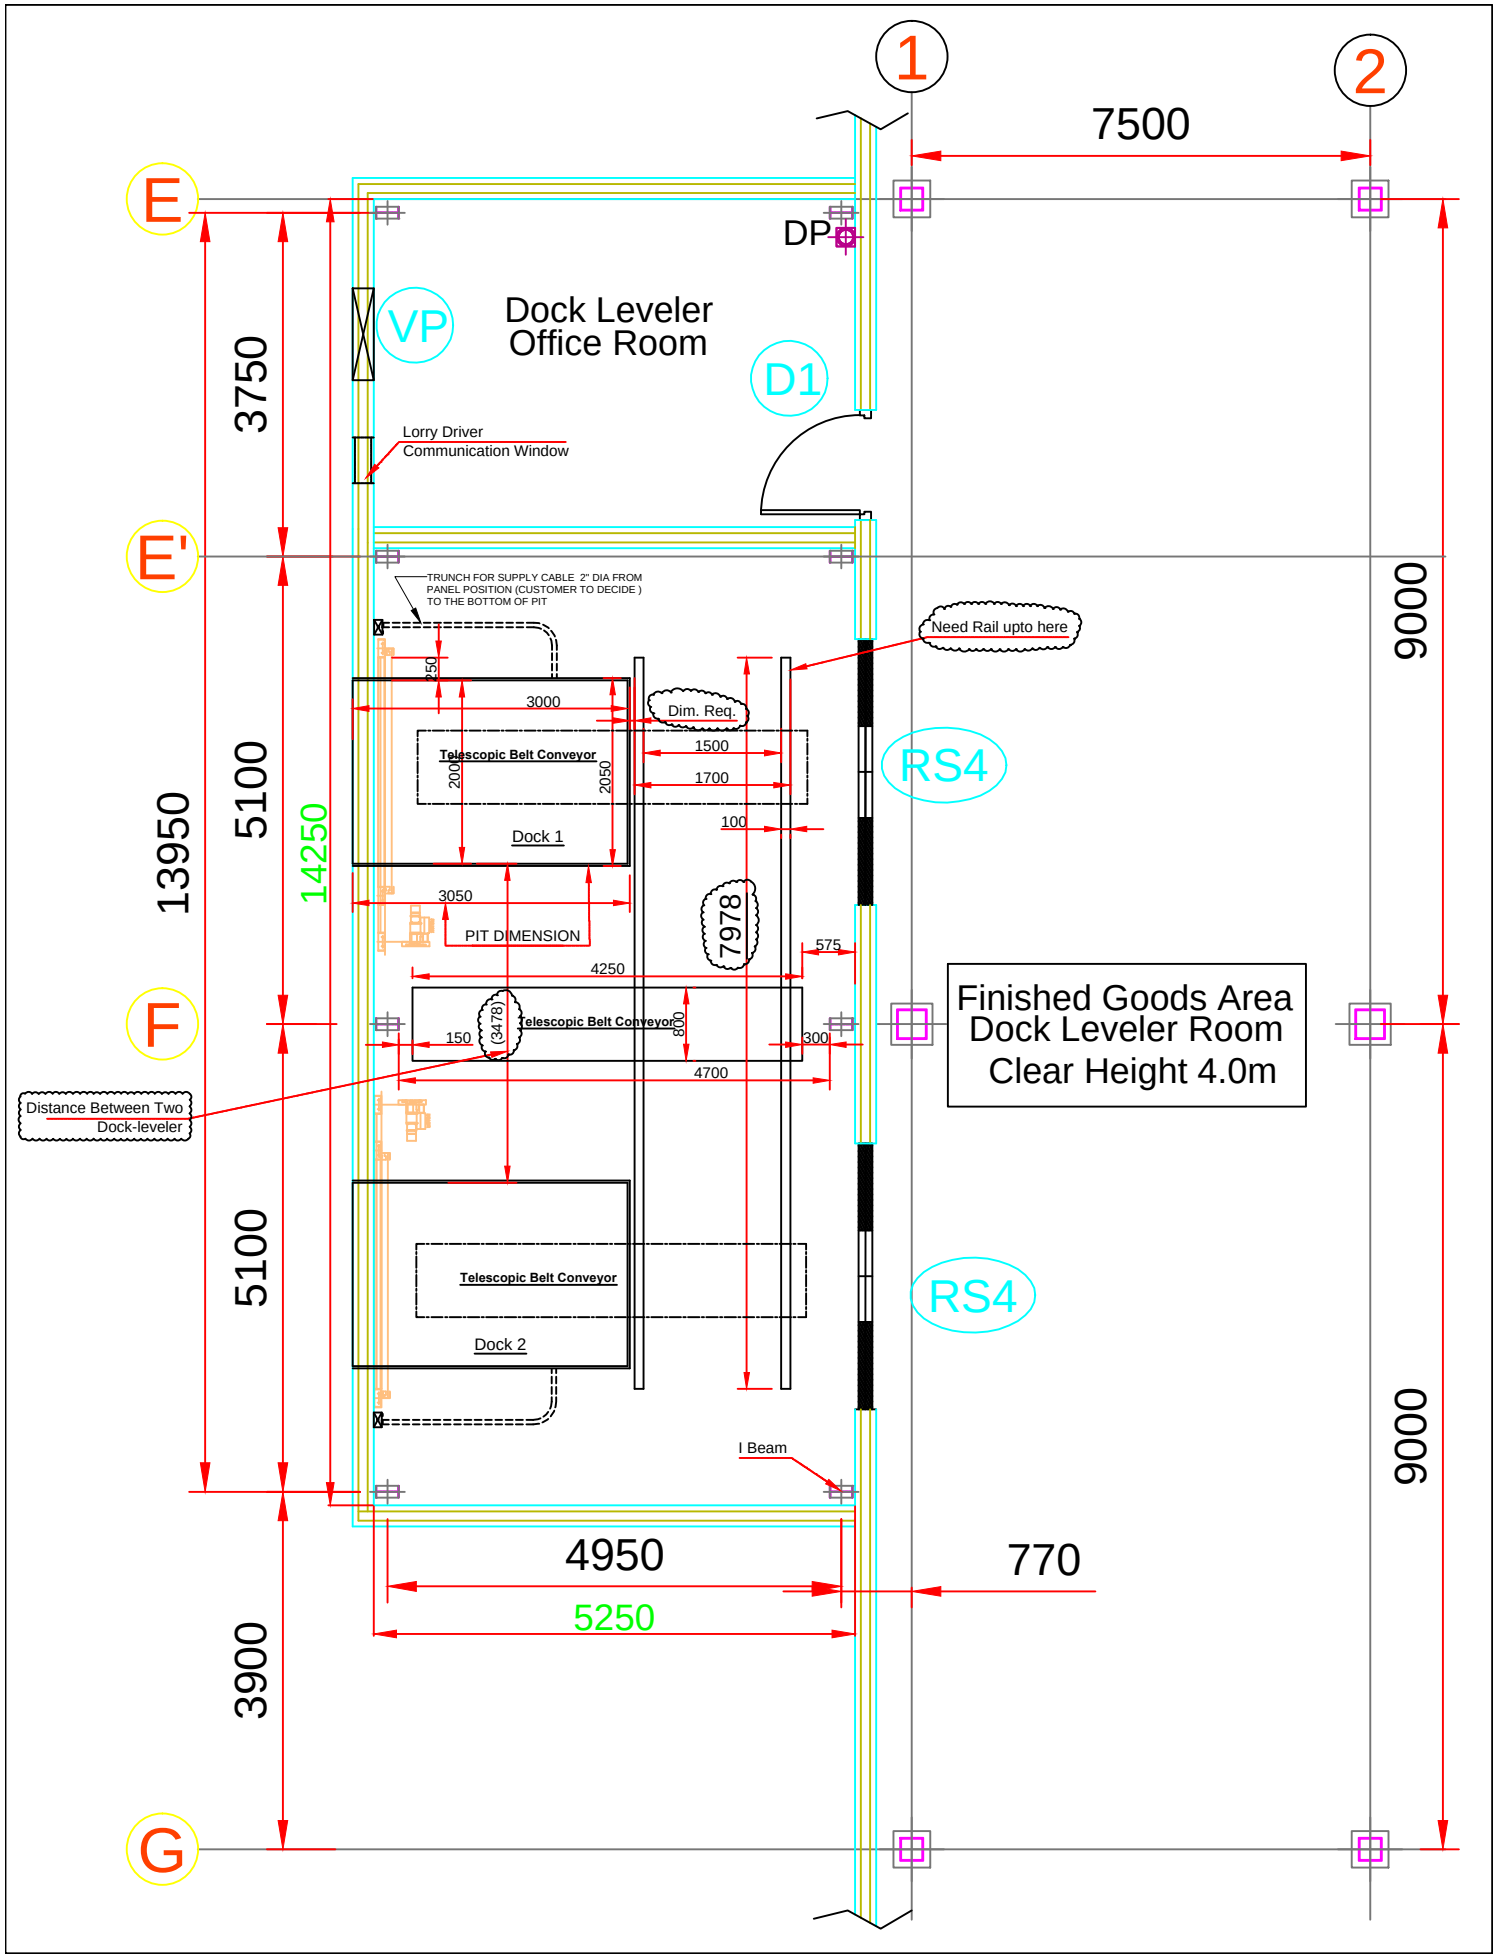

1
2
7500
E
E'
F
G
DP
VP
Dock Leveler
Office Room
D1
Lorry Driver
Communication Window
TRUNCH FOR SUPPLY CABLE 2" DIA FROM
PANEL POSITION (CUSTOMER TO DECIDE )
TO THE BOTTOM OF PIT
Need Rail upto here
250
3000
Dim. Req.
1500
1700
100
Telescopic Belt Conveyor
200
2050
Dock 1
RS4
3050
PIT DIMENSION
7978
575
4250
Telescopic Belt Conveyor
(3478)
800
150
300
4700
Distance Between Two
Dock-leveler
Finished Goods Area
Dock Leveler Room
Clear Height 4.0m
Telescopic Belt Conveyor
Dock 2
RS4
I Beam
3750
5100
13950
14250
5100
3900
9000
9000
4950
5250
770