
BOOM BARRIER LAYOUT WITH WIRING DIAGRAM


NOTE :
All wires and electrical conduit/tray coordinated with electrical vendor


TECHNICAL DETAILS – UP 8E	
POWER SUPPLY	230V AC – 50/60 Hz
OPENING TIME	5÷8 s/90°
CURRENT	1.5 A
DEGREE OF PROTECTION	IP 45
MOTOR DIMENSION	450(W) x 380(D) x 1000(H) mm
CONTROL PANEL	E1A

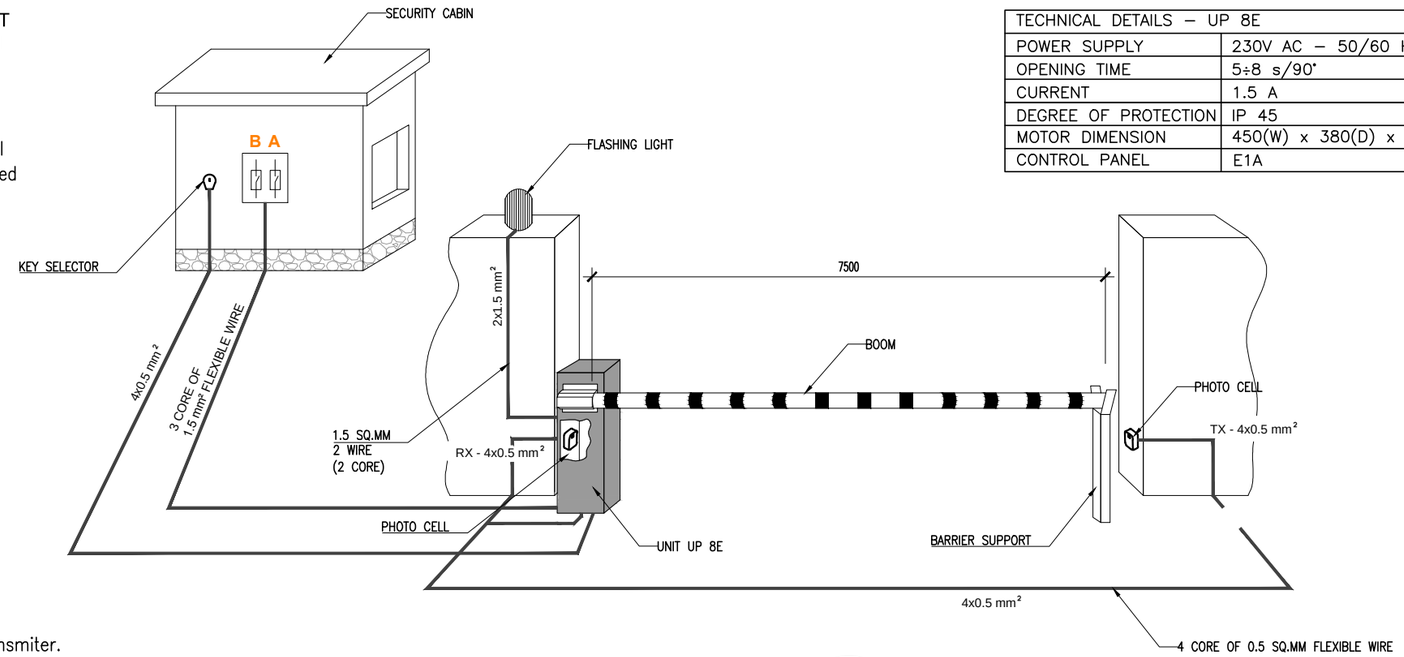

TX : Photocell transmiter.
RX : Photocell receiver.
A : 10 AMP S/P MCB
B : 10 AMP S/P MCB for provision to connect any other safety devices (voltage stabilizer / emergency UPS).


BOOM BARRIER FOUNDATION

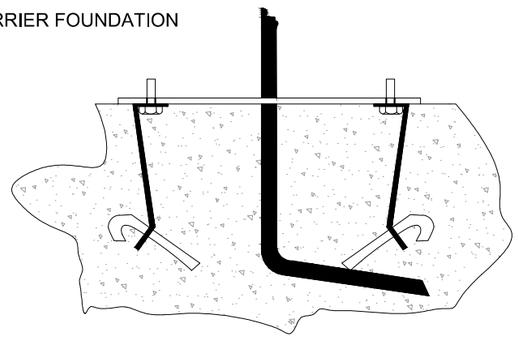

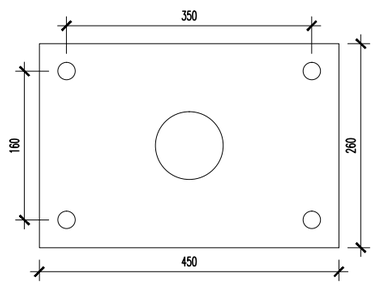

LAY A CONCRETE FOUNDATION WITH BURIED ANCHORING BRACKETS AND THE BASE PLATE, MAKING SURE THAT IT IS PERFECTLY LEVEL AND SMOOTH. INSERT APPROPRIATE ELEMENTS IN IRON OR ANY OTHER SUITABLE MATERIAL INTO THE HOLES OF THE ANCHORING HOOKS SO AS TO PERMIT FIXING TO THE CONCRETE REINFORCEMENT. ROUTE THE CABLE DUCTS THROUGH THE CENTRAL HOLE OF THE PLATE.
ATTENTION : ENSURE THAT ACHORING IS STURDY AND STABLE.

KEY PLAN :-

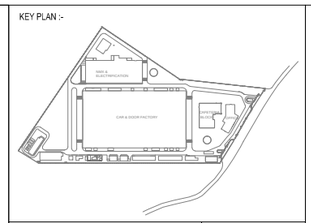

N

GENERAL NOTES :
- ALL DIMENSIONS ARE IN MILLIMETRES AND ARE UNFINISHED DIMENSIONS UNLESS OTHERWISE SPECIFIED.
- ALL LEVELS ARE IN METRES AND ARE UNFINISHED LEVELS UNLESS OTHERWISE SPECIFIED.
- DO NOT SCALE DRAWINGS. ONLY WRITTEN DIMENSIONS SHALL BE FOLLOWED. ANY DISCREPANCIES NOTED SHALL BE BROUGHT TO THE NOTICE OF THE ARCHITECT PRIOR TO EXECUTION.

REV.	DESCRIPTION	DATE	BY	CHD.
T2	ISSUED FOR TENDER	02.03.17	SV	VA
T1a	ISSUED FOR CLIENT REVIEW	24.11.16	SV	VA
T1	ISSUED FOR TENDER	01.04.15	MB	VA

AMENDMENT

GRAPHIC SCALE: 0 1M 4M 8M / 1M 2M 6M 10M

CLIENT:
KONE ELEVATOR INDIA PVT. LTD.

PROJECT:
PROPOSED KONE ELEVATOR FACTORY AT PILLAIPAKKAM, NEAR CHENNAI.

DRAWING TITLE:
STANDARD DETAILS - 05
BOOM BARRIER DETAIL TYPE - 02

SCALE : AS SHOWN	DRAWN : V.A.	REV
DATE : 18.02.2015	CHKD : V.R.	
DRAWING NO: KEIPL-P-FAC-AR20-05-01-189949		T2

ARCHITECTURE • INTERIOR DESIGN • ENGINEERING • PLANNING • CONSTRUCTION MANAGEMENT
C R NARAYANA RAO
10, KARPAGAMBAL NAGAR, MYLAPORE, CHENNAI-600 004
B.Arch. (Hons.), M.Arch., (Calif.), F.I.I.A., Intl.Assoc.A.I.A., Registered Architect.