



ELEVATION FOR ENTRANCE GATE
SCALE 1:40

OUT SIDE

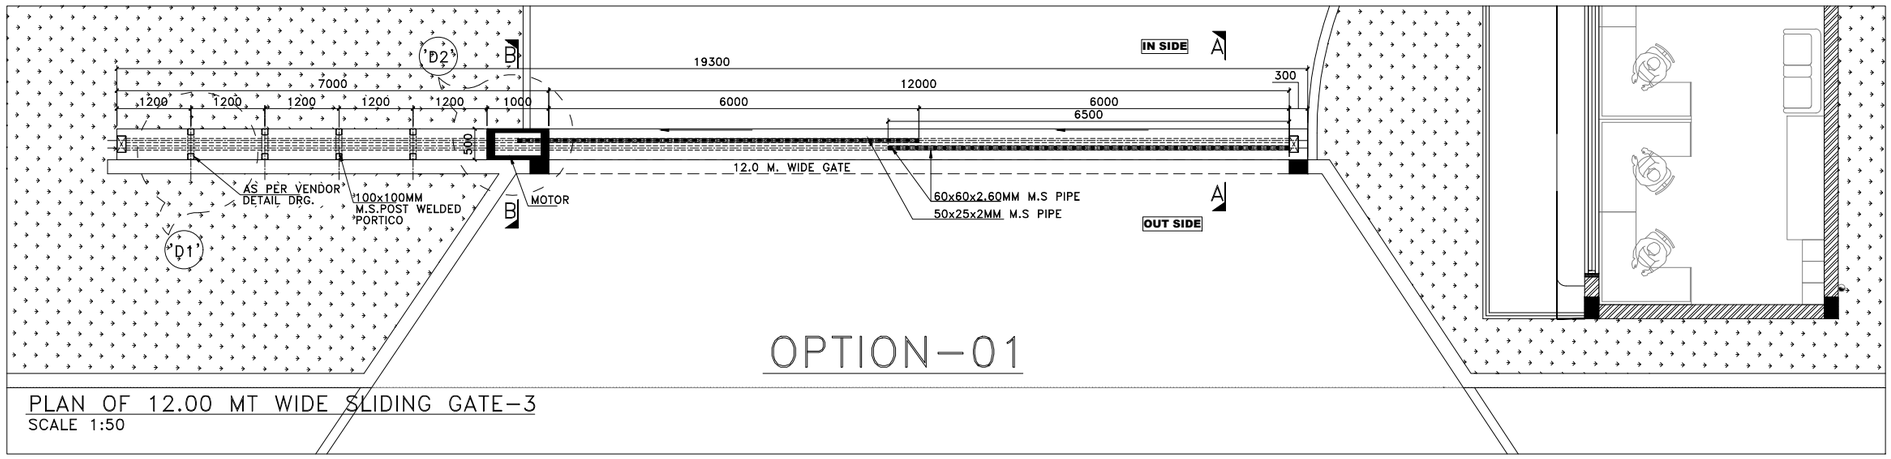

OPTION–01


PLAN OF 12.00 MT WIDE SLIDING GATE–3
SCALE 1:50

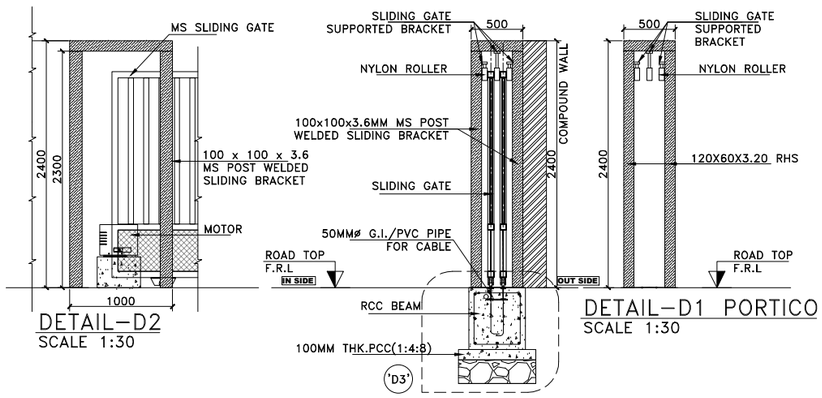


DETAIL–D2
SCALE 1:30

SECTION–B–B
SCALE 1:30


DETAIL–D1 PORTICO
SCALE 1:30

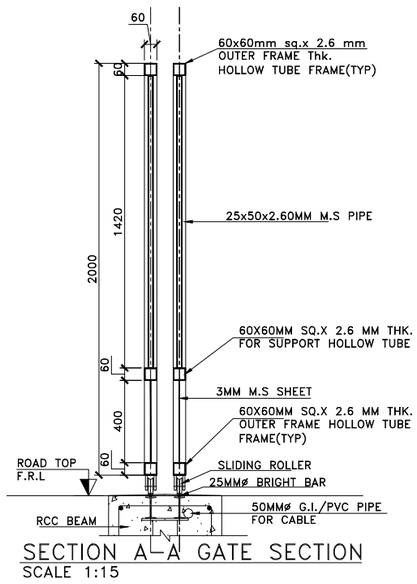


SECTION A–A GATE SECTION
SCALE 1:15

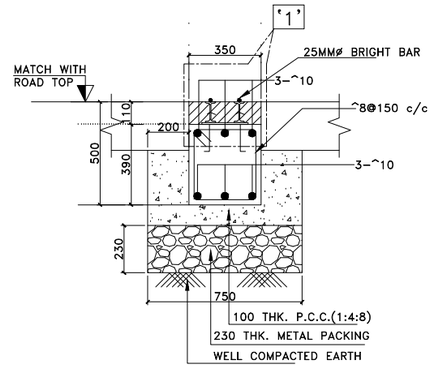

DETAIL–3 RCC BEAM
SCALE 1:15

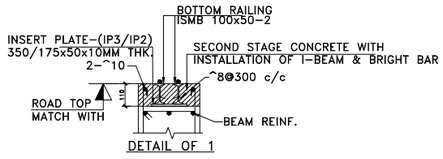

DETAIL OF 1

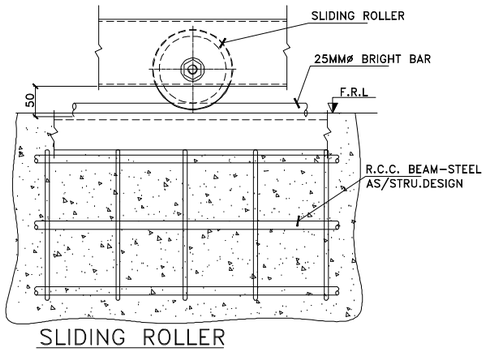

SLIDING ROLLER
SCALE 1:25

REFERENCE DRAWINGS

SR.NO.	DRAWING TITLE	DRAWING NO.
01	SITE LAYOUT	2331-GEN-A01-SH1-A01-R8

NOTE :-

1. DO NOT SCALE THE DRAWING. REFER TO WRITTEN DIMENSIONS ONLY. ALL MEASUREMENTS MUST BE CHECKED AND VERIFIED AT SITE. ANY DISCREPANCY FOUND,TO BE NOTIFIED TO THE CONSULTING ENGINEER BEFORE EXECUTION.
2. ALL DIMENSIONS ARE IN MM.& ALL LEVELS ARE IN METERS UNLESS OTHERWISE SPECIFIED.
3. F.G.L & F.R.L AS PER SITE ROAD LAYOUT PLAN.


ABBREVATION :-

N.G.L	= FINISHED GROUND LEVEL
F.G.L.	= FINISHED GROUND LEVEL
F.R.L.	= FINISHED ROAD LEVEL
F.F.L.	= FINISHED FLOOR LEVEL
T.O.C.	= TOP OF CONCRETE
T.O.W.	= TOP OF WALL
B.O.C.	= BOTTOM OF CONCRETE.
P.S.	= PLUMBING SHAFT
U.S.	= UTILITY SHAFT
D.B.	= DISTRIBUTION BOX

LEGEND :-

- 230MM THK. BRICK MASONRY WALL
- 115MM THK. BRICK MASONRY PARTITION WALL
- 200MM / 100MM THK. AAC / CONC. BLOCK MASONRY WALL
- PLATFORM AT TERRACE FFL. LVL. 150MM HIGH
- HOLD
- REVISION

KEY - PLAN :

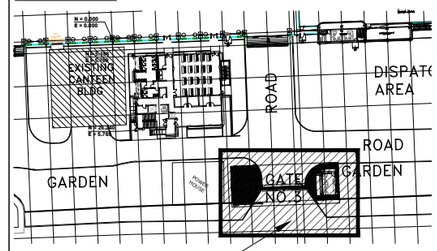

GATE- 03

F.F.L = (+) 0.00 = (+) 0.00

REV.	DATE	DESCRIPTION	DRN.	CHK	APP	PRN.
R0	16-06-25	ISSUED FOR APPROVAL	DEVANG	AMITA	GJT	EMAIL

ISSUED FOR

☐ INFORMATION ☑ APPROVAL ☐ CONSTRUCTION
☐ ENQUIRY ☐ ORDER ☐ REVIEW

CLIENT : **C G POWER & INDUSTRIAL SOLUTION LTD. AT BHOPAL**

PROJECT : PROPOSED 35000 MVA PROJECT

CONSULTANT : SHAH & TALATI Design & Engineering

9th FLOOR, KIRTI TOWER, TILAK ROAD, VADODARA-390001, GUJARAT, INDIA.
PHONE : +91-265-2440701 / 2440726
E-MAIL : design@shahntalati.com
WEBSITE : www.shahntalati.com

PROJECT NO. :-	TITLE :-
2331	**PLAN , ELEVATION & DETAIL OF SLIDING GATE-3**

DRAWN BY	DEVANG		R0 16 06 25
CHECKED BY	AMITA		
APPROVED BY	GJT		
DRAWING NO.	**2331-GATE-A01-SH1-A1-R0**		SHEET 1 OF 2
SCALE :AS SHOWN			

THIS DOCUMENT OR DRAWING IS THE PROPERTY OF SHAH & TALATI CONSULTING ENGINEERS AND SHALL NOT, UNDER ANY CIRCUMSTANCES, BE TOTALLY OR PARTIALLY, DIRECTLY OR INDIRECTLY, TRANSFERRED, REPRODUCED, COPIED, DISCLOSED OR USED WITHOUT SHAH & TALATI'S PRIOR WRITTEN CONSENT.

A1