
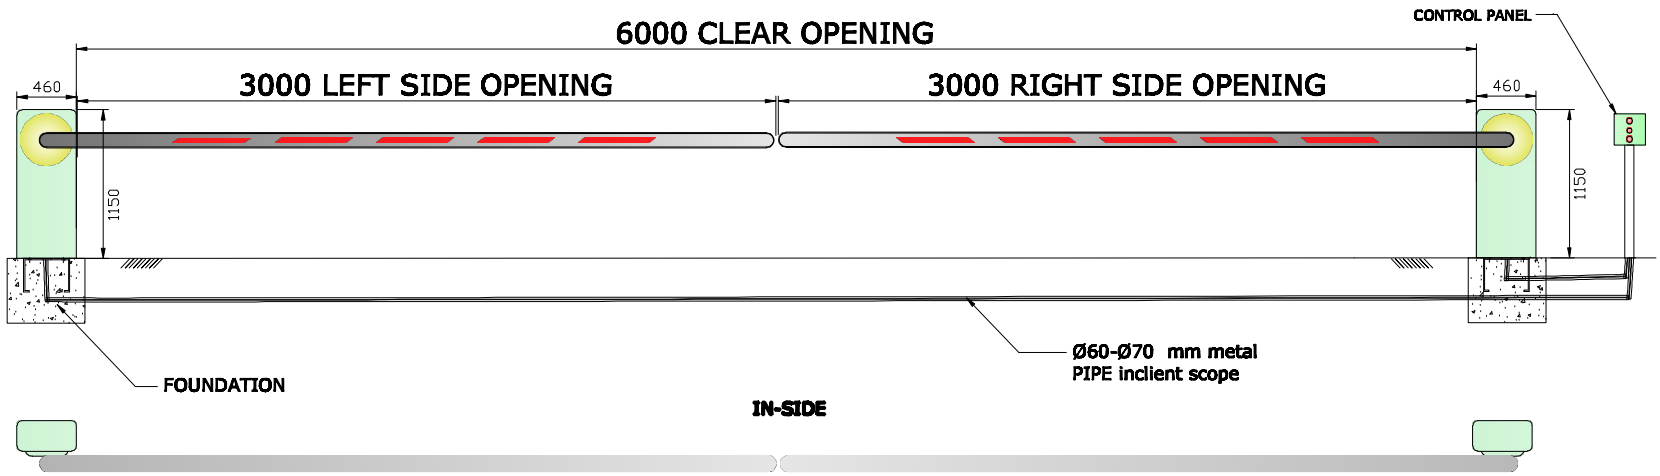


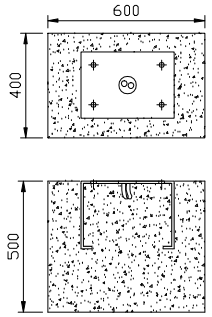

FOUNDATION DETAILS

This drawing & designing is the property of NIHVA TECHNOLOGIES. Not be sold or copy to any other concern.

TITLE

BOOM BARRIER FOUNDATION DETAILS

CLIENT APPROVAL

ALL DIMENSION ARE IN mm

	SIGN	DATE
DRAWN	ABHIJIT	08/01/15
CHECK	ANIL	08/01/15
ENG		
APPRD.		
MFG		
Ref. No.		

NIHVA TECHNOLOGIES PVT. LTD.

NIHVA TECHNOLOGY PVT. LTD. PUNE
Tel : 020 66304033
Email:- info@nihva.com
Website:- www.nihva.com

CLIENT -MAHINDRA ROYAL CITY

PROJECT -

SITE -PIMPRI

DWG. NO. - NVA/MRC/BRR/01

SCALE:01 | WT: | SHEET:01

If any queries contact : projects@nihva.com