



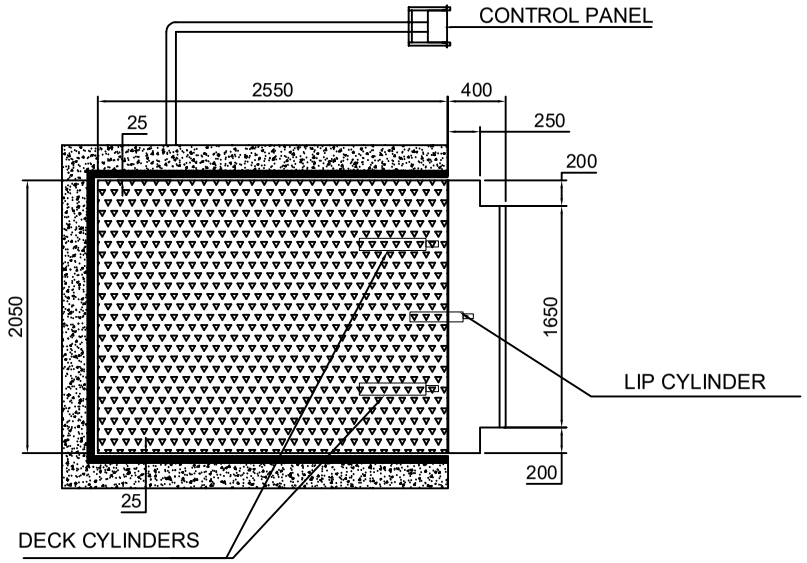


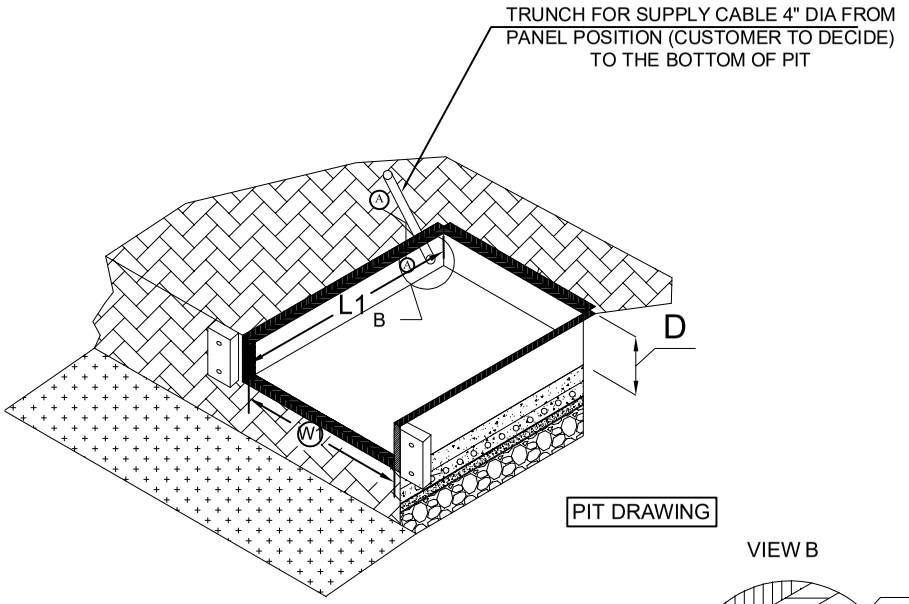

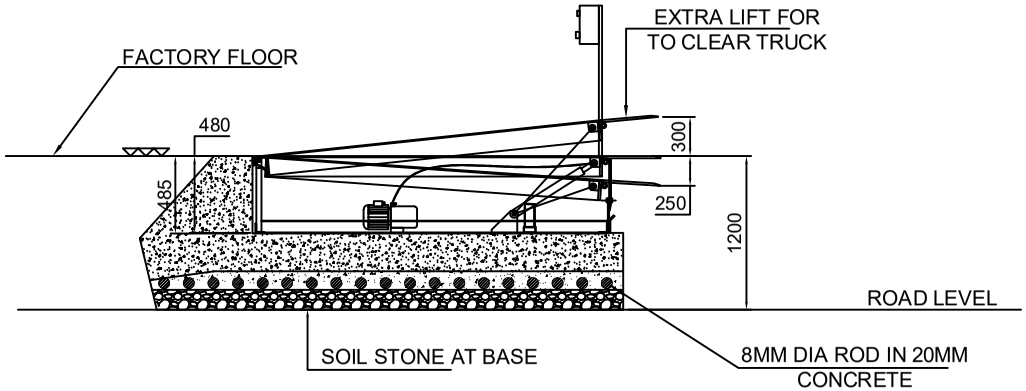

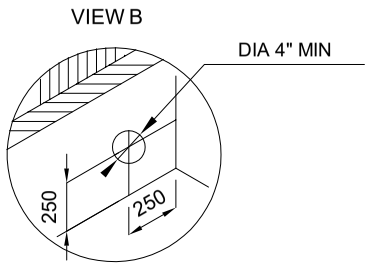

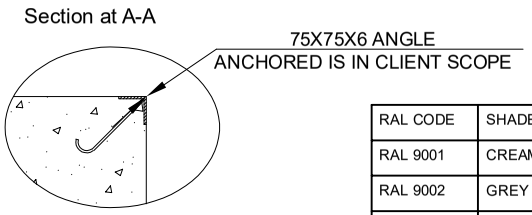

DOCK LEVELER SIZE	WIDTH (W)	LENGTH (L)	HEIGHT (H)	LIP (C) LENGTH
	2050	2550	480	400
PIT DIMENSION	WIDTH (W 1)	LENGTH (L 1)	DEPTH (D)	
DL	2100	2560	485	

Capacity:- 9MT

RAL CODE	SHADE	COLOUR
RAL 9001	CREAM	
RAL 9002	GREY WHITE	
RAL 9010	PURE WHITE	
RAL 5002	ULTRAMARINE BLUE	
RAL 7035	LIGHT GREY	
RAL 7001	SILVER GREY	

NOTE: -
1. PROPER DRAINAGE SHOULD BE DONE
2. TRENCH AS SHOWN SHOULD BE MADE BY DECIDING THE POWER PACK POSITION.
3. LEVEL OF THE PIT SHOULD BE PLAIN AND SHOULD TAKE AT LEAST 15000 KG FLOOR LOADING
4. FABRICATION TOLERANCE FOR PLATFROM SIZE WILL BE ± 20 MM.
5. PIT,DUCT FOR HOSES & ALL CIVIL WORK IN CLIENT SCOPE
6.SURFACE FINISH: APPROVED RAL CODE.

Rev No.	Revision	Date	Revised By

This drawing & design is the property of NIHVA TECHNOLOGIES. Not to be sold or copied to any other concern.

TITLE:- DOCK LEVELER GA DRAWING

	NAME	DATE	SIGN
DRAWN	SUJATA	14/04/2022	
CHECK	P.JAIN	14/04/2022	
APPRD.	M.SUTAR	14/04/2022	

NIHVA TECHNOLOGIES PVT. LTD.
NIHVA TECHNOLOGIES PVT. LTD. PUNE
Tel : 020 66304033
Email:- info@nihva.com
Website:- www.nihva.com

CLIENT - Abhi Buildcon
LOCATION - Pune
PRODUCT - Dock Leveler
If any queries contact : design@nihva.com
DWG NO:-NIHVA/22-23/CLT/0013 REV- 0
ALL DIMENSION ARE IN mm
SCALE: NTS SCALE:-- 1:1 SHEET: 01 OF 01