
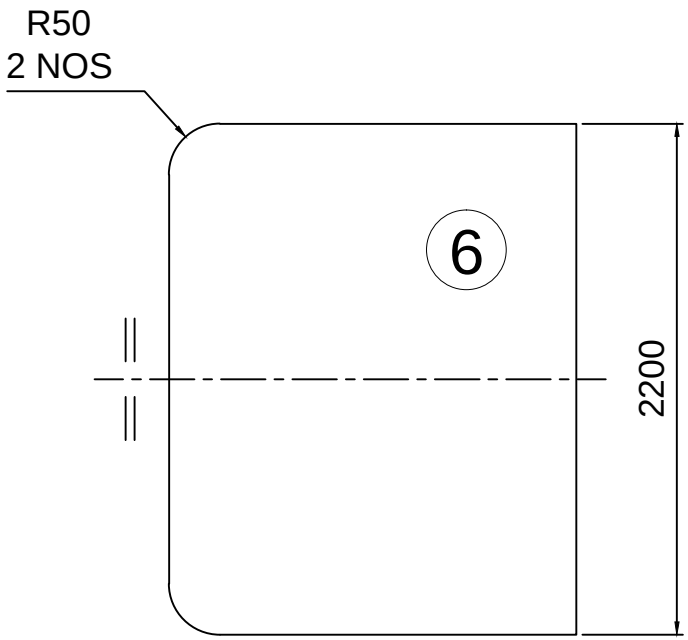


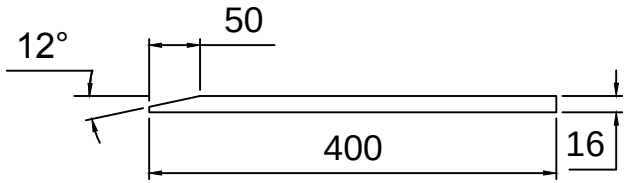

M.S LIP PLATE

400 X 16 X 2200L = 1 NO

This drawing & design is the property of NIHVA TECHNOLOGIES. Not to be sold or copied to any other concern.

TITLE			
LIP PLATE DRG			
	NAME	SIGN	DATE
DRAWN	PRADEEP		02.05.2018
CHECK	PRADEEP		02.05.2018
APPRD.	PRADEEP		02.05.2018
If any queries contact : design@nihva.com			
ALL DIMENSION ARE IN mm			

NIHVA
NIHVA TECHNOLOGIES PVT. LTD.
NIHVA TECHNOLOGIES PVT. LTD. PUNE
Tel : 020 66304033
Email:- info@nihva.com
Website:- www.nihva.com

CLIENT -

PROJECT - NDL 385 & 386

SITE LOCATION -

DWG. NO. : NIHVA/18-19/MFG/NDL385&386/008

SCALE: NTS | WT: | REV- 00