


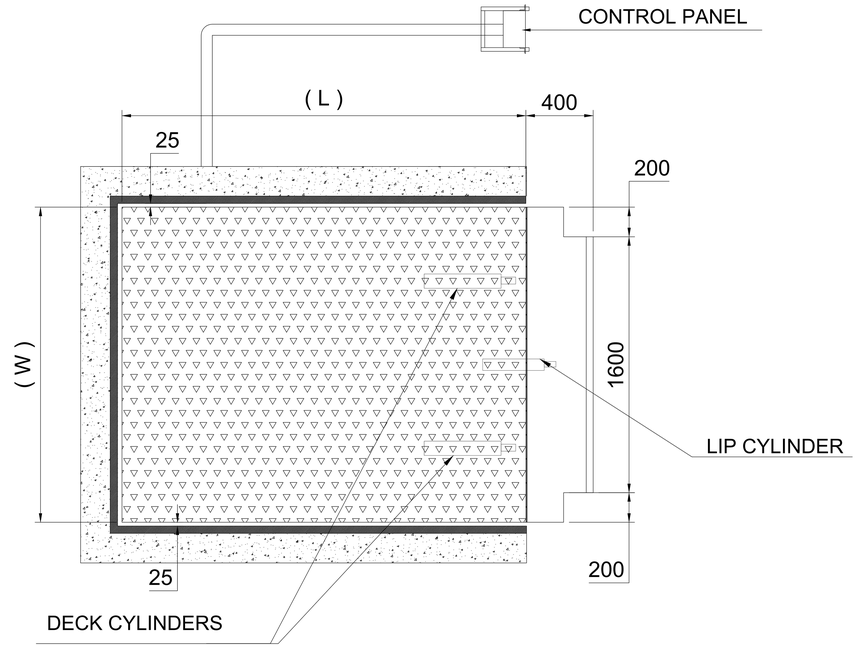


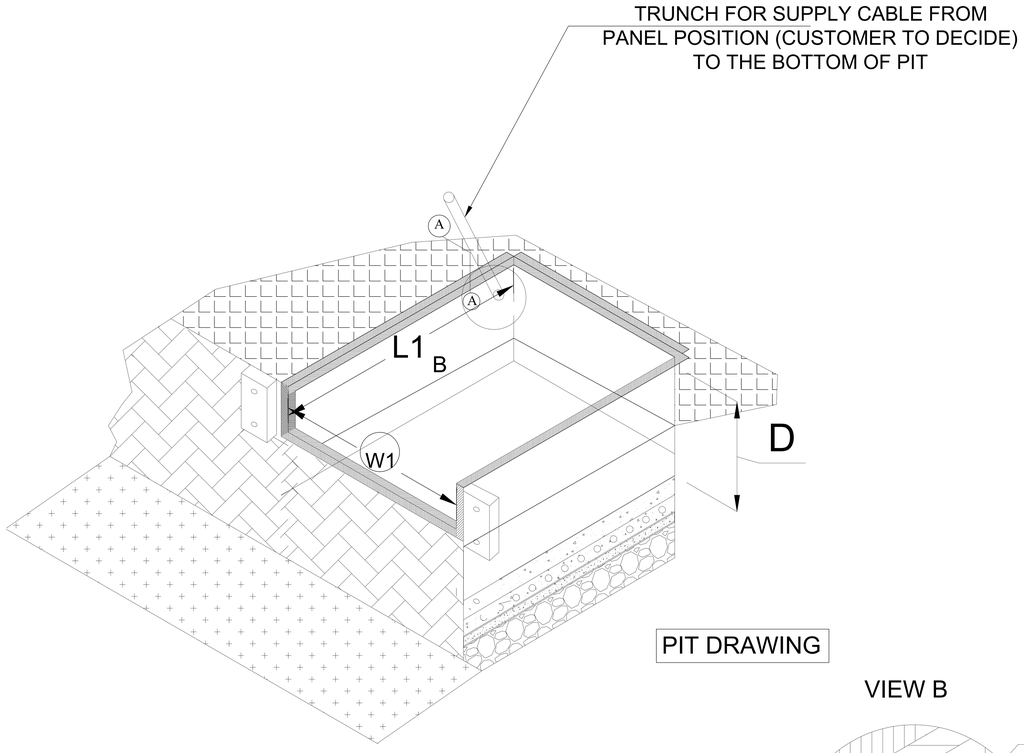


PIT DRAWING

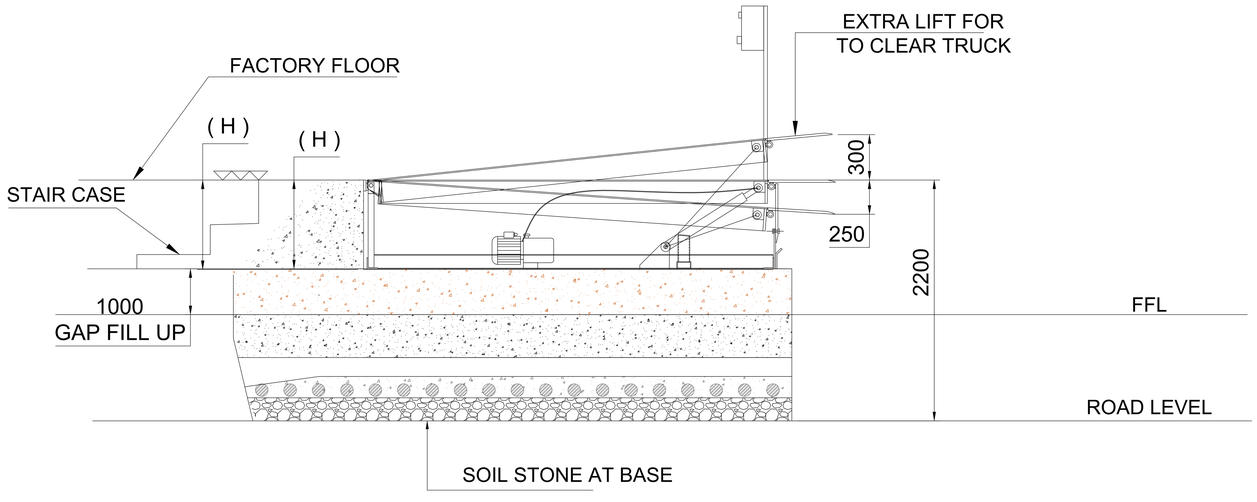

VIEW B

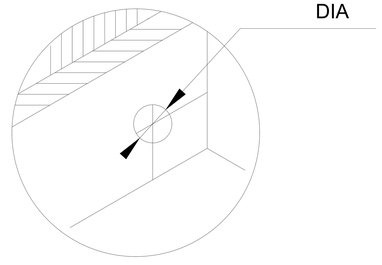

Section at A-A

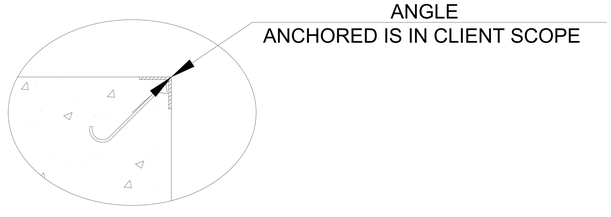

DOCK LEVELER SIZE	WIDTH (W)	LENGTH (L)	HEIGHT (H)	LIP (C) LENGTH
	2000	2500	480	400
PIT DIMENSION	WIDTH (W1)	LENGTH (L1)	DEPTH (D)	
DL	2050	2550	1485	

Capacity:-6 TON

NOTE:-

1. ALL DIMENSIONS ARE IN MM
4. THES DRAWING IS FOR UNDERSTANDING PURPOSE
3. PIT,DUCT FOR HOSES & ALL CIVIL WORK IN CLIENT SCOPE

SR.NO	DESCRIPTION	REV.NO	REV.DATE	REV.BY
01.	Pit depth 485 mm to 1485 mm	REV.01	20.10.2024	S.J.

This drawing & design is the property of NIHVA TECHNOLOGIES. Not to be sold or copied to any other concern.

TITLE:- DOCK LEVELER GA DRAWING

	NAME	DATE	SIGN
DRAWN	SUJATA	10.08.2023	
CHECK			
APPRD.	V.T	10.08.2023	

NIHVA TECHNOLOGIES PVT. LTD.
NIHVA TECHNOLOGIES PVT. LTD. PUNE
Tel : 020 66304033
Email:- info@nihva.com
Website:- www.nihva.com

CLIENT - BHOOMI AGRO BIO FOODS

LOCATION -

PRODUCT - DOCK LEVELER

If any queries contact : design@nihva.com

DWG NO:-NIHVA/22-23/CLT/0152XX REV- 01

ALL DIMENSION ARE IN mm

SCALE: NTS SCALE:-- 1:1 SHEET: 01 OF 01