

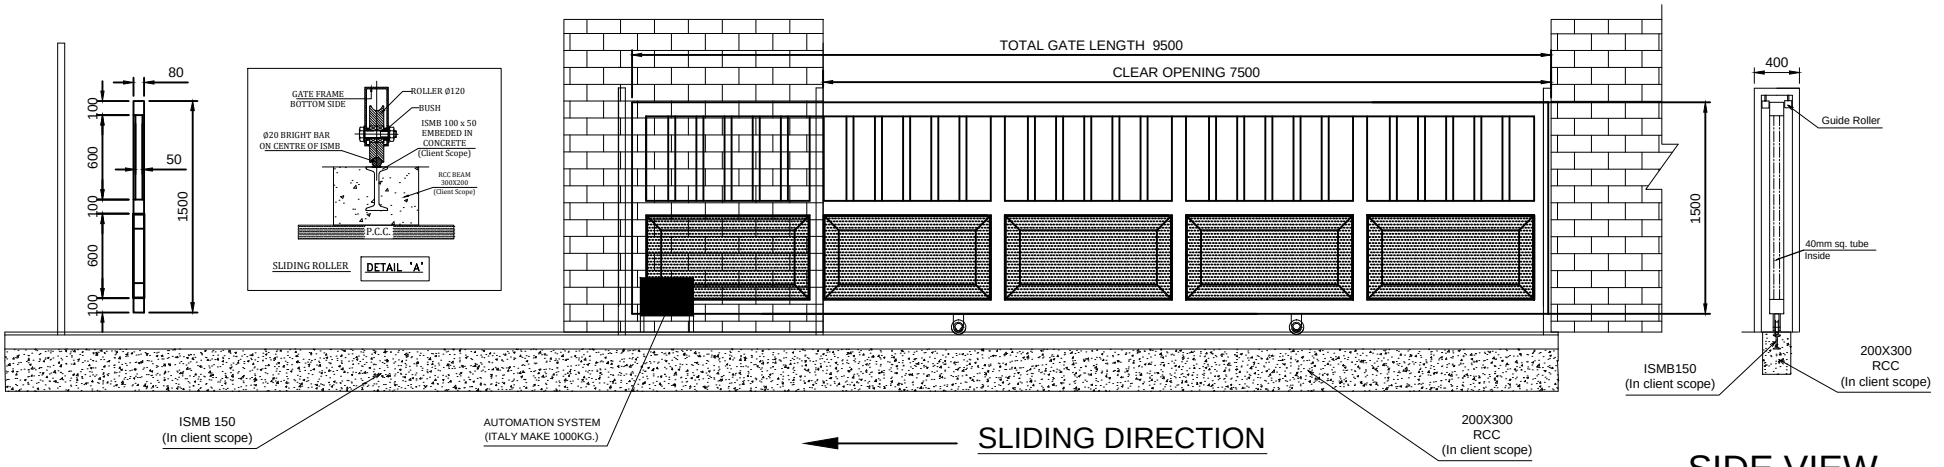


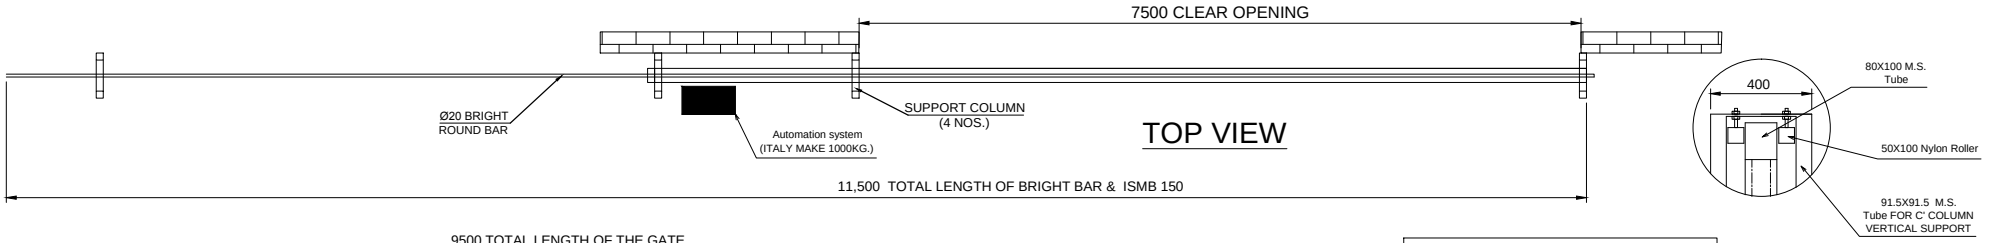

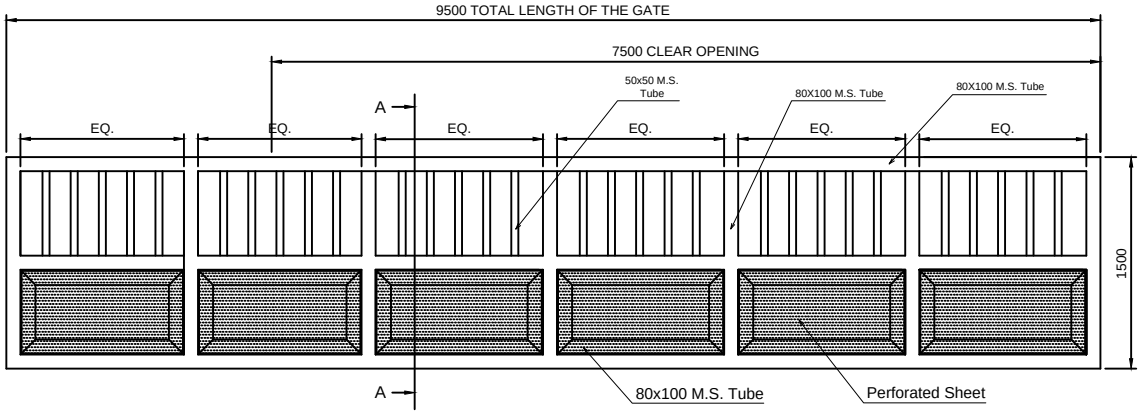

Clear Opening size - 7500X1500mm
Total length of gate - 9500X1500mm
No. Of Column - 4 nos.
Factory paint finish - Red oxide primer coat
NOTE :- *ALL REQ. CIVIL WORK WILL BE IN CLIENT SCOPE.

This drawing & designing is the property of NIHVA TECHNOLOGIES. Not be sold or copy to any other concern.

TITLE: MOTORIZED SLIDING GATE	NIHVA TECHNOLOGIES PVT. LTD.	NIHVA TECHNOLOGY PVT. LTD. PUNE Tel : 020 66304033 Email:- info@nihva.com Website:- www.nihva.com
	SIGN	DATE
DRAWN	ABHIJIT	09/10/15
CHECK	ANIL	09/10/15
REV.	01	
APPROVAL		
CLIENT - REWARD CONSTRUCTION		
PROJECT - GIVAUDAN		
SITE - RANJANGAON MIDC		
DWG. NO. : NIHVA/15-16/106		
If any queries contact : projects@nihva.com	SCALE: 01	WT: SHEET: 01 OF 01
ALL DIMENSION ARE IN mm		