




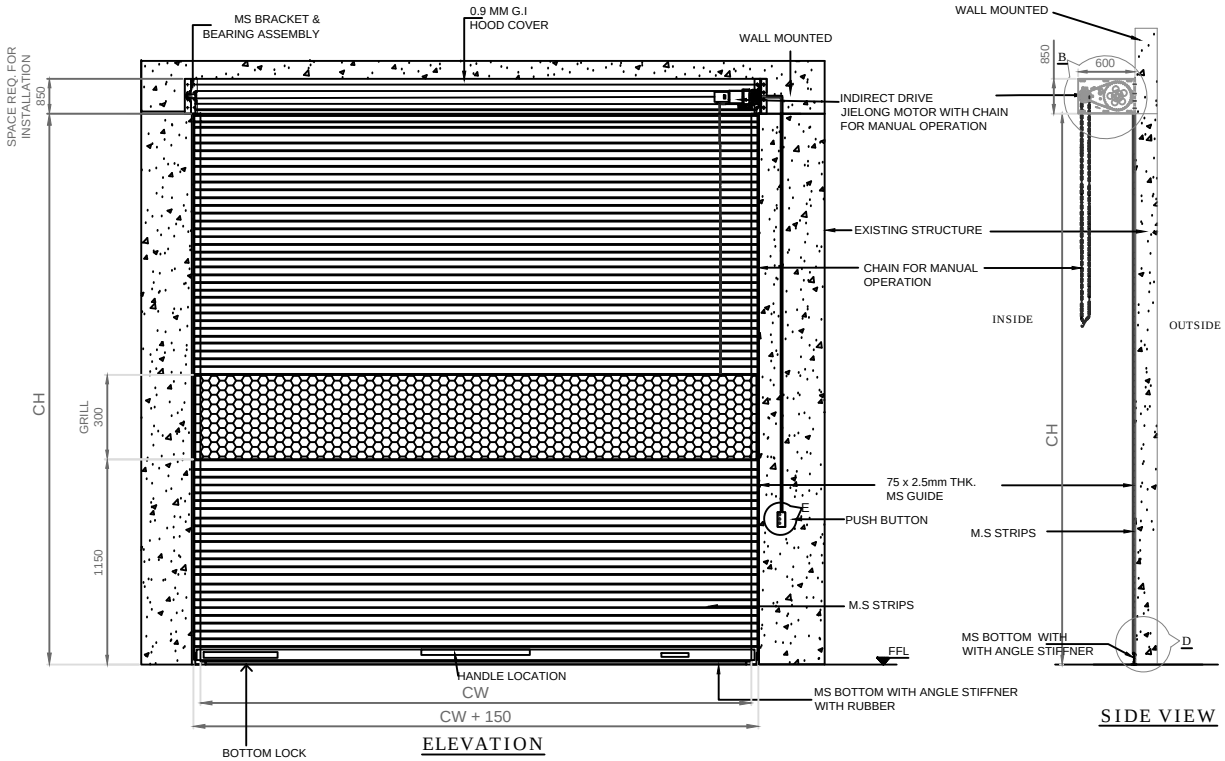


PLAN

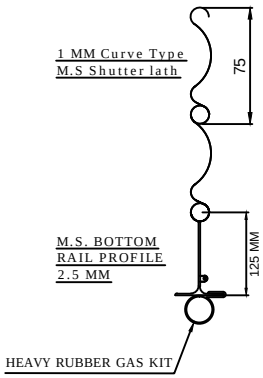


DETAILS : D

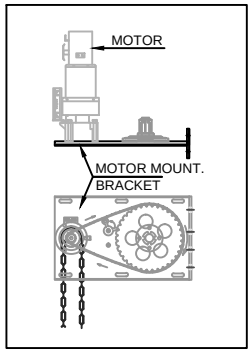


DETAILS : A & B

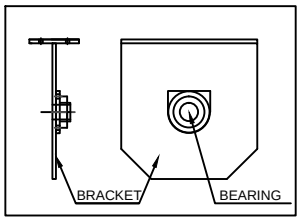


DETAILS : C

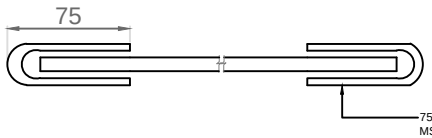

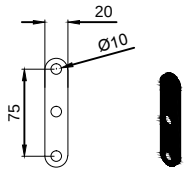

5 m m THK. LINK

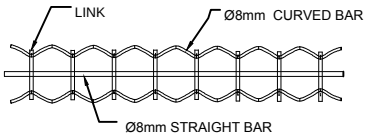

NOTE:
1. REQUIRED TECHNICAL STRUCTURE FOR SHUTTER IN CLIENT SCOPE.
2. TWO COATS OF PRIMER AND TWO COAST OF SYNTHETIC ENAMEL OR POWDER COATING.

2500	2000	2	RAL -
CLEAR WIDTH (CW)	CLEAR HEIGHT (CH)	QUANTITY	RAL COLOR POWER COATING

This drawing & design is the property of NIHVA TECHNOLOGIES. Not to be sold or copied to any other concern.

TITLE: MOTORIZED ROLLING SHUTTER

NIHVA TECHNOLOGIES PVT. LTD.

NIHVA TECHNOLOGIES PVT. LTD. PUNE
Tel : 020 66304033
Email:- info@nihva.com
Website:- www.nihva.com

	NAME	SIGN	DATE
DRAWN	P.A		20.07.2020
CHECK	G.J		20.07.2020
APPRD.			

CLIENT -HUHTAMAKI PPL LTD
PROJECT -
SITE LOCATION - KHOPOLI
If any queries contact : design@nihva.com
DWG. NO. : NIHVA/20-21/0034
REV- R00
ALL DIMENSION ARE IN mm
SCALE: NTS
WT:
SHEET: