
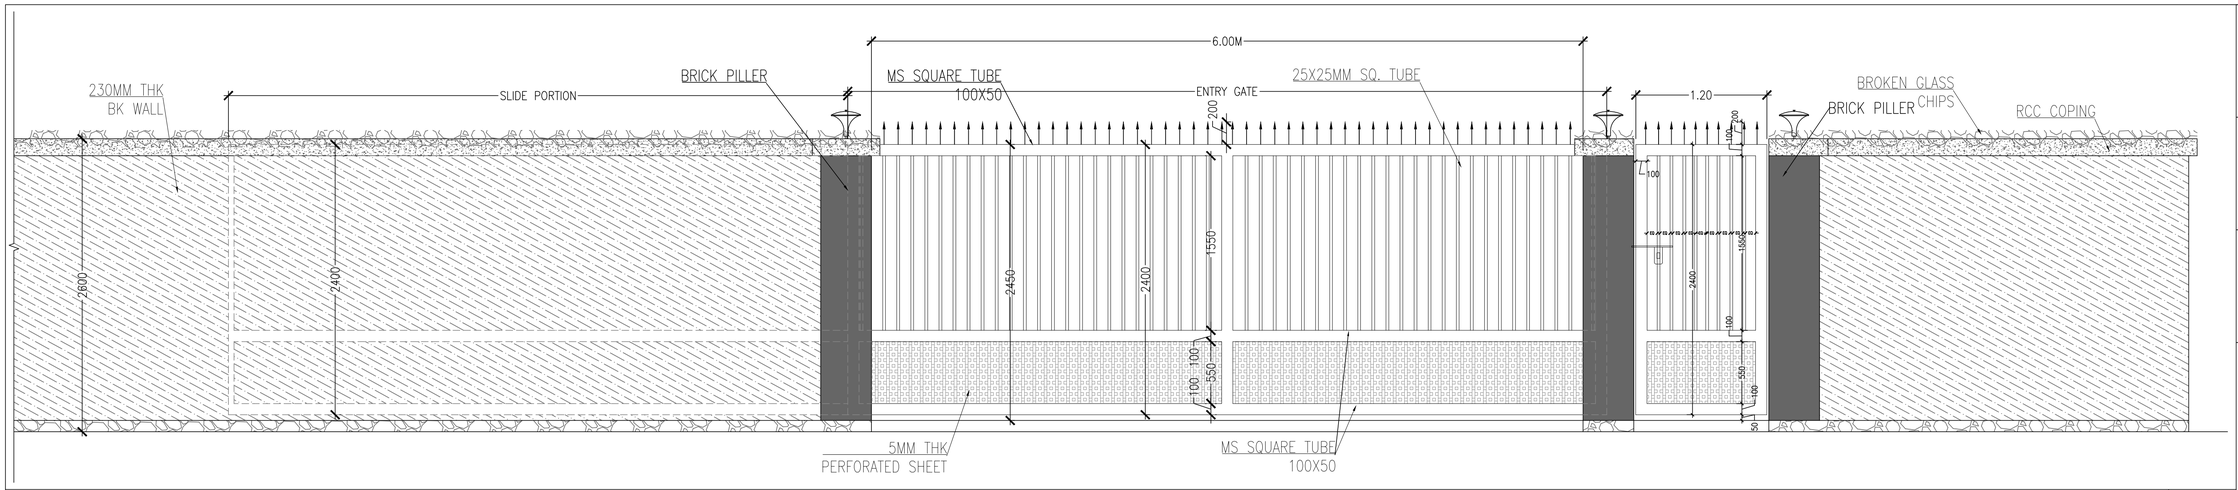



29 FRONT SIDE COMPOUND WALL ELEVATION (ENLARGE VIEW)

SCALE: 1:25

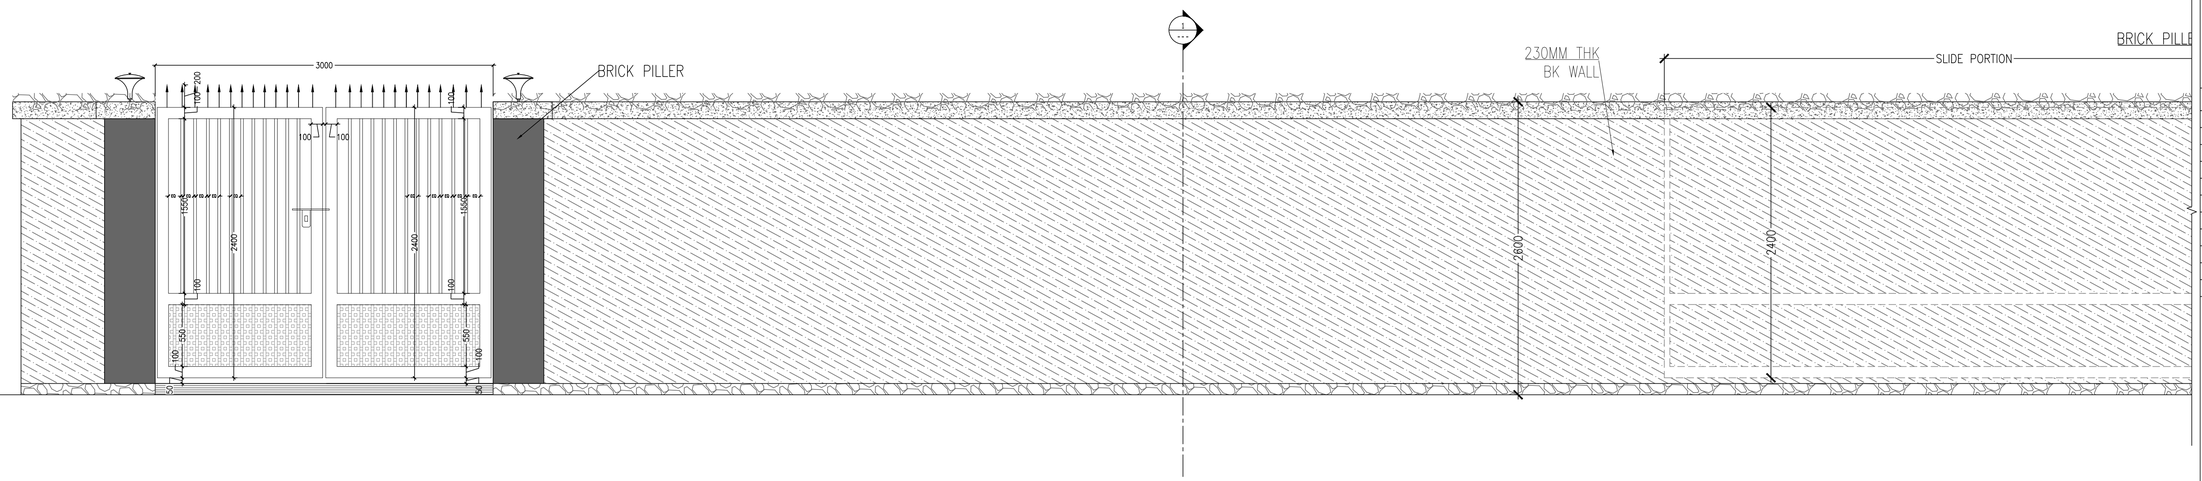


27 FRONT SIDE COMPOUND WALL ELEVATION (ENLARGE VIEW)

SCALE: 1:25

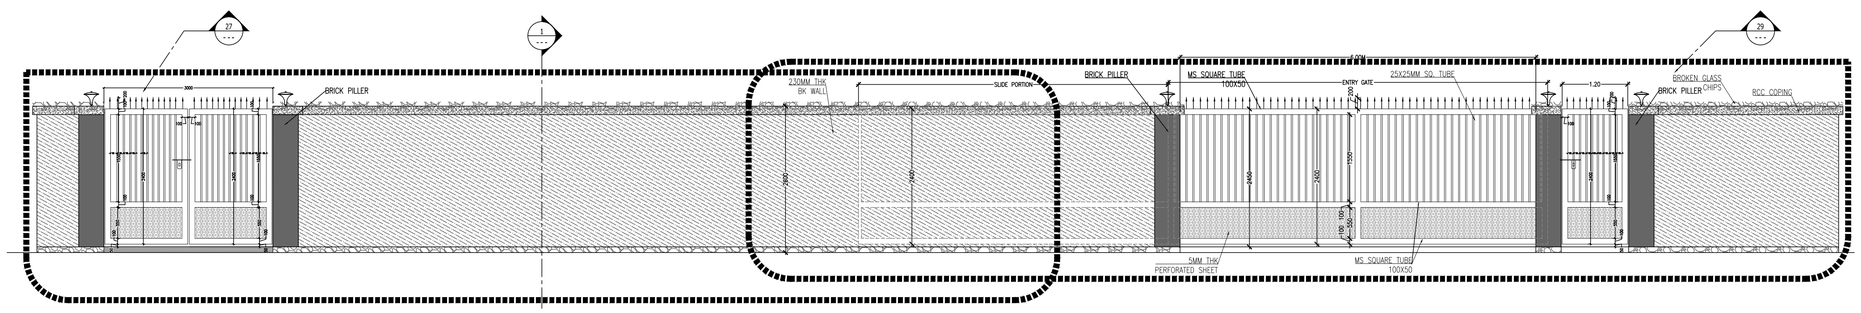

26 FRONT SIDE COMPOUND WALL ELEVATION

SCALE: 1:50

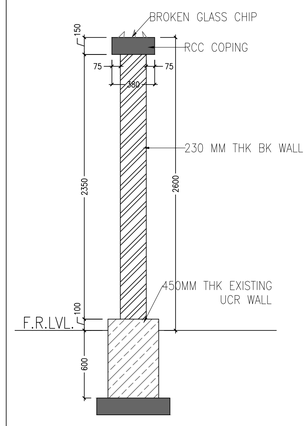

01 SECTION THROUGH COMPOUND WALL

SCALE: 1:25

ASTUTE™
ENGINEERING SERVICES PVT. LTD.

No.	Date	Revision/Issue
R0	25/09/2024	ORIGINAL ISSUE

GENERAL NOTES :

1. ANY DRAWING TO BE REFERRED AS A PART OF THE SET ONLY AND NOT IN ISOLATION.
2. ALL DIMENSIONS ARE IN MM,UNLESS MENTIONED OTHERWISE.
3. DO NOT SCALE FROM THIS DRAWING.
4. ALL DIMENSIONS TO BE VERIFIED ON SITE.
5. THIS DRAWING IS TO BE READ IN CONJUNCTION WITH RELEVANT ARCHITECTURAL, STRUCTURAL, M. E & P DRAWINGS AND SPECIFICATIONS. CONTRACTOR SHALL CO-ORDINATE THESE DRAWINGS AND REPORT ANY DISCREPANCY FOR CLARIFICATION BEFORE PROCEEDING WITH WORKS.
6. CONTRACTOR SHALL SUBMIT SHOP DRAWING FOR APPROVAL WHEREVER ESSENTIAL.
7. CONTRACTOR WILL BE RESPONSIBLE FOR THE CHECKING AND VERIFICATION OF ALL DIMENSIONS, SIZES AND TOLERANCES NEEDED FOR THE INSTALLATIONS OF ALL EQUIPMENT AND FITTINGS THOSE THAT ARE WITHIN THE SCOPE OF THE WORK OF THE CONTRACT AS WELL AS THOSE TO BE SUPPLIED BY OTHERS. THEREFORE ALL DIMENSIONS SHOWN ON DRAWINGS RELEVANT TO THESE INSTALLATION ARE FOR GUIDANCE ONLY.
8. LEVELS MENTIONED FOR LINTELS AT DOOR AND OPENINGS ARE FROM FINISHED FLOOR LEVEL.
9. ANY DISCREPANCY IN THE DRAWINGS/DIMENSIONS/SPECIFICATIONS SHALL BE BROUGHT TO THE NOTICE OF ENGINEER-IN-CHARGE FOR CLARIFICATION BEFORE EXECUTION OF THAT PART.
10. ALL CUTOUTS AND SLEEVES OF M.E.P. SERVICES MUST BE CLOSED AS PER METHOD SPECIFIED.
11. ALL OPENINGS DIMENSIONS SHOWN ARE STRUCTURAL OPENINGS UNLESS NOTED OTHERWISE.
12. ALL WET AREAS AND SHAFT FLOORING SHOULD HAVE WATER PROOFING LAYER AS PER SPECIFICATIONS.

SIGN. SEAL

Project Name

HODEK VIBRATION TECHNOLOGIES PVT LTD
BELUR INDUSTRIAL AREA,
TALUKA– DHARWAD, KARNATKA.

Sheet Title

FRONT SIDE COMPOUND WALL ELEVATION

Sheet Number

ARCH_WD_116_R0

Date	Scale	Drawn	Checked
25/09/2024	AS SHOWN	VILAS	S.M.

THIS DRAWING IS THE COPY RIGHT PROPERTY OF ASTUTE ESPL. ANY MISUSE, DUPLICATION, ALTERATION OR REUSE FOR ANOTHER PURPOSE IS STRICTLY PROHIBITED & SHALL BE DEALT LEGALLY.