

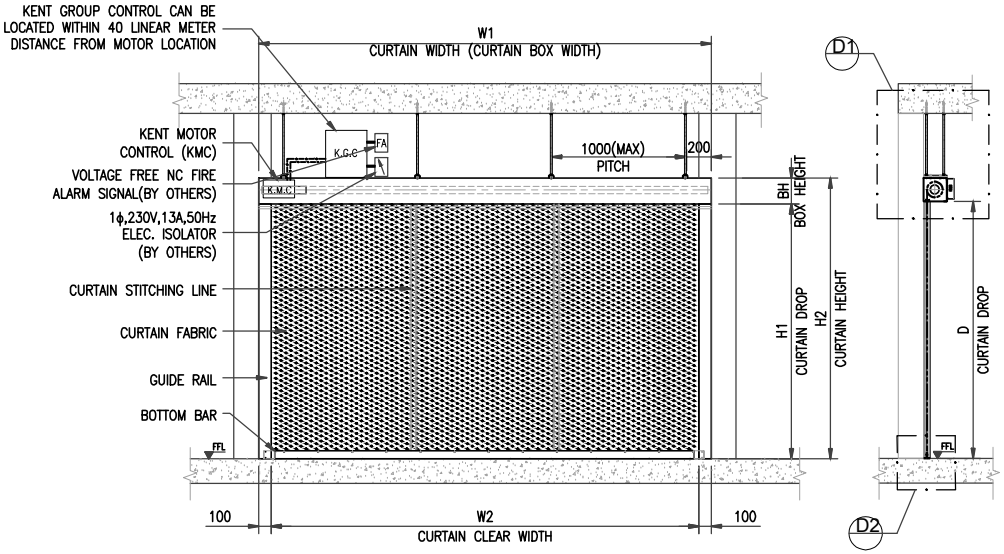


A ELEVATION
SCALE: NTS


B SECTION
SCALE: NTS

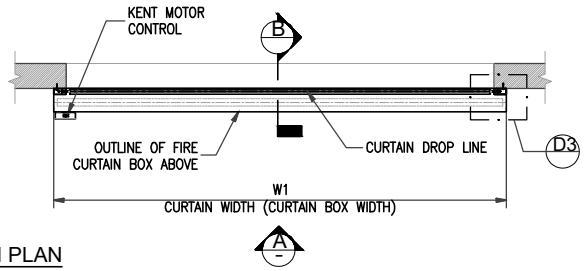


CURTAIN PLAN
SCALE: NTS

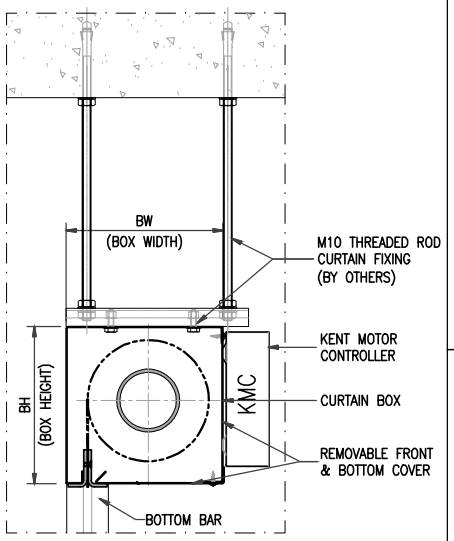

D1 ENLARGED DETAILS OF BOX CURTAIN
SCALE: NTS

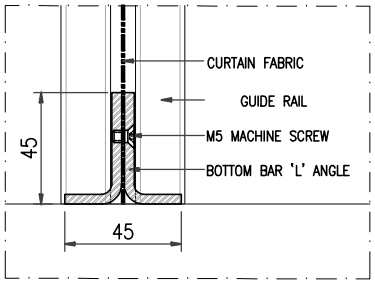

D2 ENLARGED DETAIL OF BOTTOM BAR
SCALE: NTS

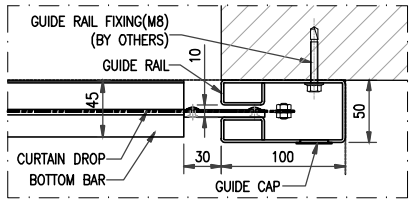

D3 ENLARGED DETAIL OF GUIDE RAIL
SCALE: NTS

FIRE CURTAIN SPECIFICATION:

CURTAIN	MANUFACTURED FROM WIRE REINFORCED, WOVEN GLASS FIBRE, FABRIC COATED ON EACH SIDE WITH POLYURETHANE (VWG-520)
BOTTOM BAR	45x23x4.7mm THK STEEL BOTTOM BAR POWDER COATED FINISH RAL TO BE CONFIRMED
BOX COVER	1.2mmTHK GALVANISED STEEL FINISH POWDER COATED FINISH RAL TO BE CONFIRMED
END PLATE	3mmTHK GALVANISED STEEL END PLATES AND BRACKETS
GUIDE RAIL	2mmTHK GALVANISED STEEL POWDER COATED FINISH RAL TO BE CONFIRMED
MOTOR	INTERNAL, ELECTRIC, TUBULER GEARED CONSTANT SPEED MOTOR
POWER SUPPLY	SINGLE PHASE, 230V,5A MIN,50Hz
FIRE ALARM SIGNAL	VOLTAGE FREE N.C SIGNAL

2HRS FIRE RATED FIRE CURTAIN - SCHEDULE

				CURTAIN WIDTH		CURTAIN HEIGHT		CURTAIN BOX SIZE		MOTOR LOCATION	FINISH	REMARKS
S.NO	SHUTTER REF.	LOCATION	QTY	W1	W2	H1	H2	BW	BH			
1	FC-1	–	1NO	4200	4000	4500	4710	210	210	LEFT	TBC	
2	FC-2	–	7NOS	3200	3000	4500	4710	210	210	LEFT	TBC	
3	FC-3	–	8NOS	2200	2000	4500	4710	210	210	LEFT	TBC	

NOTE:
ALL DIMENSIONS ARE IN MILLIMETRES UNLESS OTHERWISE STATED.

Rev.	Date	By	Description	Checked	Approved
0	19.10.2024		FOR APPROVAL		

ROHAN BUILDERS (INDIA) PVT LTD

NIHVA Technologies PVT Ltd

Designed	Checked	Approved
MTK		
Scale N.T.S	Drawn MTK	Date 19.10.2024

Project Title : PEPSI CO MP

Drawing Title : 2HRS FIRE CURTAIN PLAN, ELEVATION, SECTION & DETAILS

Drawing No. : FER-NTP-FC-SD-001 | Rev. 00 | Sheet 1 of 1

CAD File Name :FER-NTP-FC-SD-001_0.dwg | A3