


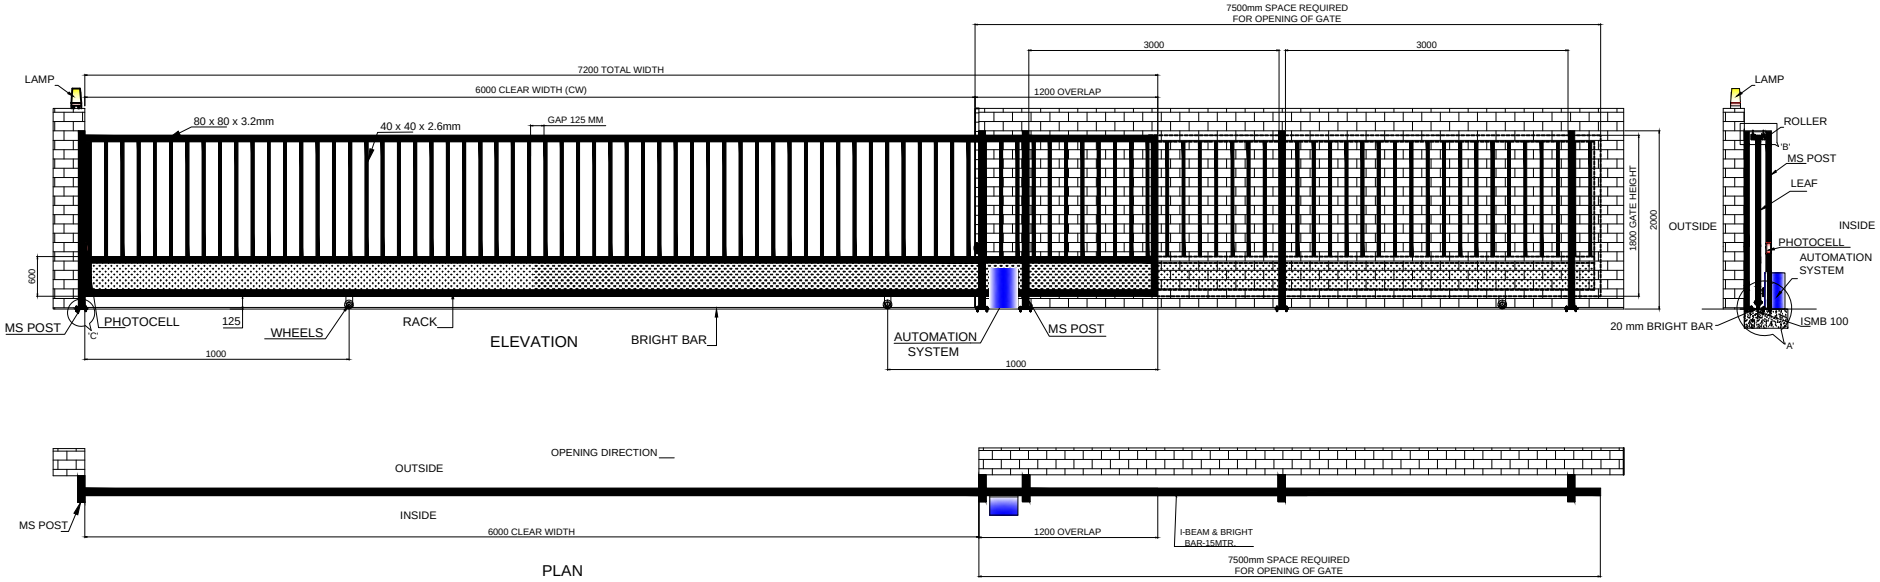


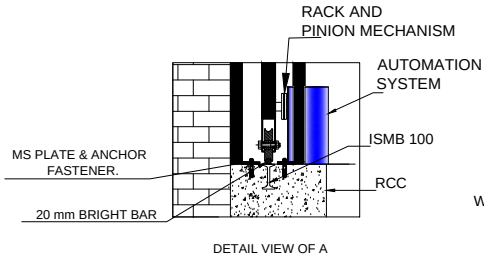

DETAIL VIEW OF A

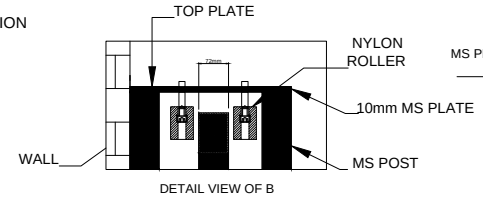

DETAIL VIEW OF B

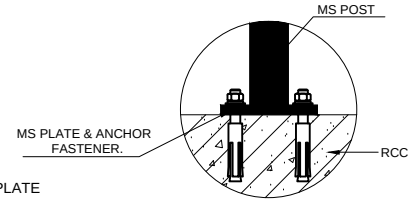

DETAIL VIEW OF C
(FIXING DETAILS)

SR NO	DATE	DRAWN	REMARK
R03	03.10.19	P.V.A	CLEAR WIDTH CHANGE
R02	03.10.19	P.V.A	PARKING DETAILS ADD
R01	03.10.19	P.V.A	CLIENT NAME CHANGE

This drawing & designing is the property of NIHVA TECHNOLOGIES. Not be sold or copy to any other concern.

TITLE
MOTORIZED SLIDING GATE

NIHVA
NIHVA TECHNOLOGIES PVT. LTD.

NIHVA TECHNOLOGY
PVT. LTD. PUNE
Tel : 020 66304033
Email:- info@nihva.com
Website:- www.nihva.com

	NAME	SIGN	DATE
DRAWN	P.V.A		26.09.2019
CHECK	G.J		26.09.2019
APPROVAL			

CLIENT - ASHOK CONSTRUCTION
PROJECT - JOHN DEERE
SITE LOCATION - RANJANGAON
DWG. NO. : NIHVA/19-20/0105/R03 REV: R03
If any queries contact : projects@nihva.com
SCALE: 01 WT: SHEET: 01 OF 01
ALL DIMENSION ARE IN mm