Revision		Date	By
A	Door measurements changed	2019-02-12	EB

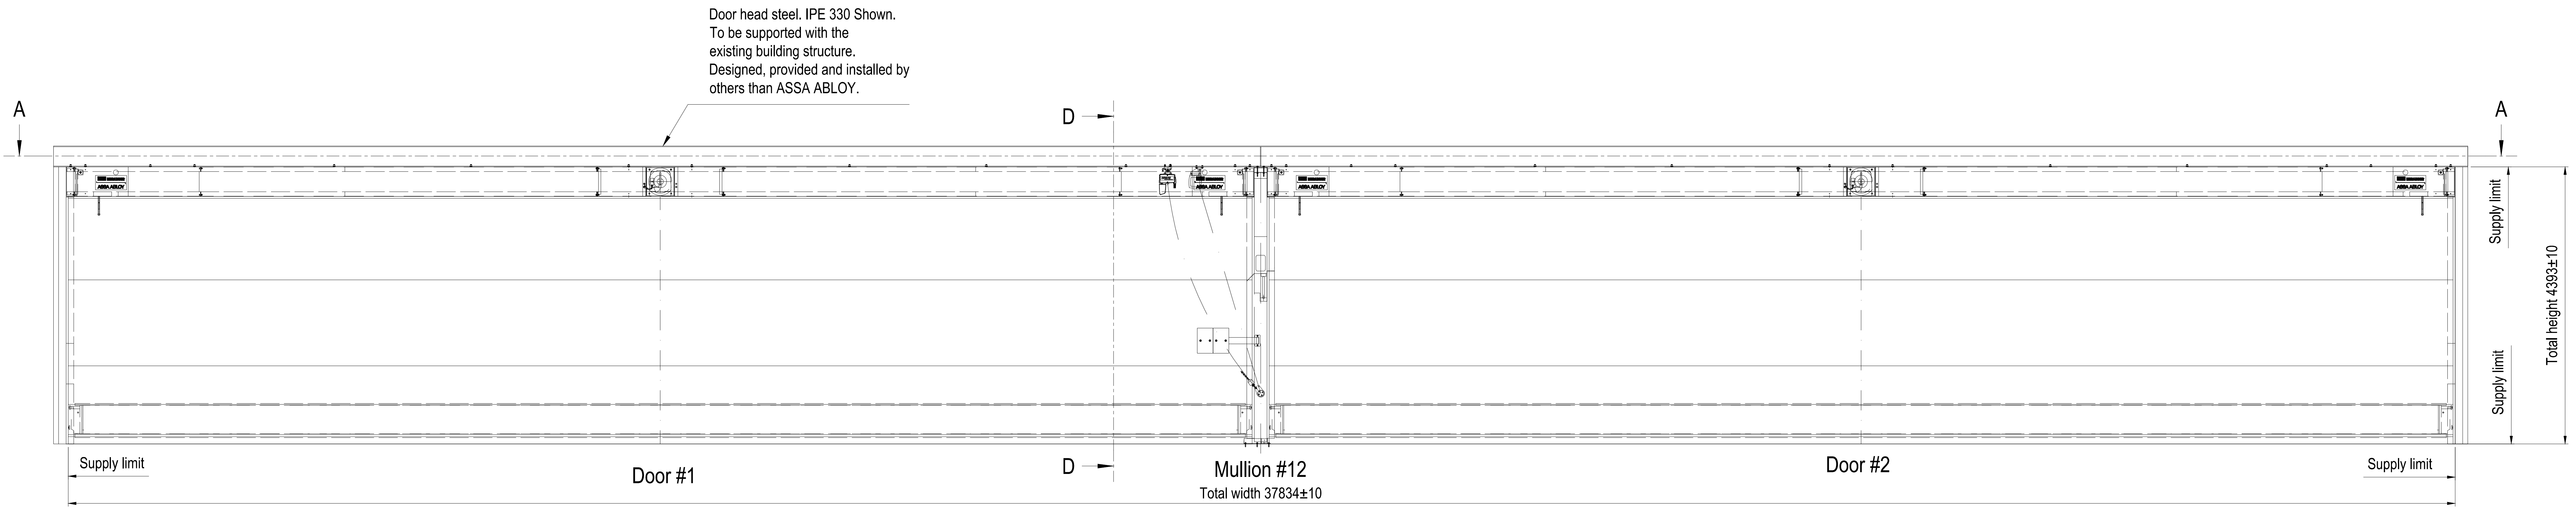

Interior view, Door closed

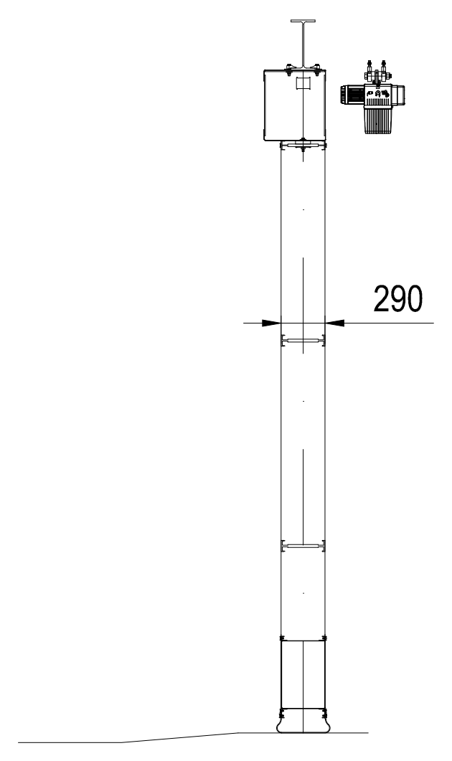

SECTION D-D

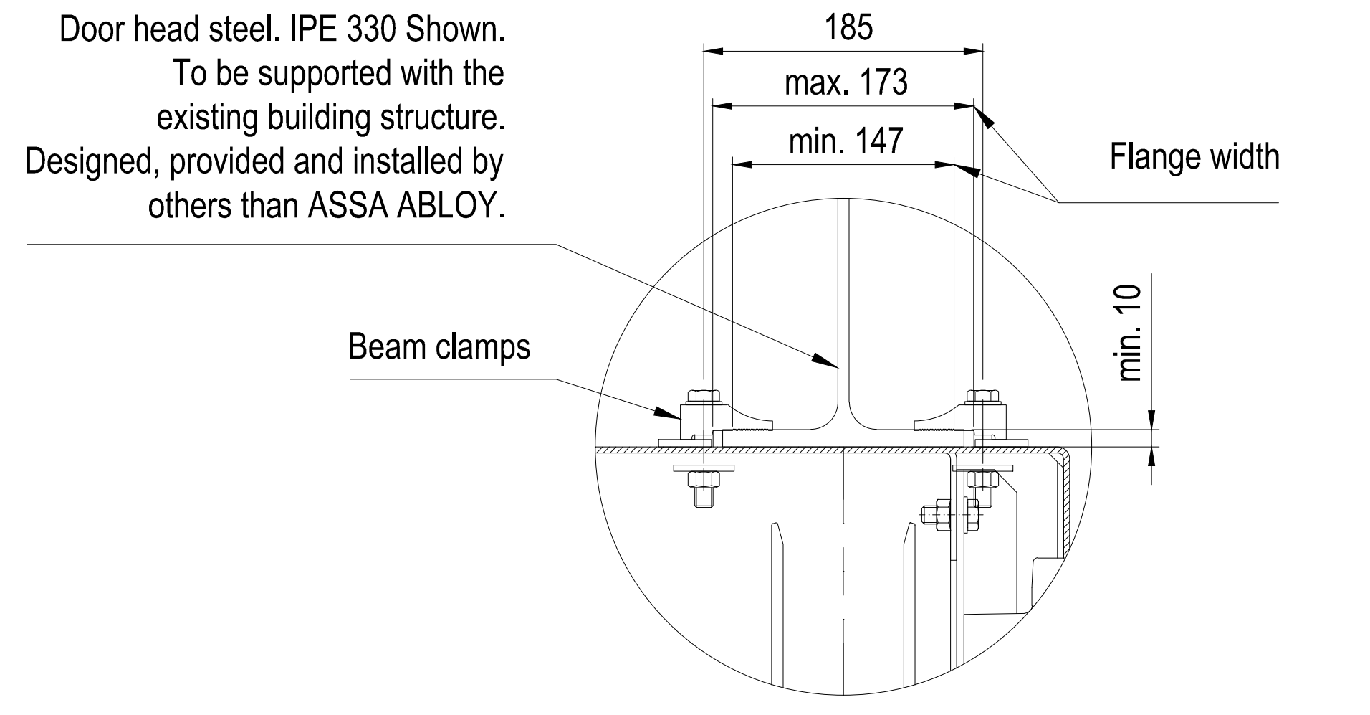

DETAIL A, SCALE (1:5)

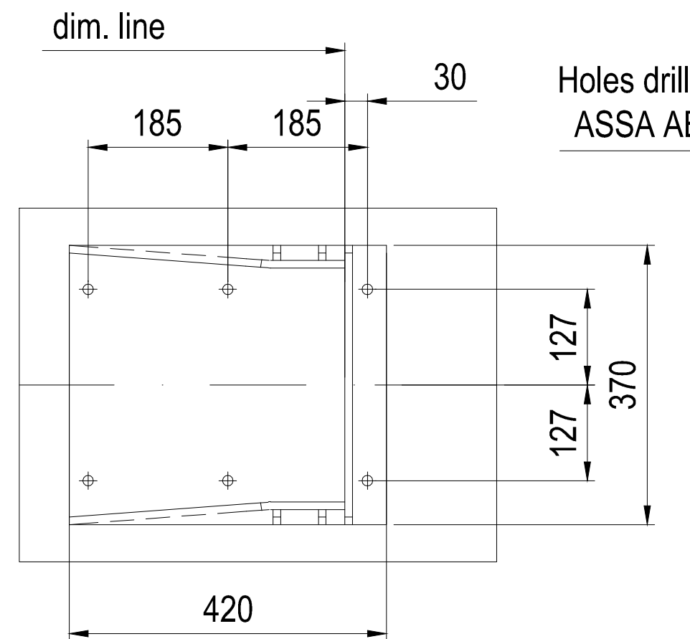

DETAIL E, SCALE (1:10)

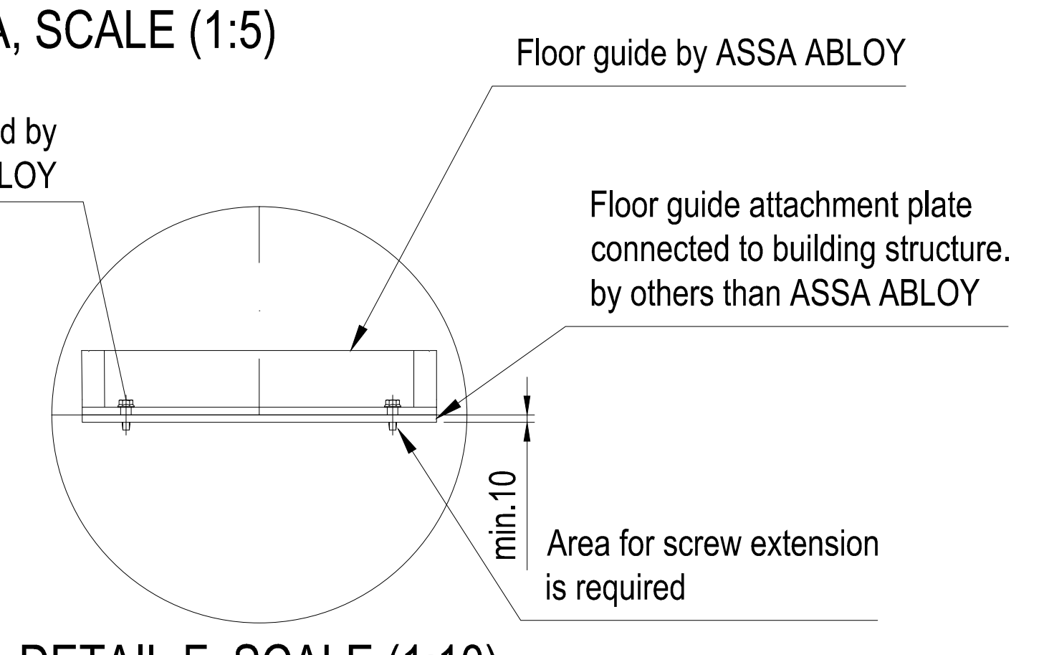
Floor guide by ASSA ABLOY
Holes drilled by
ASSA ABLOY
Floor guide attachment plate
connected to building structure.
by others than ASSA ABLOY
min.10
Area for screw extension
is required

DETAIL F, SCALE (1:10)

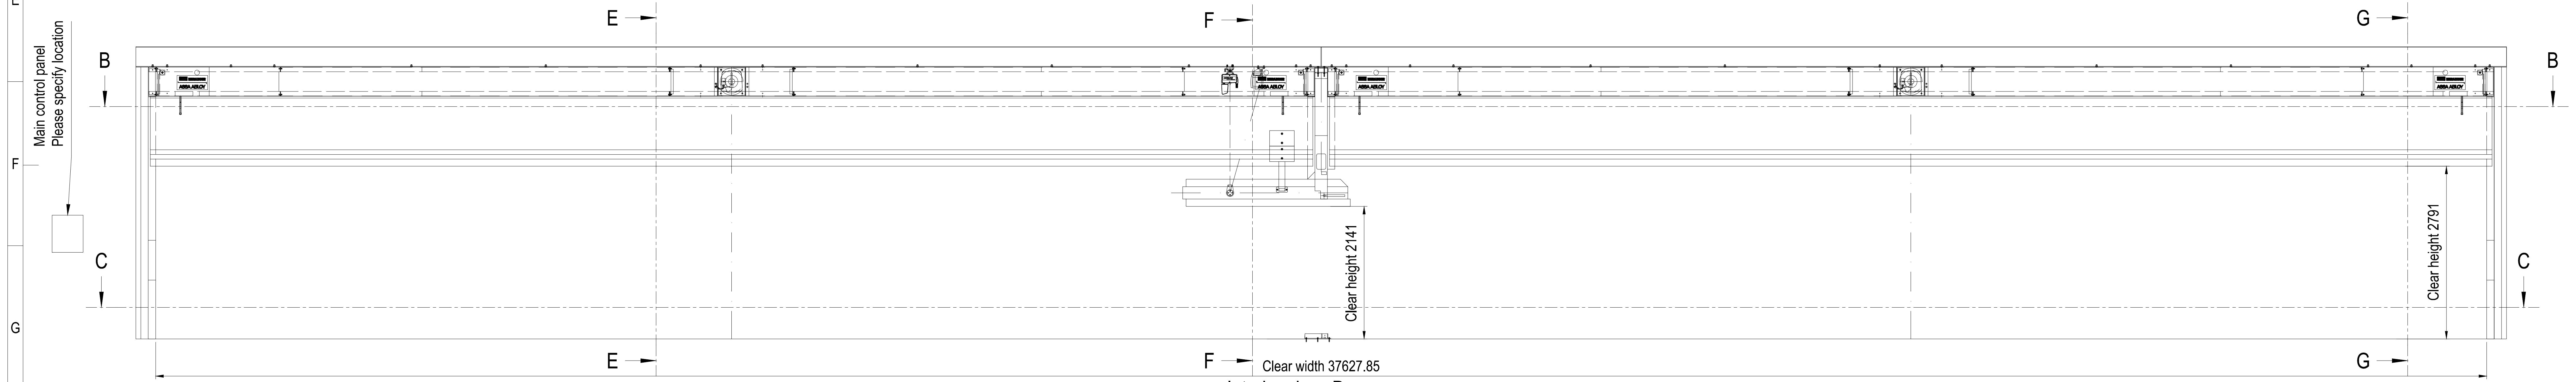

Interior view, Door open

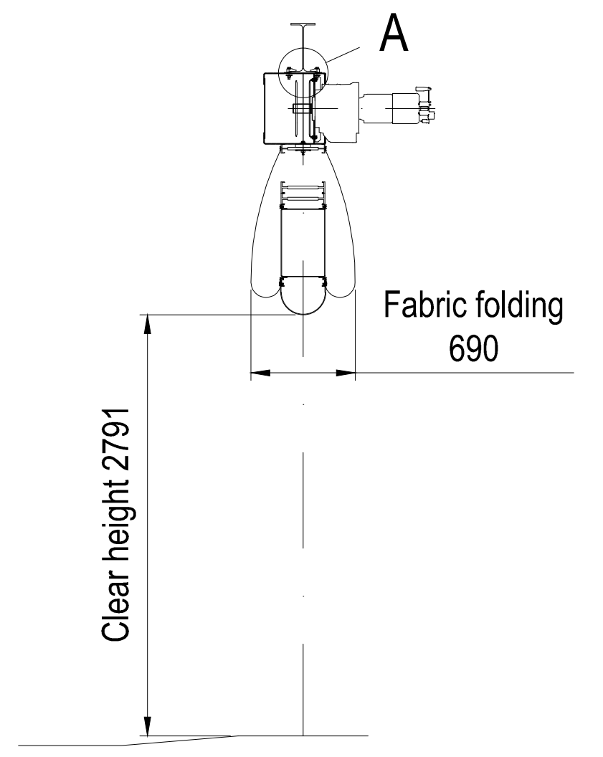

SECTION E-E

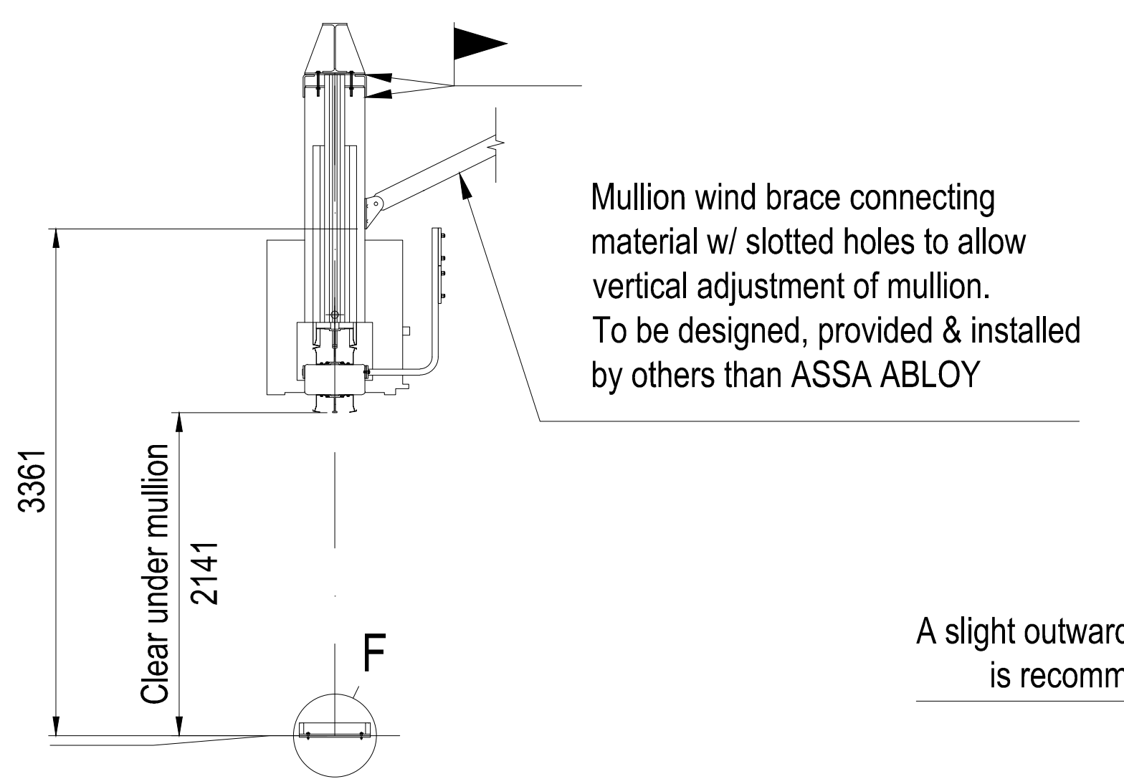
Mullion wind brace connecting
material w/ slotted holes to allow
vertical adjustment of mullion.
To be designed, provided & installed
by others than ASSA ABLOY
3361
Clear under mullion
2141
F

SECTION F-F
Header box & door leaf not shown

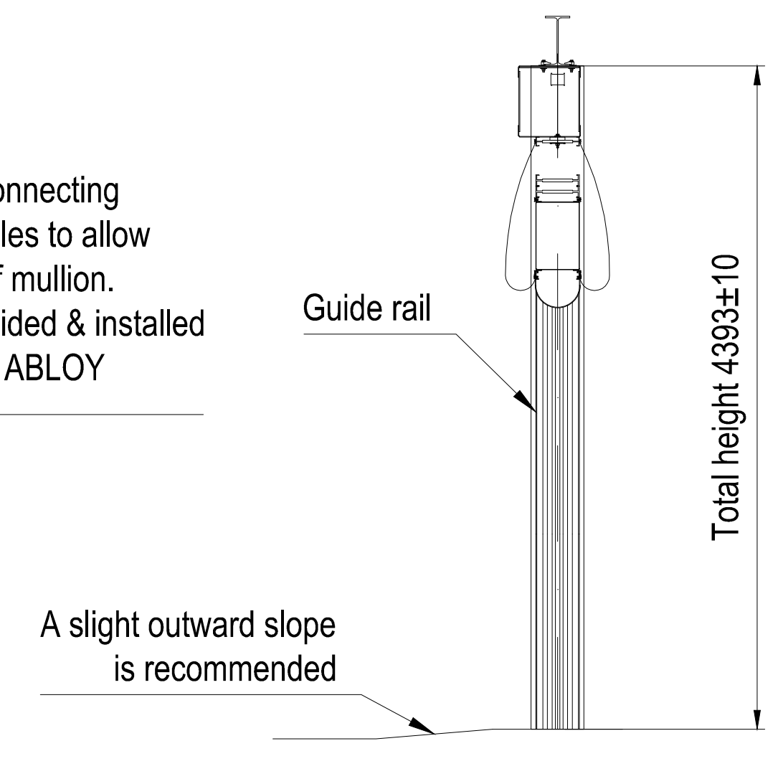

SECTION G-G

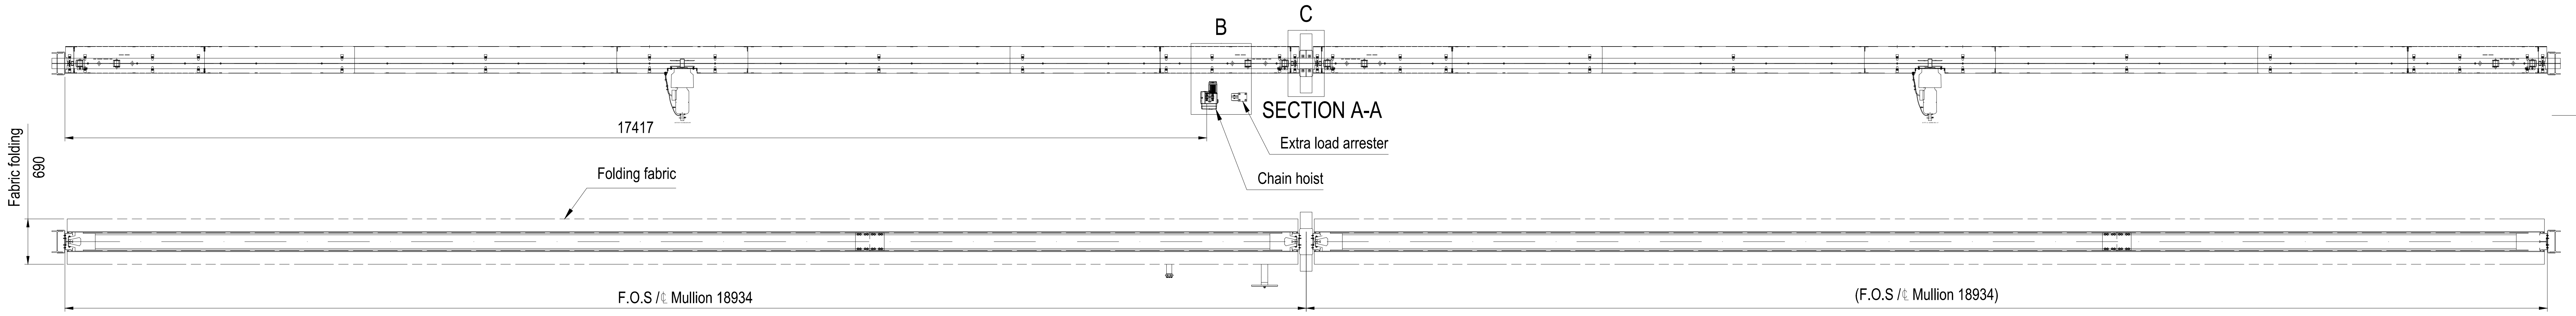

SECTION A-A

SECTION B-B

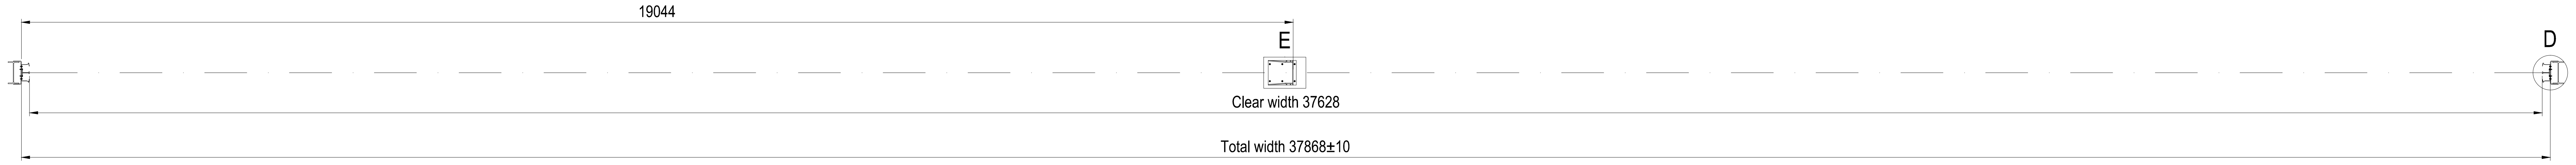

SECTION C-C

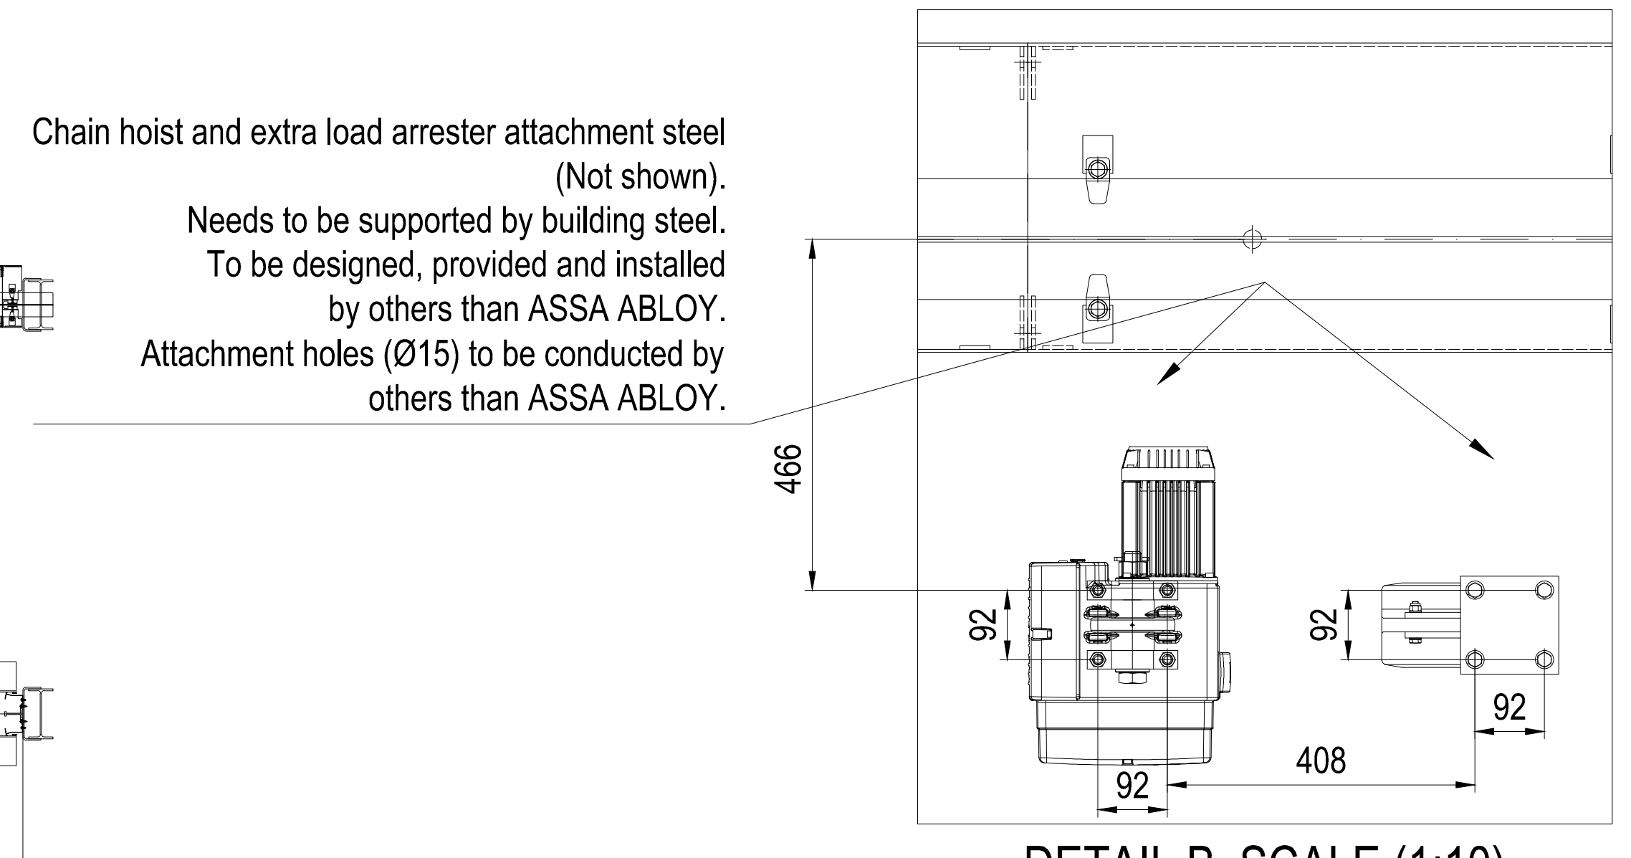
Chain hoist and extra load arrester attachment steel
(Not shown).
Needs to be supported by building steel.
To be designed, provided and installed
by others than ASSA ABLOY.
Attachment holes (Ø15) to be conducted by
others than ASSA ABLOY.
466
92
92
92
408
92

DETAIL B, SCALE (1:10)

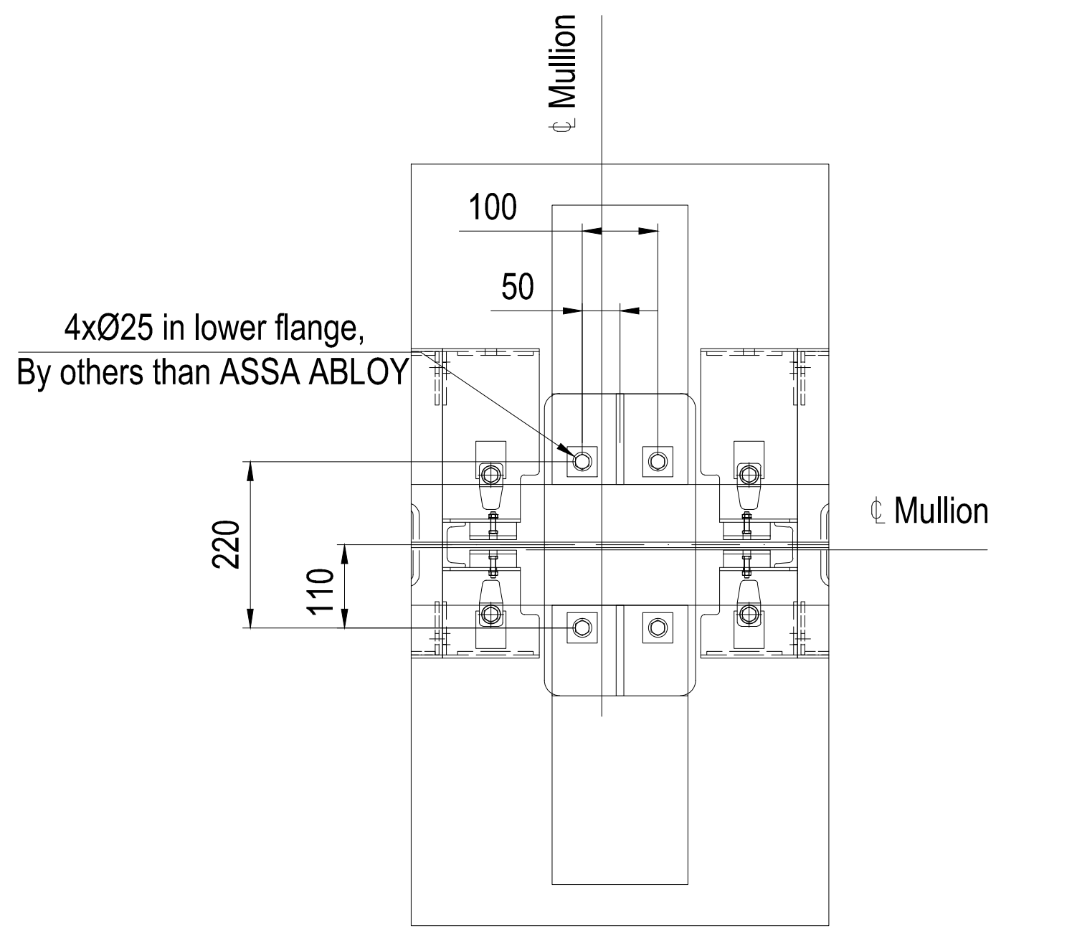

DETAIL C, SCALE (1:10)

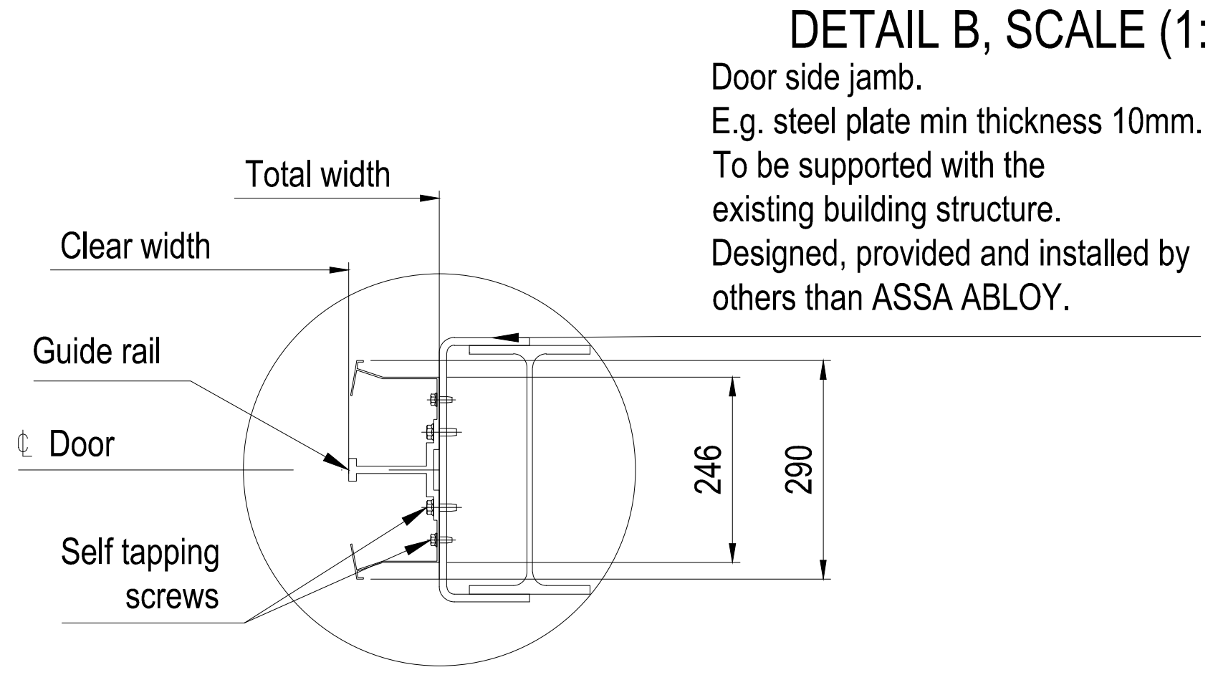

DETAIL D, SCALE (1:10)

DOOR IDENTITY NUMBER: 84384001

LOAD DIAGRAM & NOTES, ref. to drwng. no. 68128

DESIGNED
EB
SIZE A1F
SCALE 1:50
CODE
84384
ITEM NO
DATE
2019-02-05
ASSA ABLOY

If not otherwise stated:
Tolerances
ISO 2768-m
EN ISO 13920-B
Cutting class
ISO 9013-442
Weld class
ISO 5817-C
Surface finish
Smooth raw surface

NVIDIA Phase 2
India
Megadoor 37628 x 2791/2141
Interface

PLOT DATE
DRAWING NO
68127
REVISION
A

This document is the property of ASSA ABLOY Entrance Systems AB and shall not without our written permission be copied, imparted to a third party or used for any other unauthorized purpose.