


Pg~1 of 2

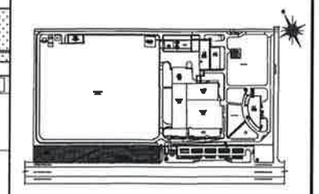


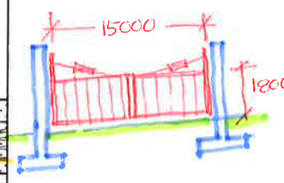

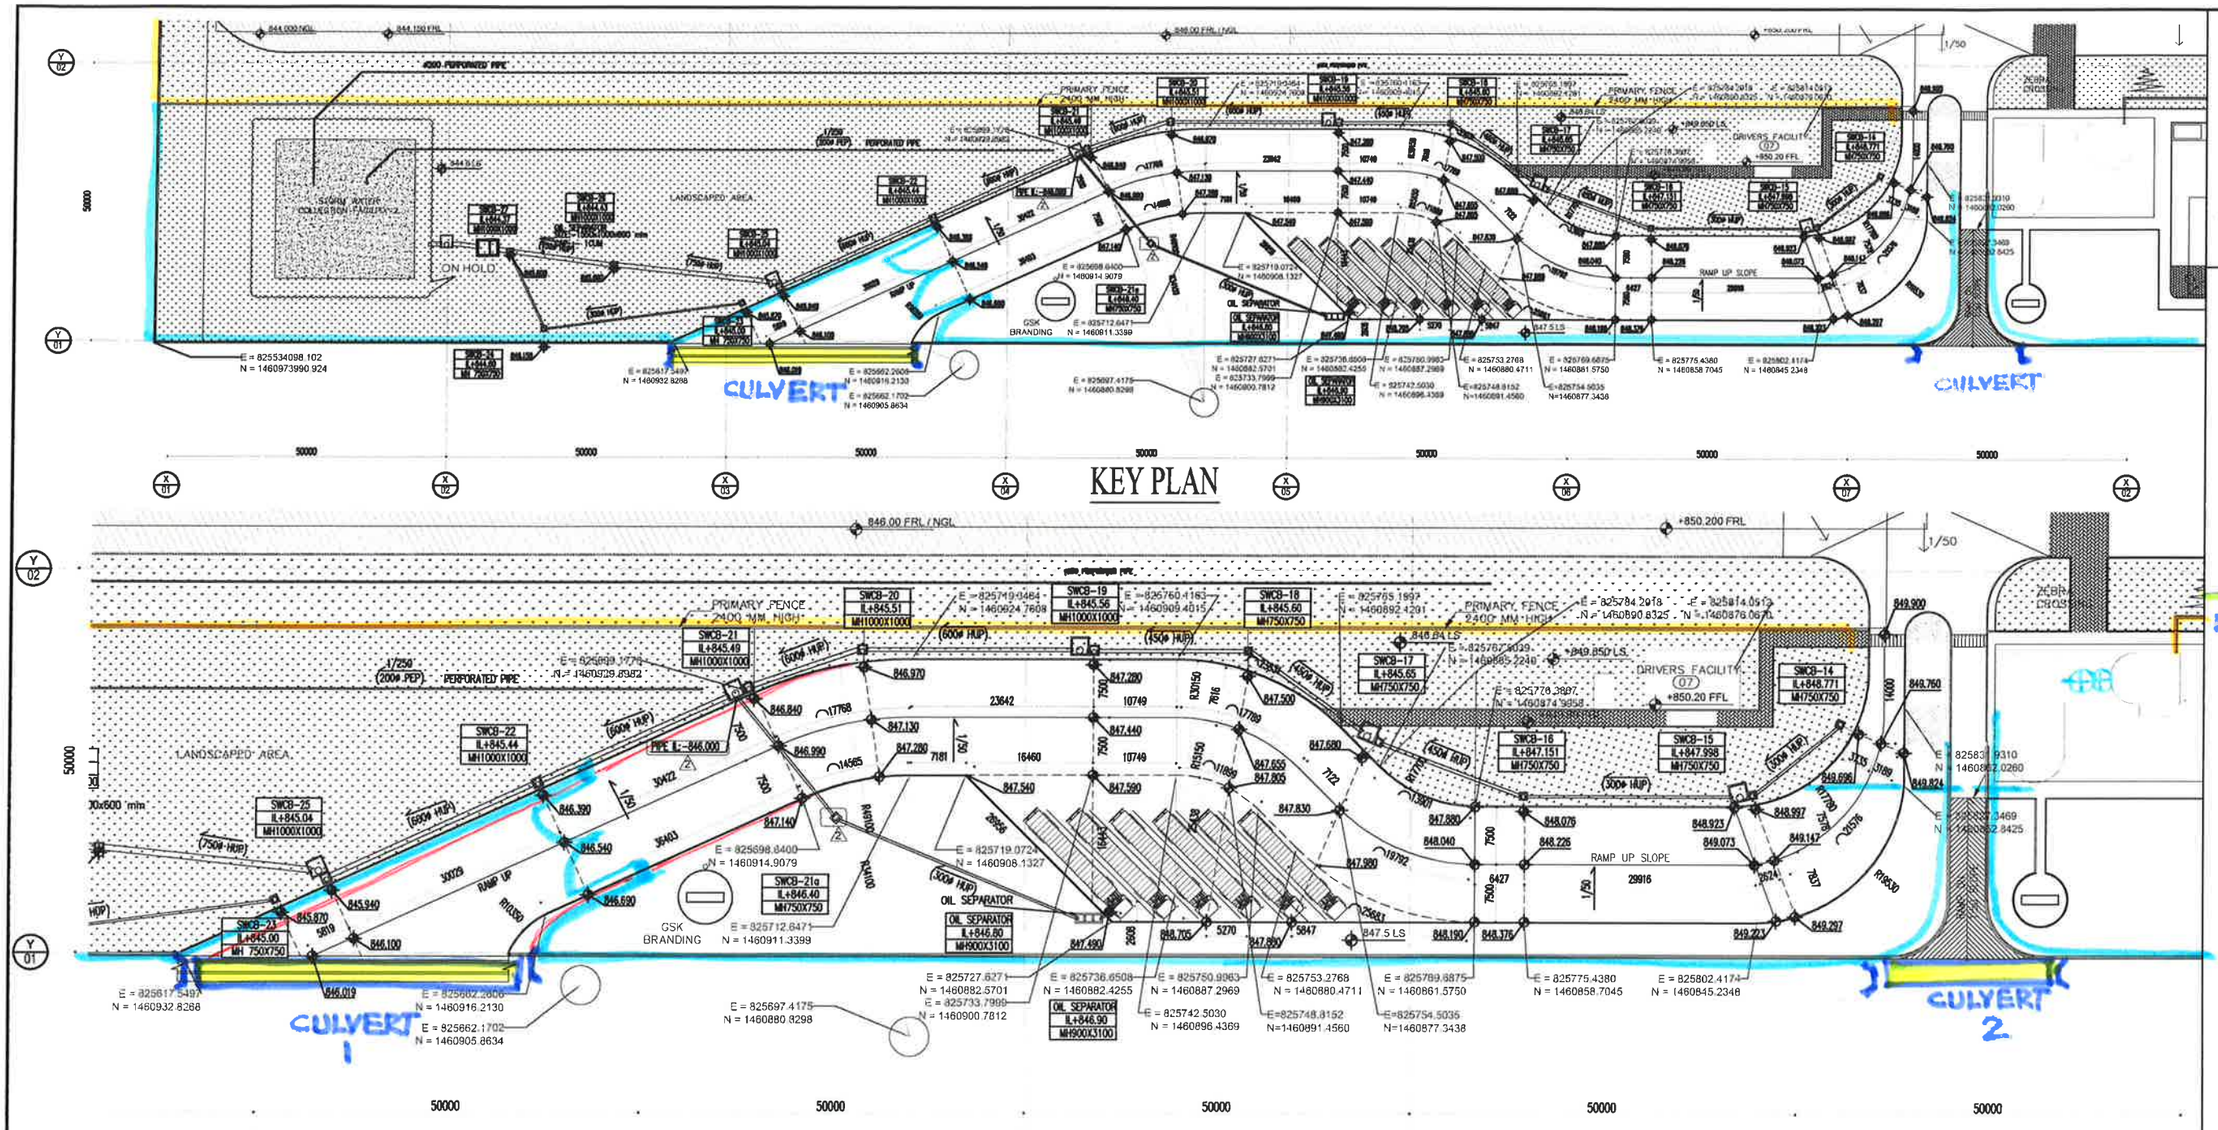

KEY PLAN

ROAD PLAN

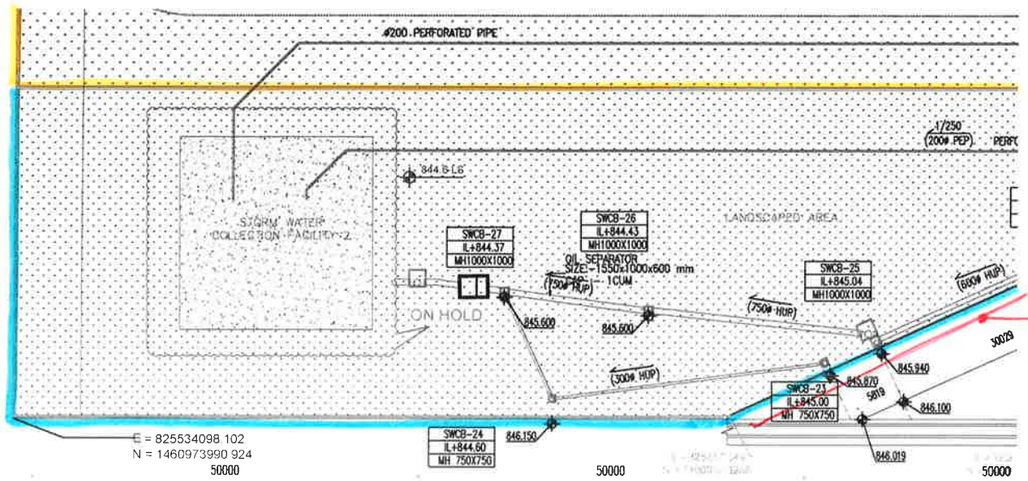

ROAD PLAN

NEED TO SHIFT ROAD LINE TO ACCOMMODATE BOUNDARY FENCE & GATE COLLUMN.

CHANGES / MODIFY:

(1) 15m SWING GATE TO BE ADDED AT TRUCK ENTRY (MANUAL)
(2) BOUNDARY WALL LENGTH MODIFY – INCREASE
(3) SECONDARY FENCE GRILL HT INCREASE TO 1200 mm
(4) CULVERT ADDED TO ENTRY / EXIT GATE.
(5) ROAD TO BE ADJUSTED.

DISCUSSED WITH MR. STEVEN
07/SEP/2016

REV.	DATE	DESCRIPTION	DRWN	CHKD
2	23.08.2016	REVISION	V.K.	M.D.
1	20.08.2016	REVISION	V.K.	M.D.
0	28.06.2016	FOR CONSTRUCTION	V.K.	M.D.

PROJECT TITLE:
NEW ORAL SOLID DOSE FACILITY
Bangalore

FOR CONSTRUCTION


DESIGN AND BUILT:
SHIMIZU CORPORATION
SHIMZ

DRAWING TITLE:
EXTERNAL AREA
SOUTH ROAD PLAN DETAIL
PART 1 of 1


SCALE:	DATE:	DRAWN BY:	CHECKED BY:
1:- @ A1	23.08.2016	VISHAL.K	AKASH.K

PROJECT : GSK
DRAWING NO. GSK-S-CBP-EXT-ROAD-PL-01
REV. 2

Pg~2 of 2

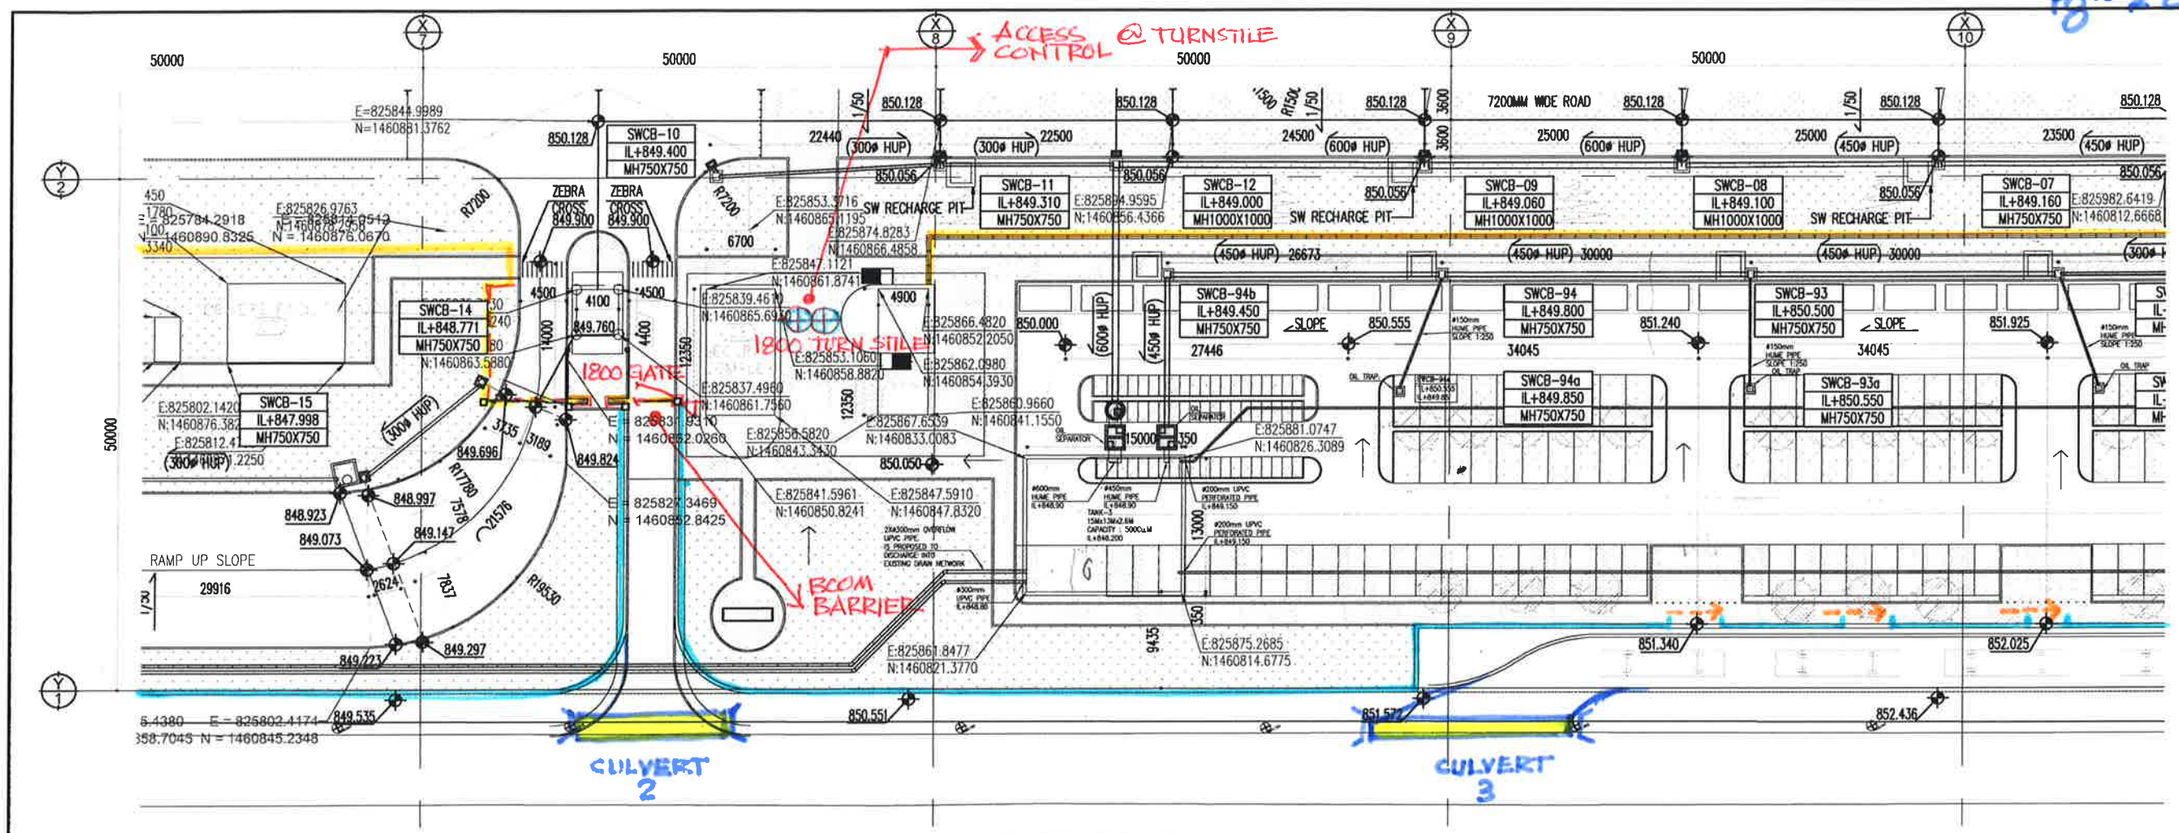


X1 ROAD PLAN

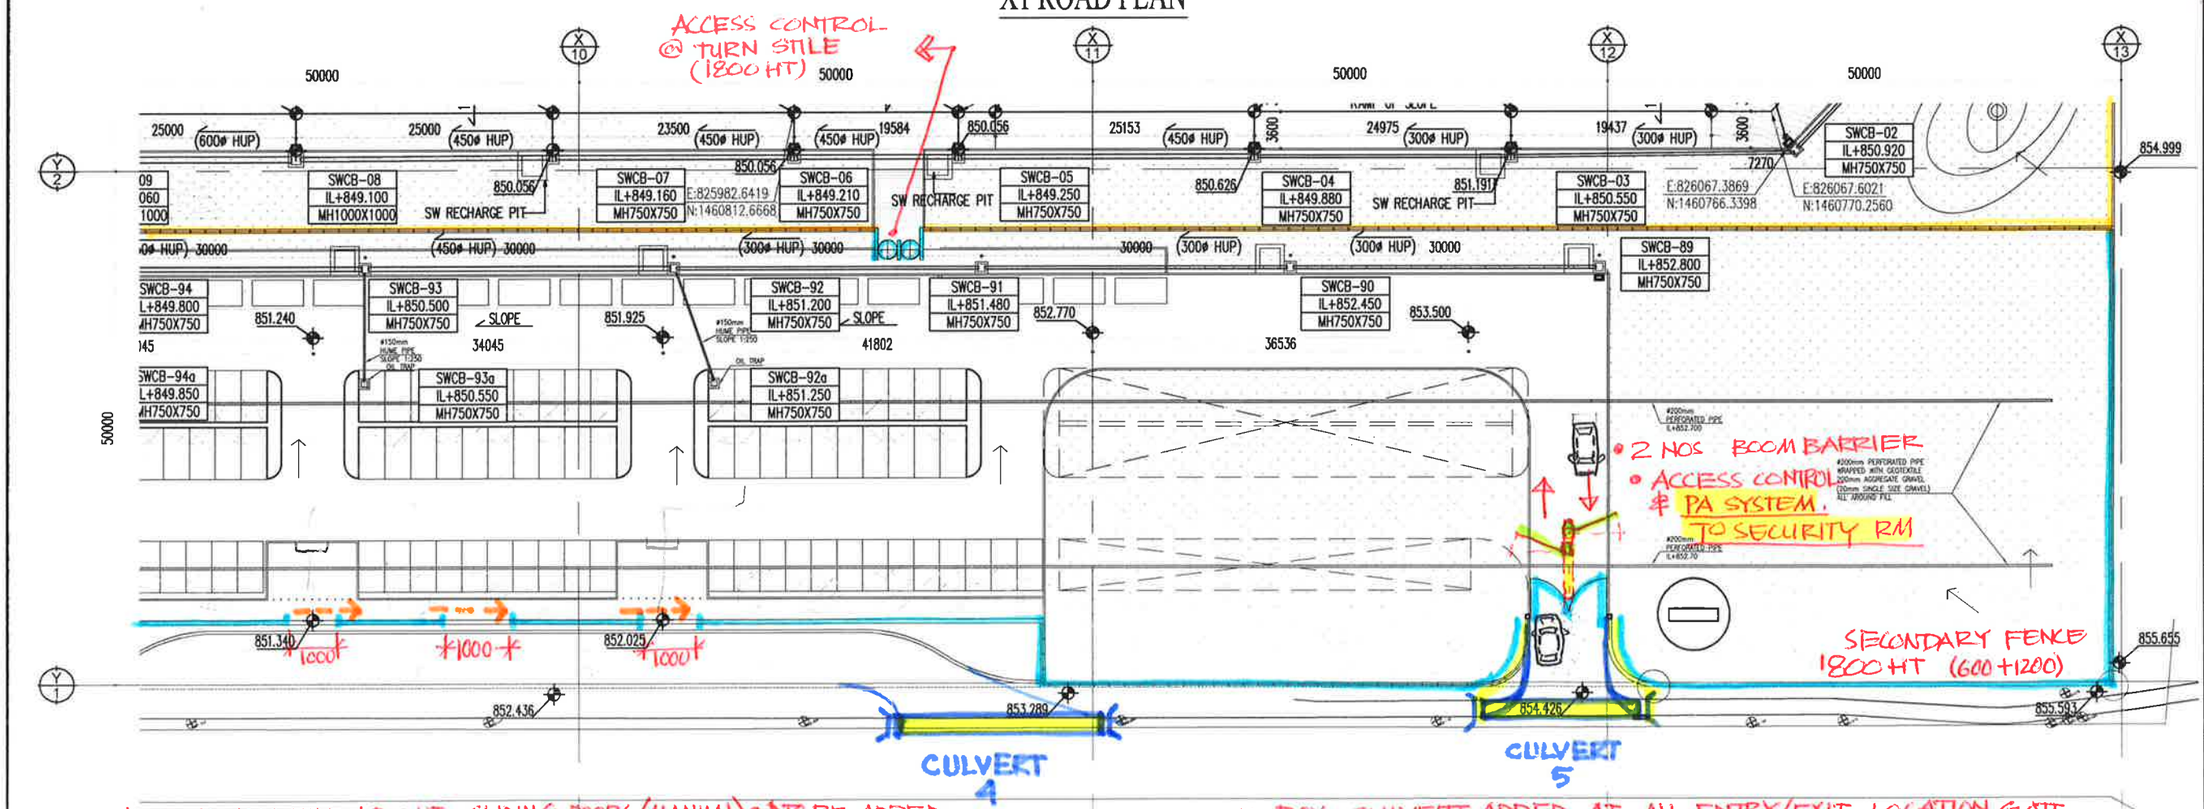

X1 ROAD PLAN

* 3 NO. 1000 WIDE 1800 HT SLIDING DOORS (MANUAL) → TO BE ADDED

* BOX CULVERT ADDED AT ALL ENTRY/EXIT LOCATION GATE WITH METAL CATTLE TRAP.

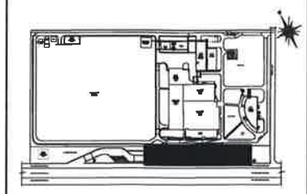

NOTES/INFORMATION :-

- MEDIUM DUTY PAVER 80mm PAVER (M40)
- RAMP AREA
- WALKABLE PAVER 60mm PAVER (M40)
- LANDSCAPE AREA
- STORM WATER LINE

* TURNSTILES 1800HT

* SECONDARY FENCE = 1800 HT (1200 GRILL)

REV.	DATE	DESCRIPTION	DRWN	CHKD
0	24.08.2016	FOR CONSTRUCTION	V.K.	M.D.

PROJECT TITLE:
NEW ORAL SOLID DOSE FACILITY
Bangalore

FOR CONSTRUCTION

DESIGN AND BUILT:
SHIMIZU CORPORATION
SHIMZ

DRAWING TITLE:
EXTERNAL AREA
X1 ROAD PLAN DETAIL
PART 1 of 1

SCALE:	DATE:	DRAWN BY:	CHECKED BY:
2:- @ A2	24.08.2016	VISHAL.K	AKASH.K

PROJECT :	DRAWING NO.	REV.
GSK	GSK-S-CBP-EXT-ROAD-PL-13	0